



ИП Голенкова Анна Владимировна
ИНН 910300016034 ОГРНИП 314910223200051
р/с 40802810642680100764 в РНКБ Банк (ПАО)
корр. счет №30101810335100000607, БИК 043510607
Юр. адрес: 298612, Республика Крым, г. Ялта, ул. Ореховая, 31/1/31
Факт. Адрес: 298612, Республика Крым, г. Ялта, ул. Московская, 43, офис 5
тел.: +7 978 750 47 55; +7 978 053-12-42

САМОРЕГУЛИРУЕМАЯ ОРГАНИЗАЦИЯ АССОЦИАЦИЯ
"МЕЖРЕГИОНАЛЬНОЕ ОБЪЕДИНЕНИЕ ПРОЕКТНЫХ ОРГАНИЗАЦИЙ"
СРО-П-014-05082009 Рег.№ 767-18 от 06.07.2018г.

Заказчик: **КОСЯКОВ А.Н.**

ИНДИВИДУАЛЬНЫЙ ЖИЛОЙ ДОМ, ПО АДРЕСУ:
РЕСПУБЛИКА КРЫМ, МУНИЦИПАЛЬНОЕ ОБРАЗОВАНИЕ
ГОРОДСКОЙ ОКРУГ АЛУШТА, п. РОЗОВЫЙ

РАБОЧАЯ ДОКУМЕНТАЦИЯ

Архитектурные решения

02-2019-АР

Главный инженер проекта

Голенкова А.В.

2019

Согласовано			
Взам. инв. №			
Подпись, Дата			
Инв. № подл.			

Согласовано

Взам. инв. №

Подпись. Дата

Инв. № подл.

Ведомость чертежей комплекта		
лист №	Наименование	Примечания
1	Общие данные.	
2	План на отм. 0,000. М 1:100	
3	План на отм. 0,000 с обозначением проемов и типов полов . М 1:100	
4	План чердака на отм. 3,100. М 1:100	
5	План чердака на отм. 4,100. М 1:100	
6	План кровли. М 1:100	
7	Разрез 1-1. М 1:100	
8	Разрез 2-2. М 1:100	
9	Разрез 3-3. М 1:100	
10	Разрез 4-4. М 1:100	
11	Разрез 5-5. М 1:100	
12	Разрез 6-6. М 1:100	
13	Узлы и детали (начало)	
14	Узлы и детали (окончание)	
15	Фасад в осях 1-4. М 1:100	
16	Фасад в осях 4-1. М 1:100	
17	Фасад в осях А-Г. М 1:100	
18	Фасад в осях Г-А. М 1:100	
19	Элементы пола	
20	Эскизы заполнения оконных и дверных проемов (начало). Спецификация	
21	Эскизы заполнения оконных и дверных проемов (окончание). Спецификация	
22	Отделка фасадов (общий вид)	
23	Отделка фасадов (общий вид)	
24	Отделка фасадов (общий вид)	
25	Отделка фасадов (общий вид)	
26	Ведомость наружной отделки	

Технические решения, принятые в рабочих чертежах, соответствуют требованиям экологических, санитарно-гигиенических, противопожарных и других норм, действующих на территории Российской Федерации, и обеспечивают безопасную для жизни и здоровья людей эксплуатацию объекта при соблюдении предусмотренных рабочими чертежами мероприятий.
Главный инженер проекта
А.В. Голенкова


Ведомость ссылочных документов		
Лист	Наименование	Примечание
	Ссылочные документы	
ГОСТ Р 21.1101-2013	Система проектной документации для	
	строительства. Основные требования	
	к проектной и рабочей документации.	
ГОСТ 27751-2014	Надежность строительных конструкций и	
	оснований.	
	Основные положения и требования.	
СП 14.13330.2011	Строительство в сейсмических районах.	
СНиП 21-01-97*	Пожарная безопасность зданий и сооружений.	
СНиП 31-02-2001	Дома жилые многоквартирные	
№190-ФЗ с изм. от 27.12.2018г.	Градостроительный кодекс РФ	
СП 15.13330.2012	Каменные и армокаменные конструкции.	
СНиП 2.01.01-82	Строительная климатология и геофизика	

Примечание.
За относительную отметку 0,000 принят уровень чистого пола первого этажа, что соответствует абсолютной отметке 224,05 м над уровнем моря.

Архитектурно-строительную часть проекта разработано для следующих условий строительства:
- климатический район строительства - IV Б
- средняя температура наружного воздуха наиболее холодных суток -6С
- снеговой район I - Р=1000 кПа
- ветровой район III - Р=500 кПа
Класс ответственности здания - III
Степень огнестойкости - I
Сейсмичность площадки - 8 баллов

						02 - 2019 - АР			
						Индивидуальный жилой дом, по адресу: Республика Крым, Муниципальное образование городской округ Алушта, п. Розовый			
Изм.	Кол.	Лист	№ док.	Подпись	Дата	Индивидуальный жилой дом	Стадия	Лист	Листов
							Р	1	
ГИП		Голенкова					Общие данные		Индивидуальный Предприниматель Голенкова А.В. ОГРНИП 314910223200051
Разработ.		Гемдицкий							
Н. контр.		Коломиец							

Формат А3

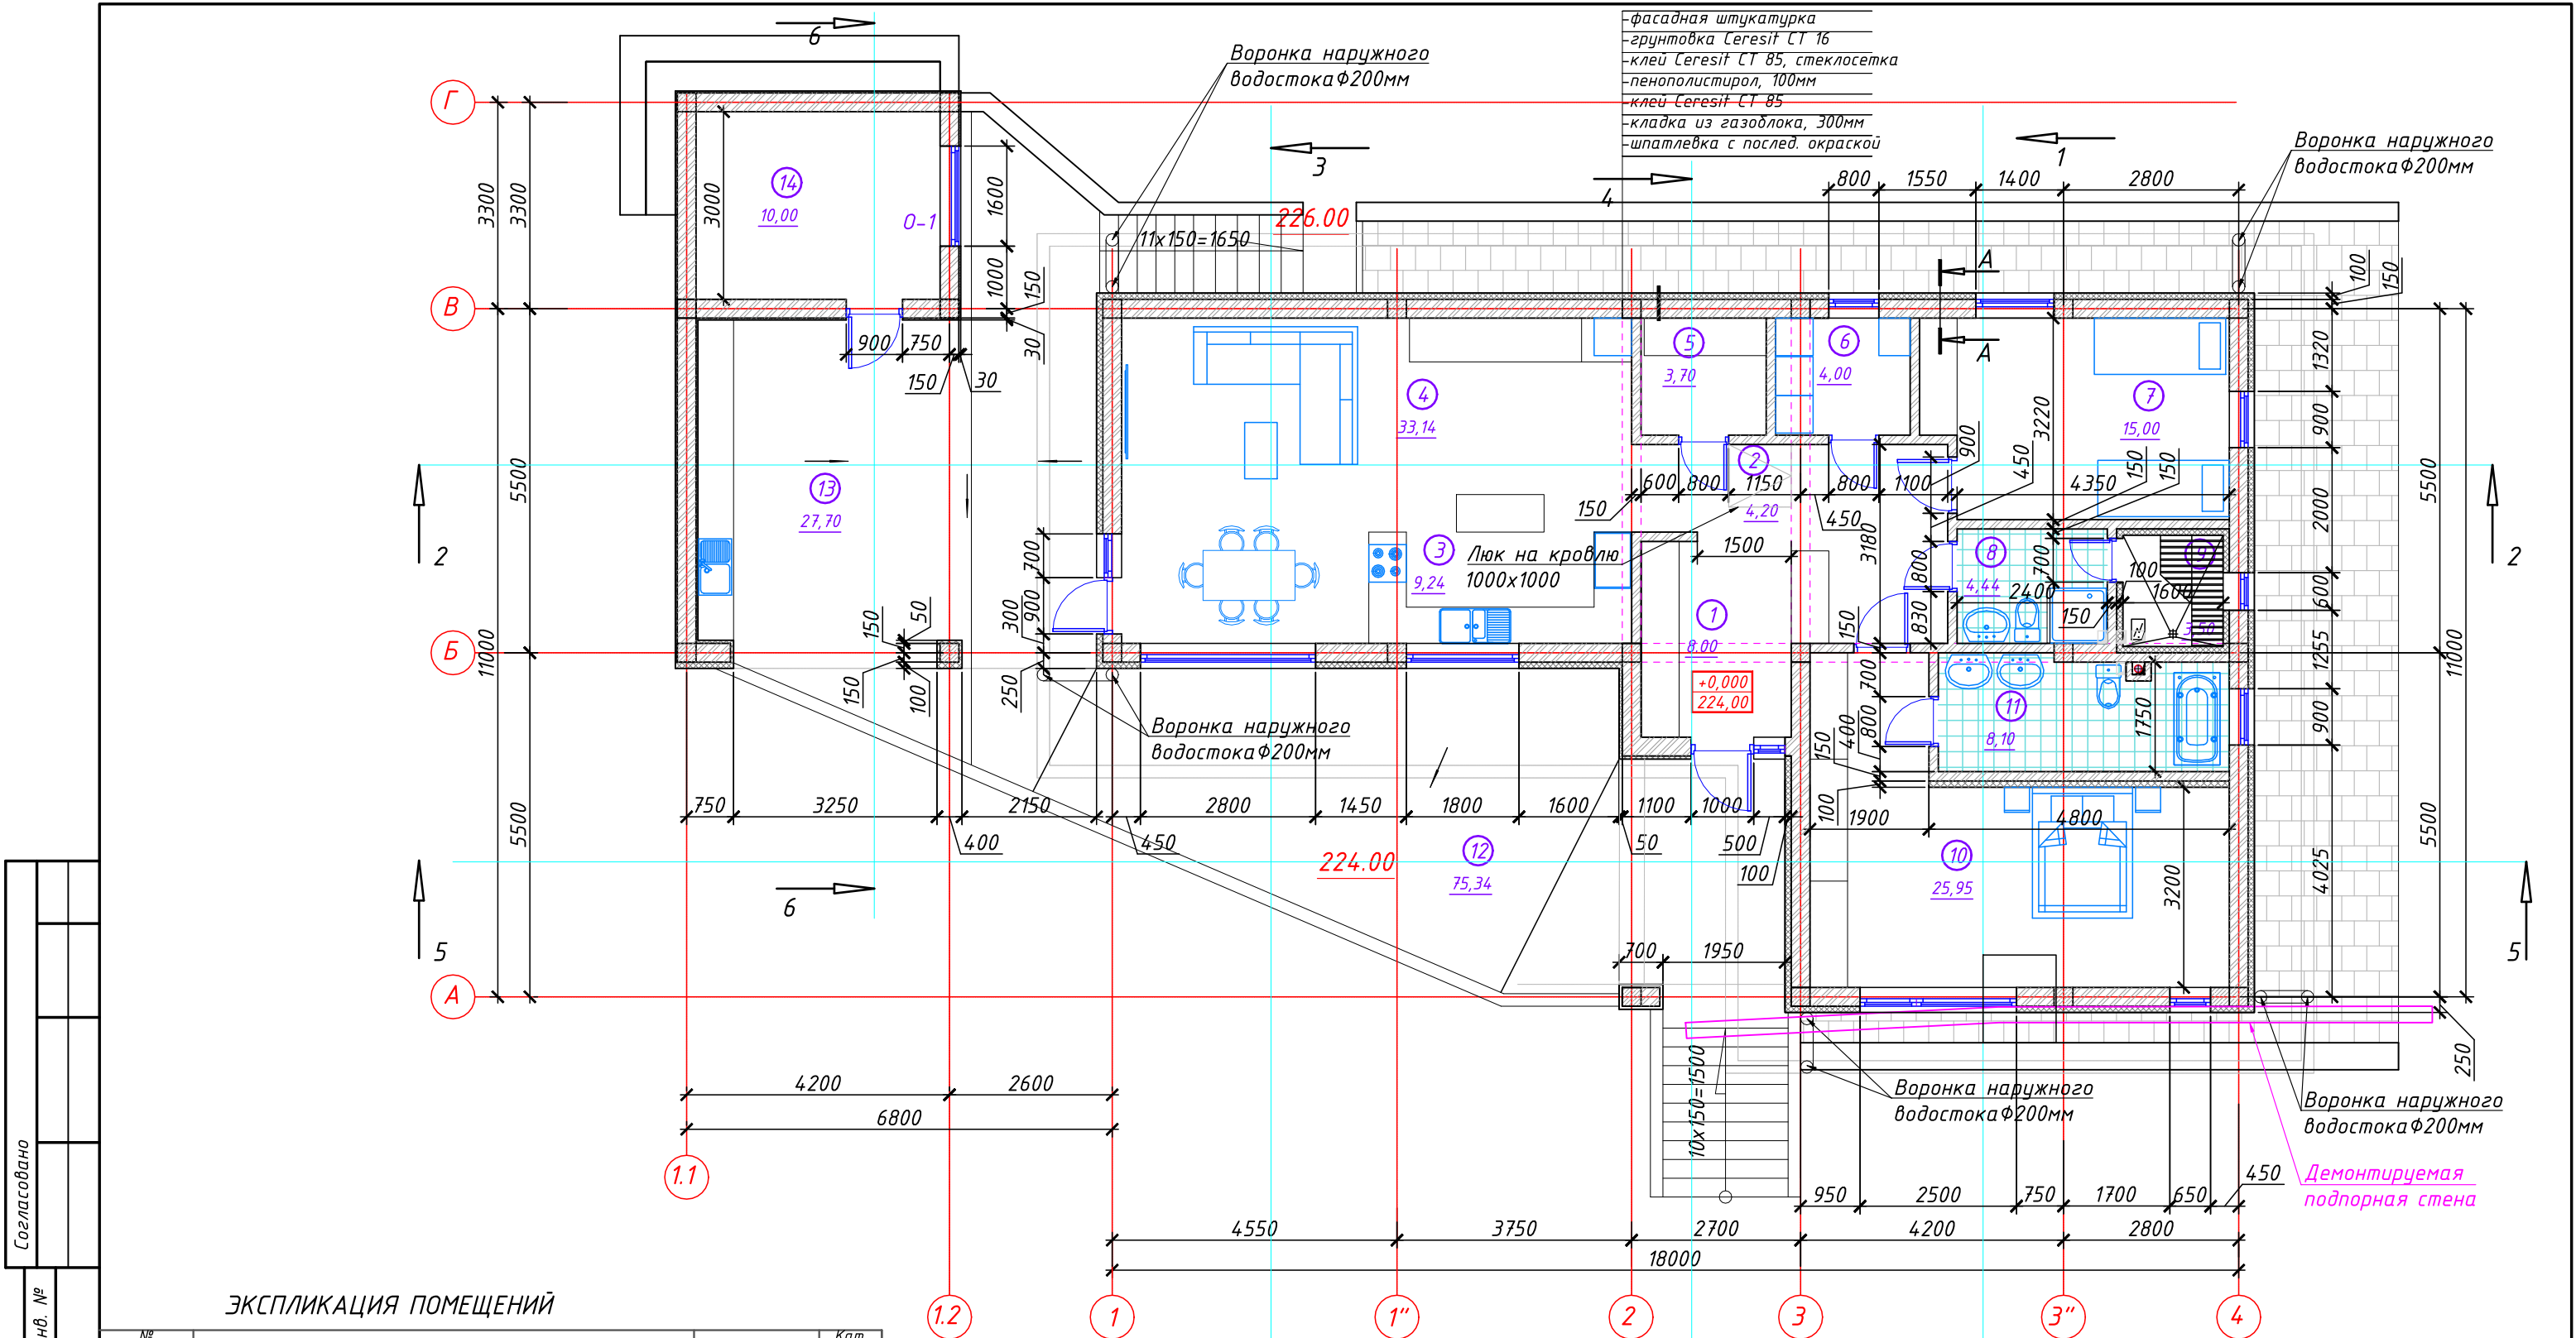

Согласовано		
Взам. инв. №		
Подпись. Дата		
Инв. № подл.		


ЭКСПЛИКАЦИЯ ПОМЕЩЕНИЙ

№ помещения	Наименование	Площадь, м²	Кат. помещен
1	Прихожая	8,00	
2	Коридор	4,20	
3	Кухня	9,24	
4	Гостиная	33,14	
5	Кладовая	3,70	
6	Постирочная, котельная	4,00	
7	Спальня	15,00	
8	Санузел	4,44	
9	Сауна	3,50	
10	Спальня	25,95	
11	Санузел	8,10	
12	Терраса	75,34	
13	Барбекю	27,70	
14	Мастерская	10,00	

УСЛОВНЫЕ ОБОЗНАЧЕНИЯ

- жб колонны, 300x300мм
- вентшахты
- наружные стены, 300мм
кладка из газобетонных блоков,
утеплитель - минераловатные плиты 80мм
штукатурка - 20мм
- перегородки - 150мм,
кладка из газобетонных блоков
- грунт

						02 - 2019 - AP			
						Индивидуальный жилой дом, по адресу: Республика Крым, Муниципальное образование городской округ Алушта, п. Розовый			
Изм.	Кол.	Лист	№ док.	Подпись	Дата				
						Индивидуальный жилой дом	Стадия	Лист	Листов
							Р	2	
ГИП		Голенкова							
Разработ.		Гемдицкий				План на отм. 0,000		самлайн проект инженерное обеспечение зданий	Индивидуальный Предприниматель Голенкова А.В. ОГРНИП 314910223200051
Н. контр.		Коломиец							

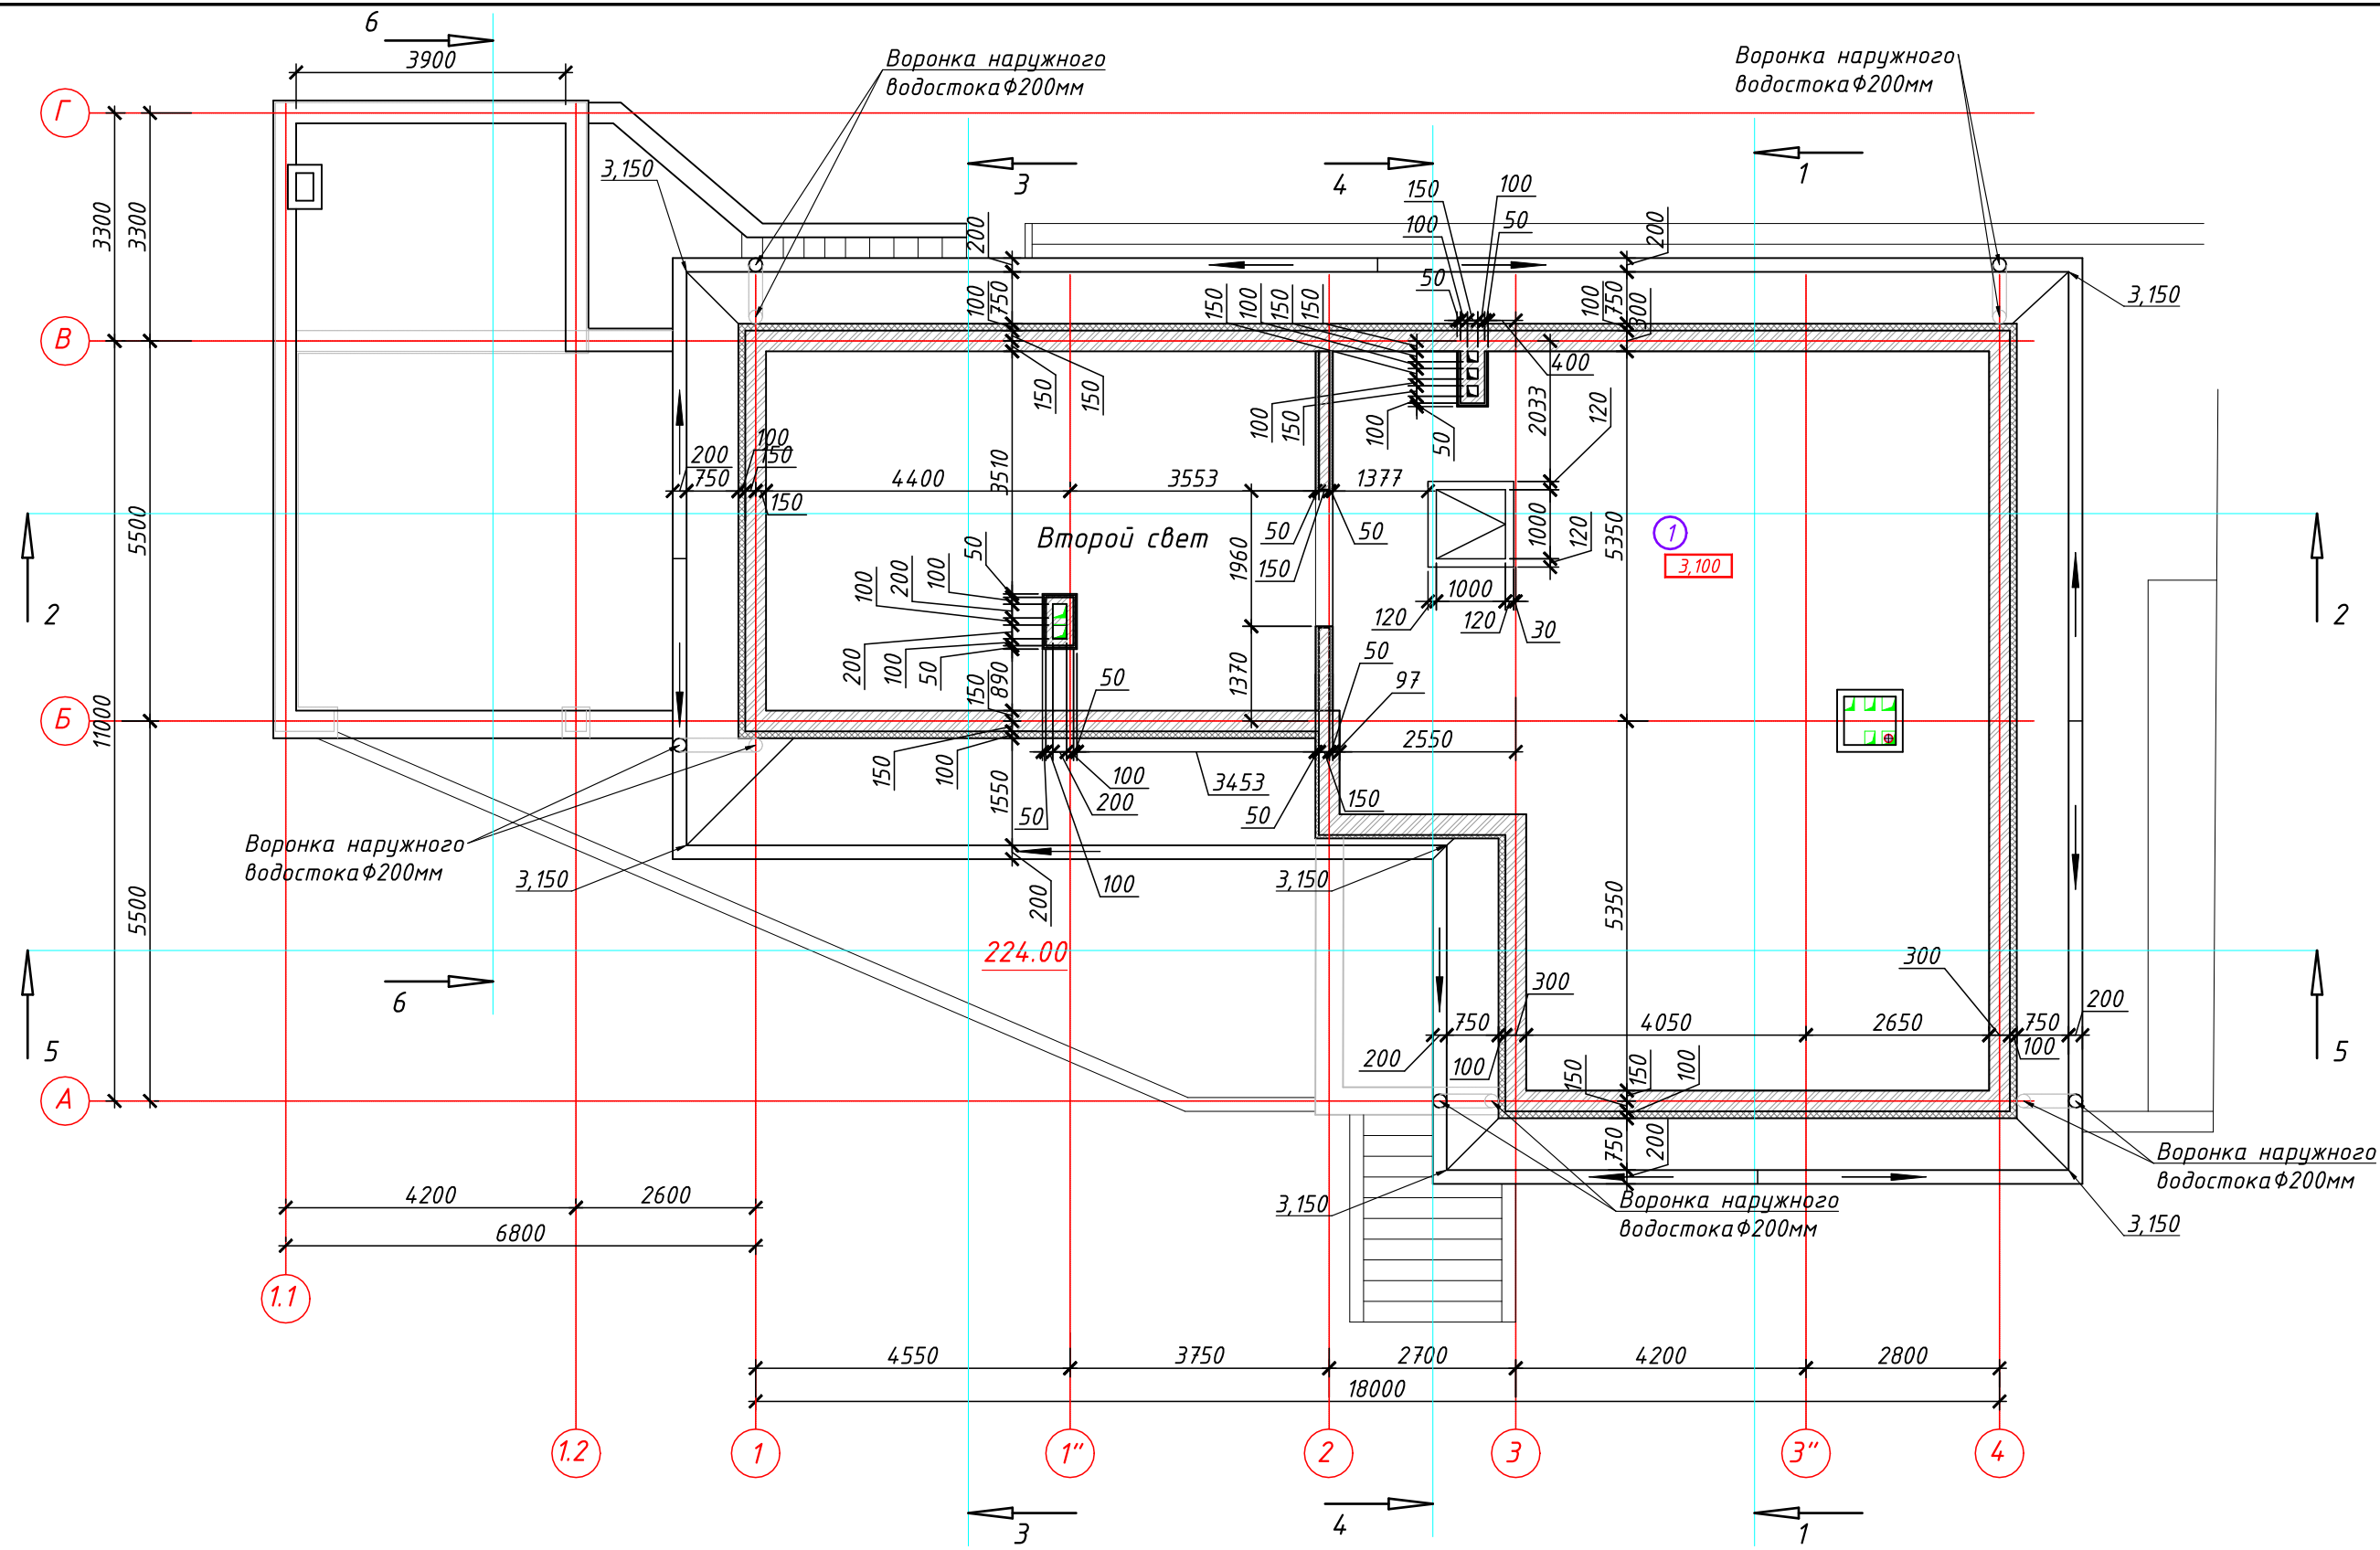


Согласовано					
Взам. инв. №					
Подпись. Дата					
Инв. № подл.					

ЭКСПЛИКАЦИЯ ПОМЕЩЕНИЙ

№ помещения	Наименование	Площадь, м2	Кат. помещен
1	Чердачное пространство	89,92	

						02 - 2019 - AP		
						Индивидуальный жилой дом, по адресу: Республика Крым, Муниципальное образование городской округ Алушта, п. Розовый		
						Индивидуальный жилой дом		
						Стадия	Лист	Листов
						P	4	
						План чердака на отм. 3,100 M1:100		
						Индивидуальный Предприниматель Голенкова А.В. ОГРНИП 314910223200051		
						Формат А3		

Согласовано					
Взам. инв. №					
Подпись. Дата					
Инв. № подл.					

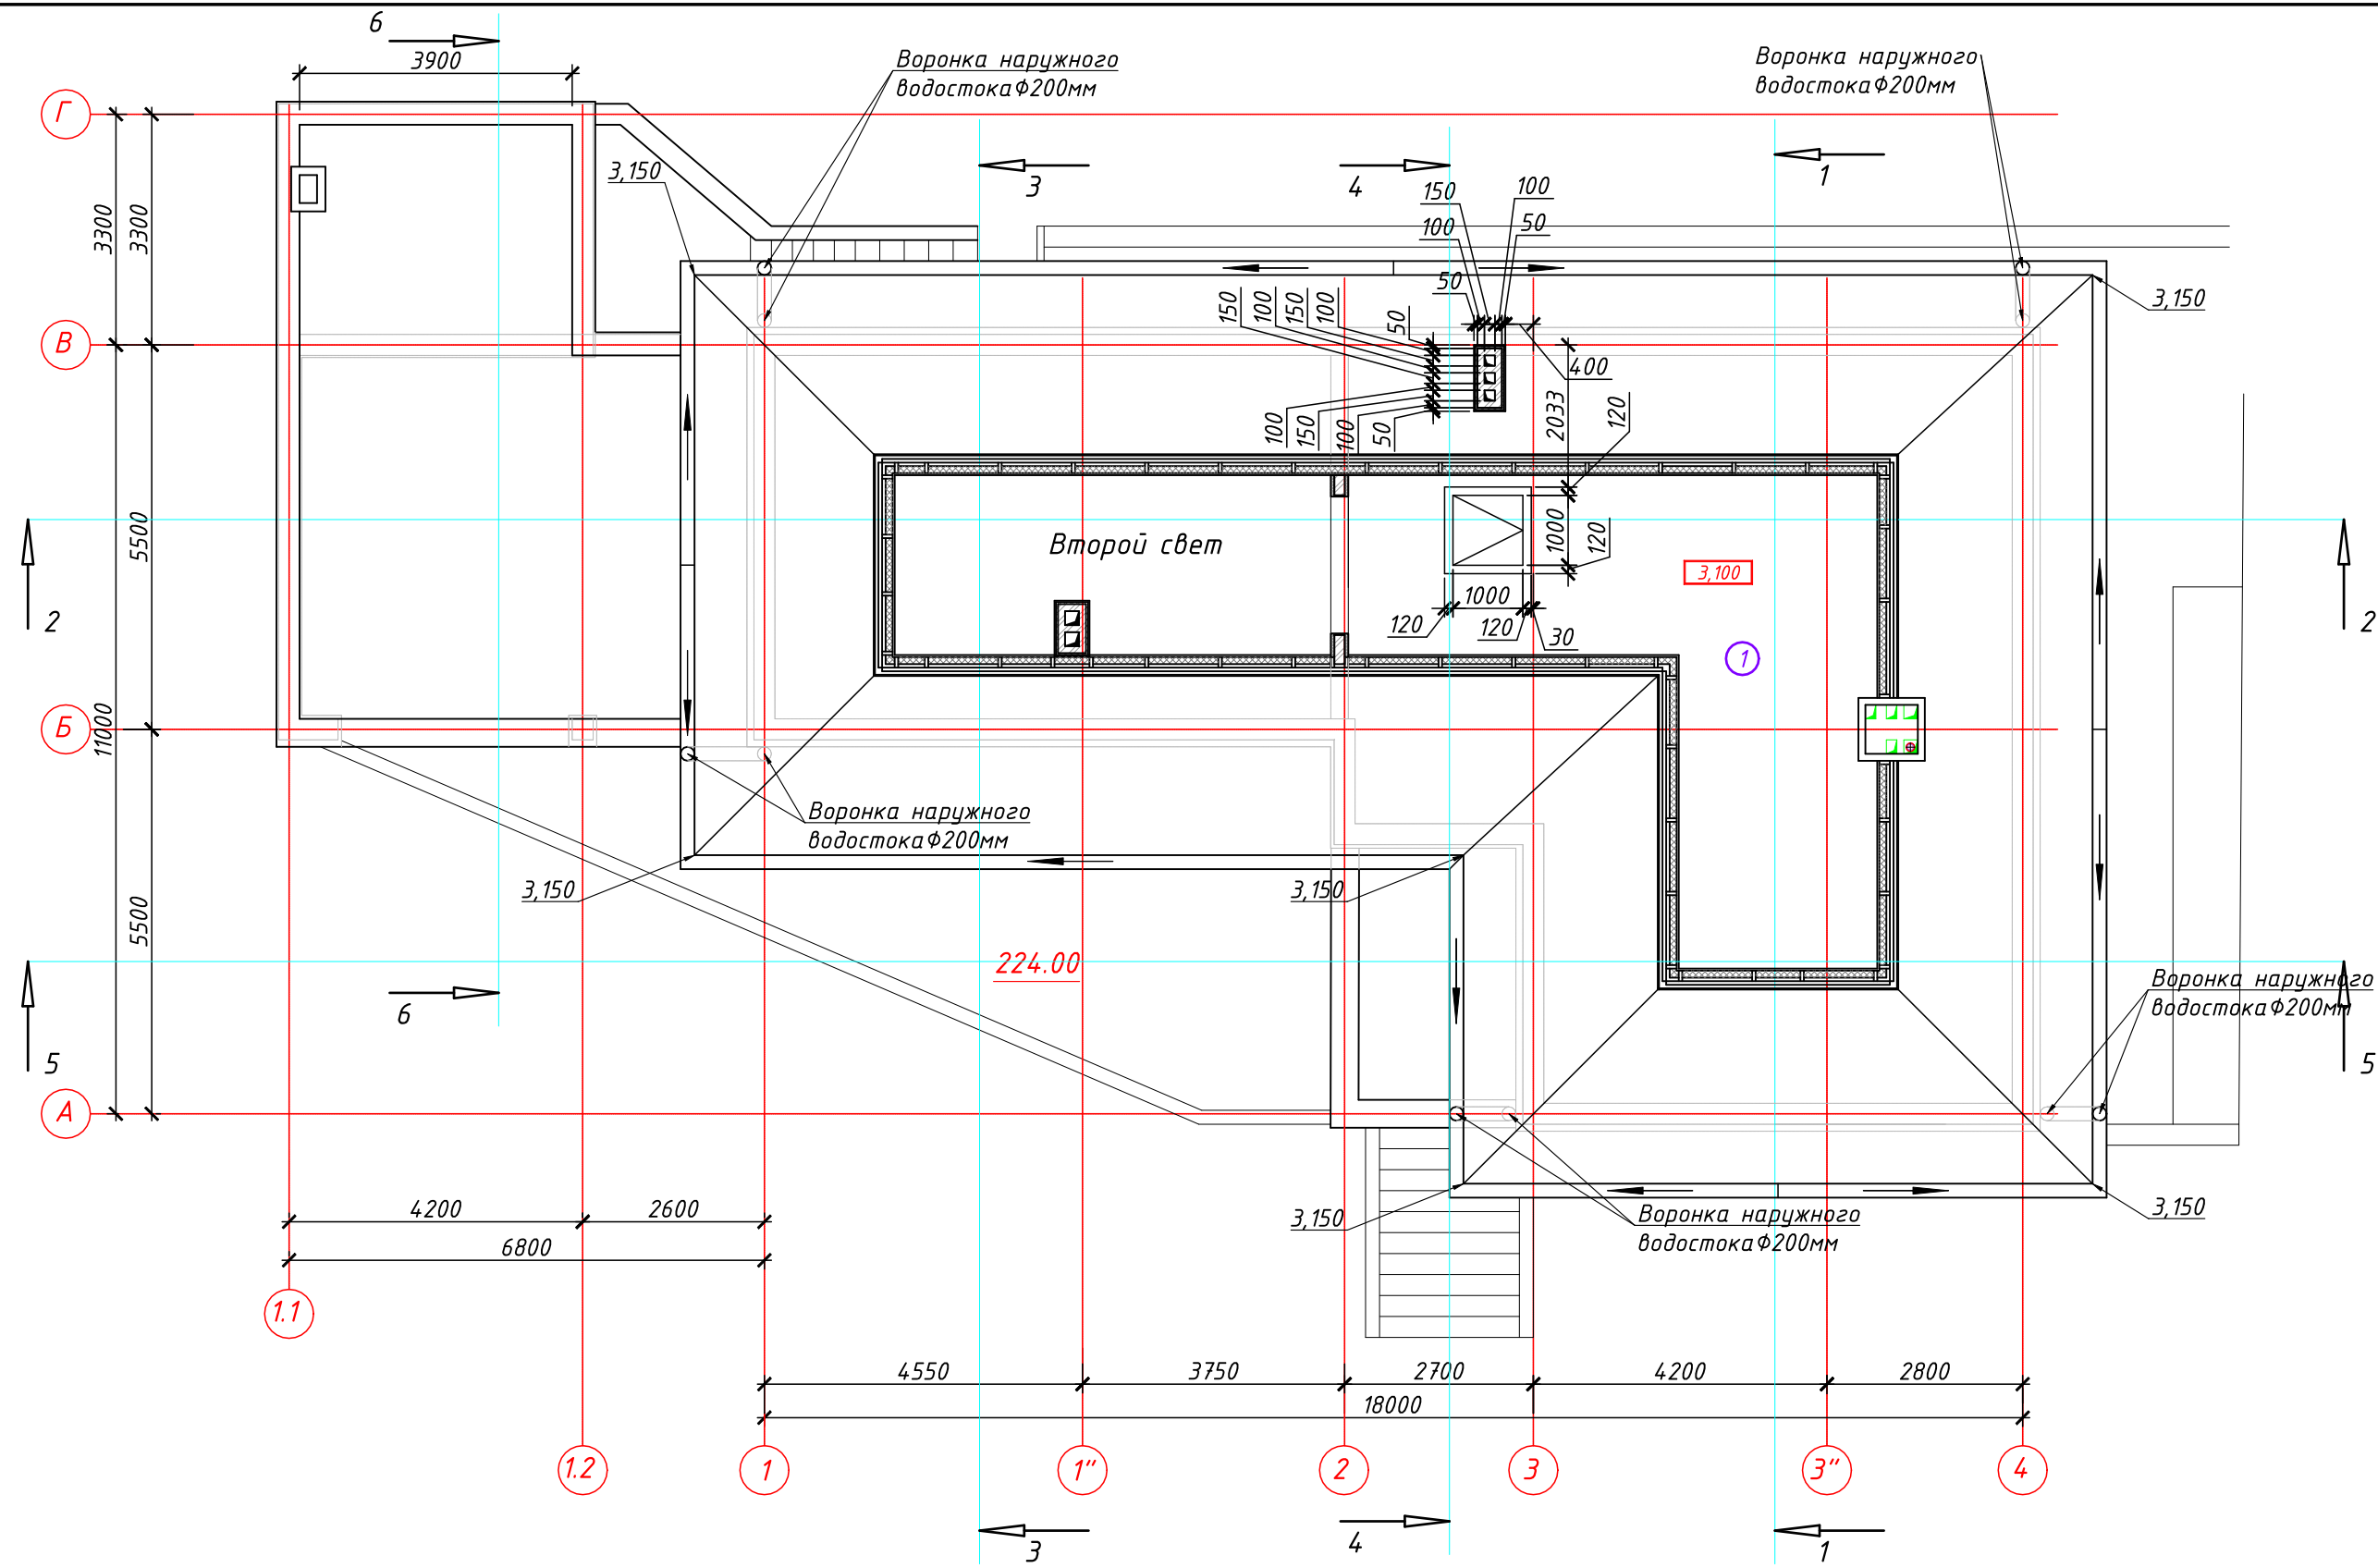


ЭКСПЛИКАЦИЯ ПОМЕЩЕНИЙ

№ помещения	Наименование	Площадь, м2	Кат. помещен
1	Чердачное пространство		

						02 – 2019 – AP			
						Индивидуальный жилой дом, по адресу: Республика Крым, Муниципальное образование городской округ Алушта, п. Розовый			
Изм.	Кол.	Лист	№ док.	Подпись	Дата				
						Индивидуальный жилой дом	Стадия	Лист	Листов
							P	5	
ГИП		Голенкова				План чердака на отм. 4,100 М 1:100	 самлайн проект инженерное обеспечение зданий Индивидуальный Предприниматель Голенкова А.В. ОГРНИП 314910223200051		
Разработ.		Гемдицкий							
Н. контр.		Коломиец							

Согласовано					
Взам. инв. №					
Подпись. Дата					
Инв. № подл.					

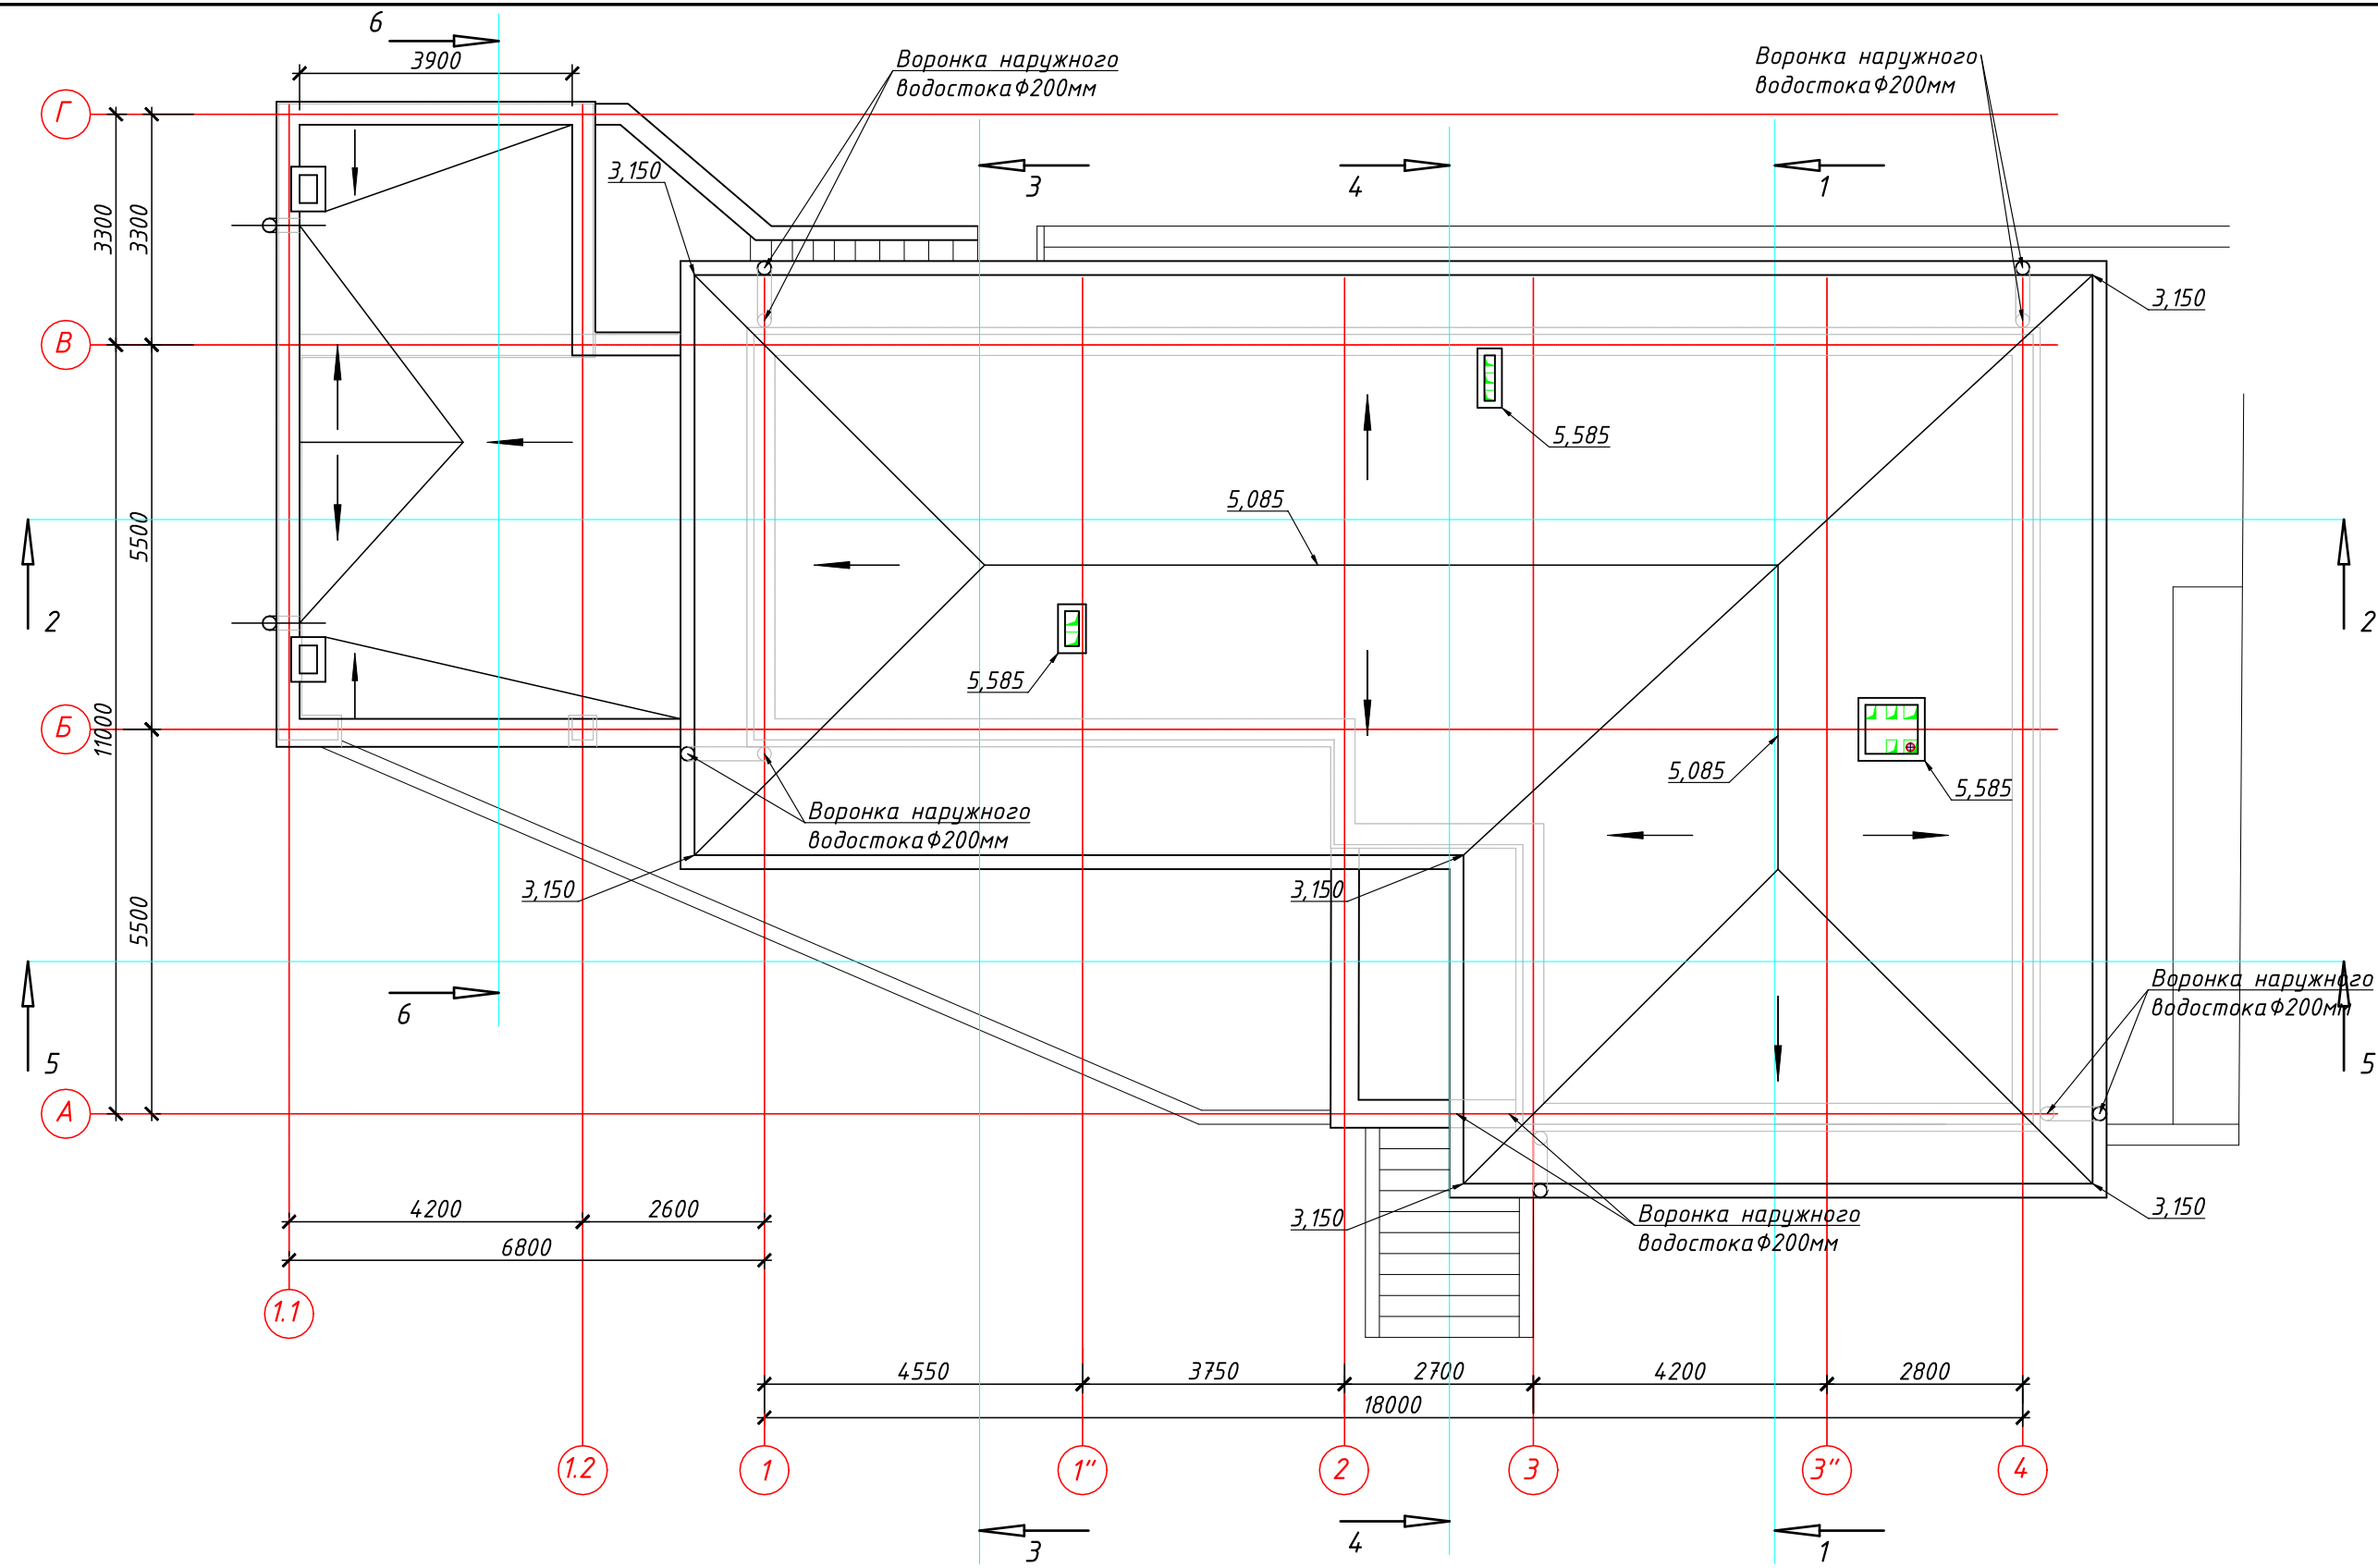


Состав кровли:
-гибкая черепица (Shinglas)
-подкладочный ковер
-сплошной настил (доска/OSB)
-контрорешетка
-ветрозащита
-утеплитель 200мм
-стропила
-пароизоляция
-утепление 50мм
-брус 50х50мм
-гипсокартон 2 слоя

Площадь кровли: 230м²

						02 – 2019 – AP			
						Индивидуальный жилой дом, по адресу: Республика Крым, Муниципальное образование городской округ Алушта, п. Розовый			
Изм.	Кол.	Лист	№ док.	Подпись	Дата				
						Индивидуальный жилой дом	Стадия	Лист	Листов
							P	6	
ГИП		Голенкова				План кровли			
Разработ.		Гемдицкий							
Н. контр.		Коломиец							

Разрез 1-1

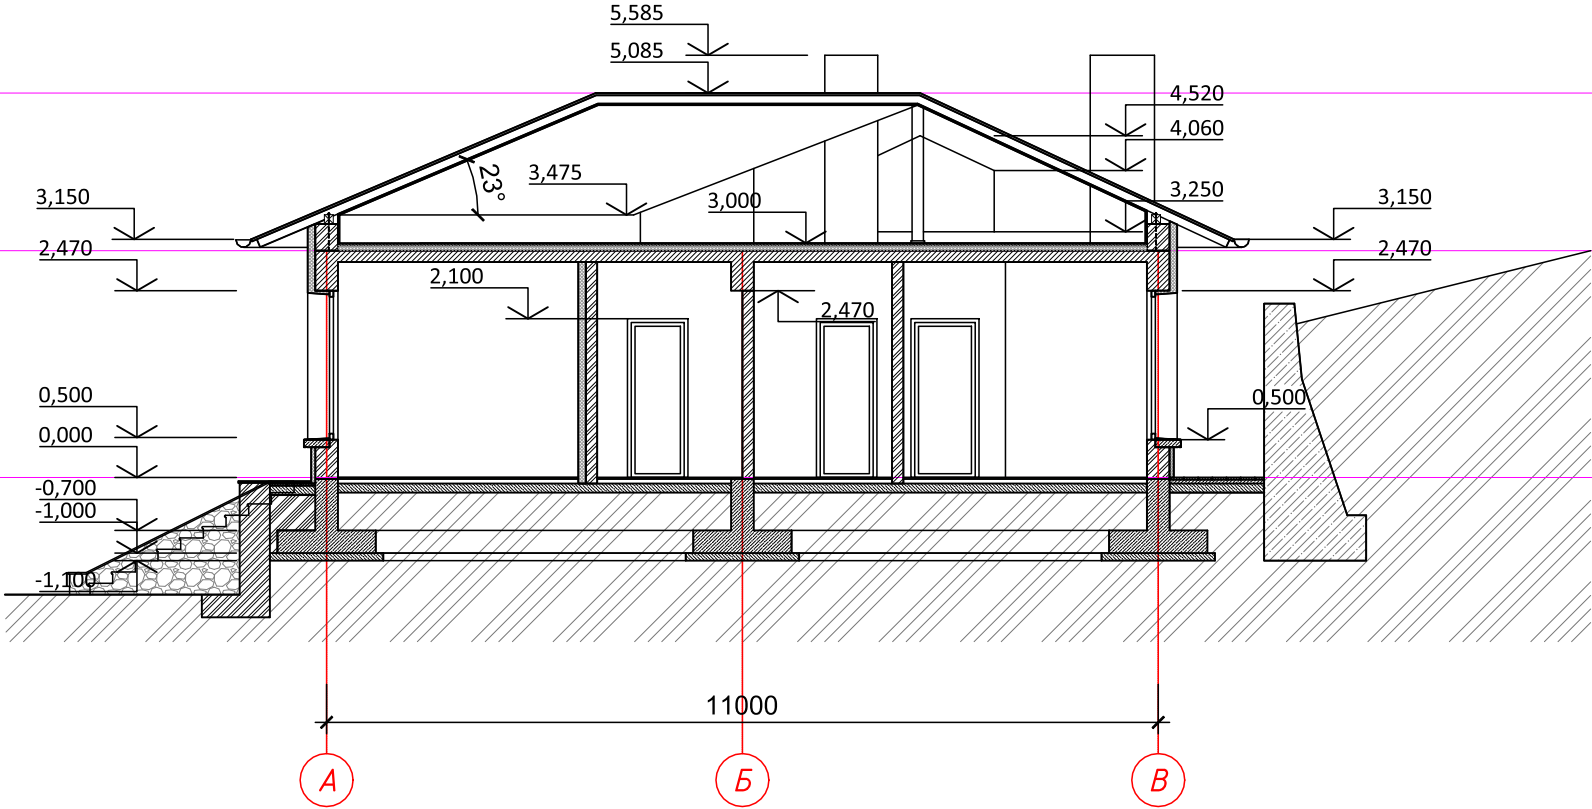


Согласовано				
Взам. инв. №				
Подпись. Дата				
Инв. № подл.				

						02 - 2019 - AP		
						Индивидуальный жилой дом, по адресу: Республика Крым, Муниципальное образование городской округ Алушта, п. Розовый		
Изм.	Кол.	Лист	№ док.	Подпись	Дата	Индивидуальный жилой дом	Стадия	Лист
							P	7
ГИП		Голенкова				Разрез 1-1		Индивидуальный Предприниматель Голенкова А.В. ОГРНИП 314910223200051
Разработ.		Гемдицкий						
Н. контр.		Коломиец						

Разрез 2-2

Монолитная армированная стяжка 20мм
Теплоизоляция из экструдированного
пенополистирола Europlex 80мм
Монолитная железобетонная плита 150мм


-гибкая черепица (Shinglas)
-подкладочный ковер
-сплошной настил (доска/OSB)
-контрорешетка
-ветрозащита
-утеплитель 200мм
-стропила
-пароизоляция
-утепление 50мм
-брус 50х50мм
-гипсокартон 2 слоя

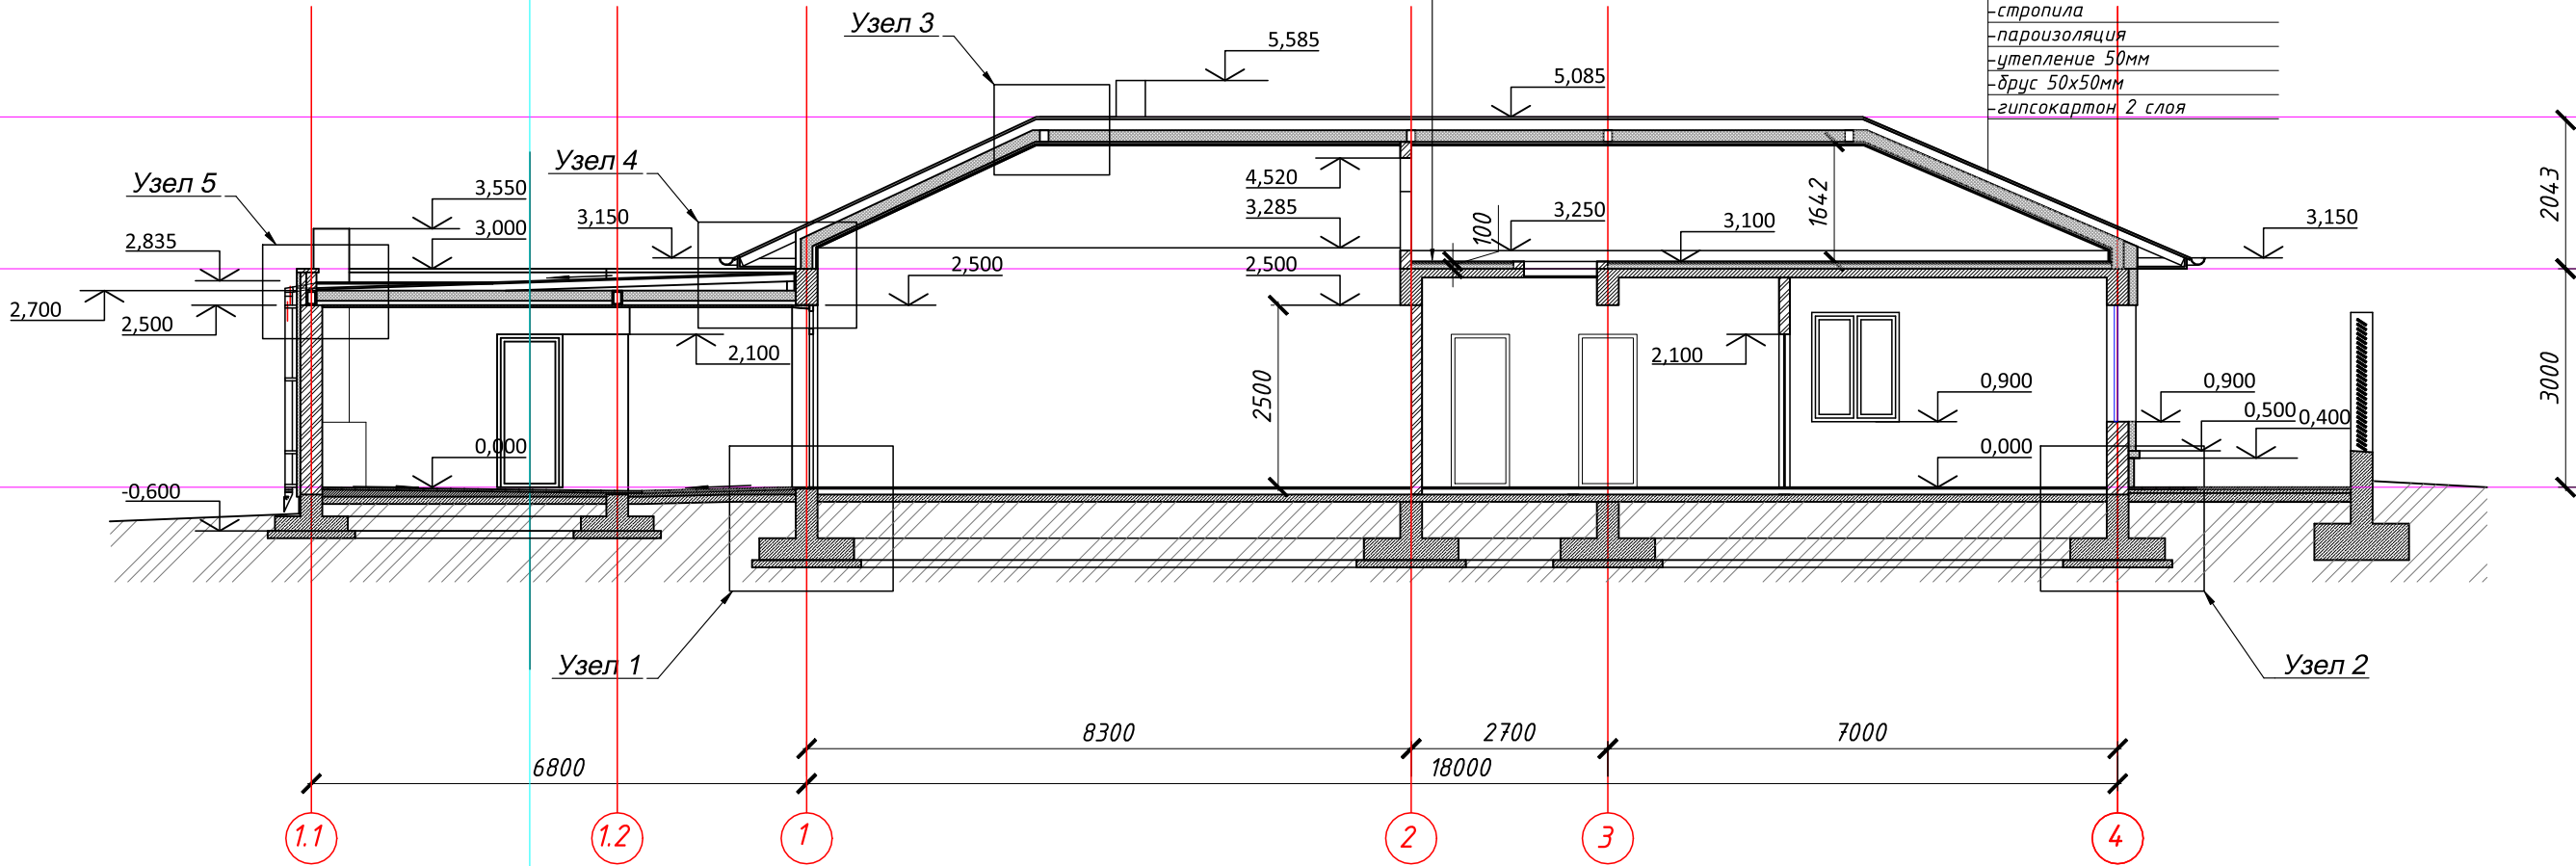

Согласовано	
Взам. инв. №	
Подпись. Дата	
Инв. № подл.	

						02 - 2019 - AP			
						Индивидуальный жилой дом, по адресу: Республика Крым, Муниципальное образование городской округ Алушта, п. Розовый			
Изм.	Кол.	Лист	№ док.	Подпись	Дата				
						Индивидуальный жилой дом	Стадия	Лист	Листов
							P	8	
ГИП		Голенкова				Разрез 2-2	 самлайн проект инженерное обеспечение зданий Индивидуальный Предприниматель Голенкова А.В. ОГРНИП 314910223200051		
Разработ.		Гембицкий							
Н. контр.		Коломиец							

Разрез 3-3

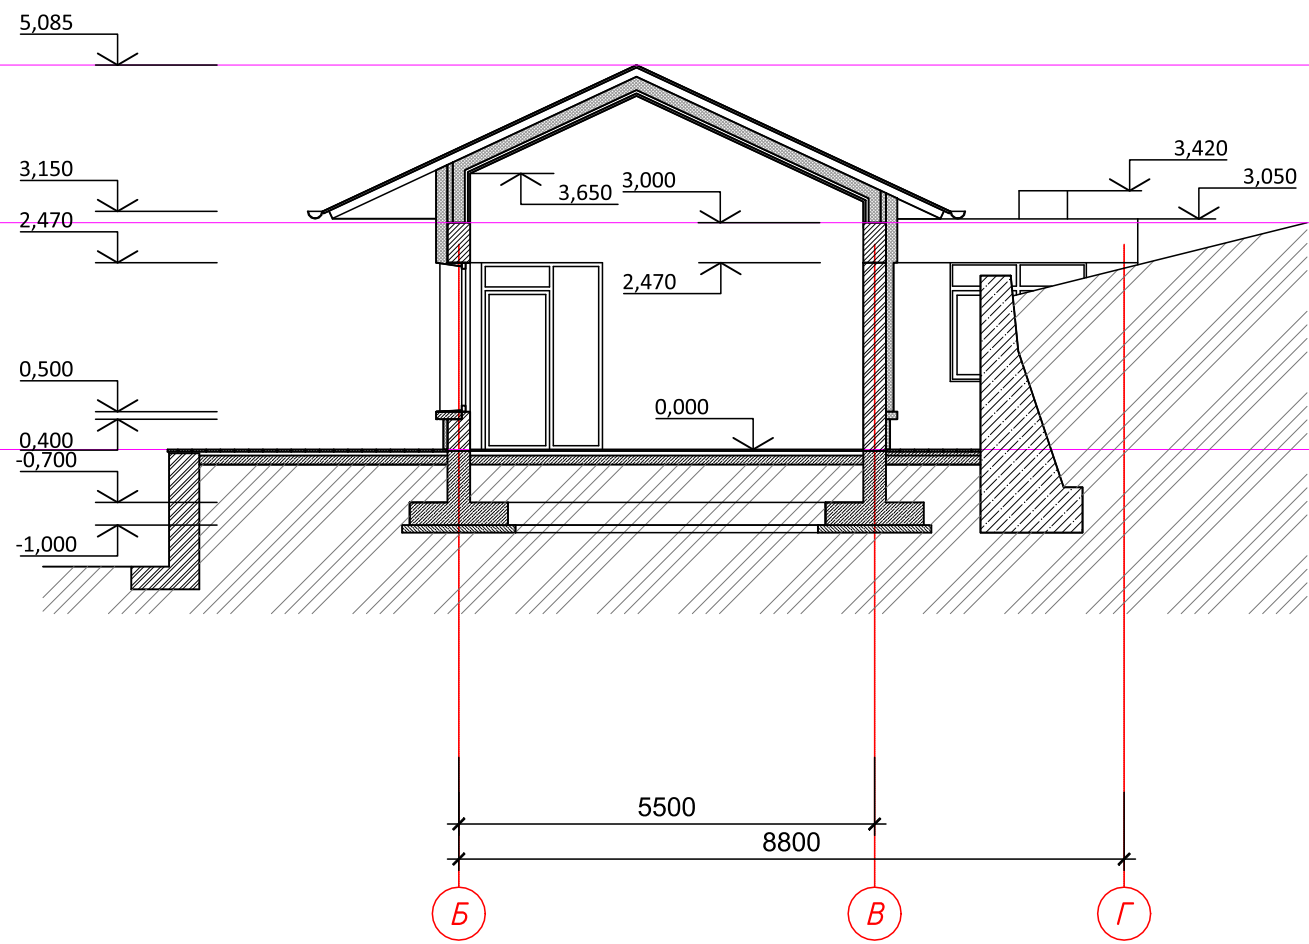


Согласовано			
Взам. инв. №			
Подпись. Дата			
Инв. № подл.			

						02 - 2019 - AP			
						Индивидуальный жилой дом, по адресу: Республика Крым, Муниципальное образование городской округ Алушта, п. Розовый			
Изм.	Кол.	Лист	№ док.	Подпись	Дата				
						Индивидуальный жилой дом	Стадия	Лист	Листов
							P	9	
ГИП		Голенкова				Разрез 3-3	 самлайн проект Индивидуальный Предприниматель Голенкова А.В. ОГРНИП 314910223200051		
Разработ.		Гемдицкий							
Н. контр.		Коломиец							

Согласовано			
Взам. инв. №			
Подпись. Дата			
Инв. № подл.			

Разрез 4-4

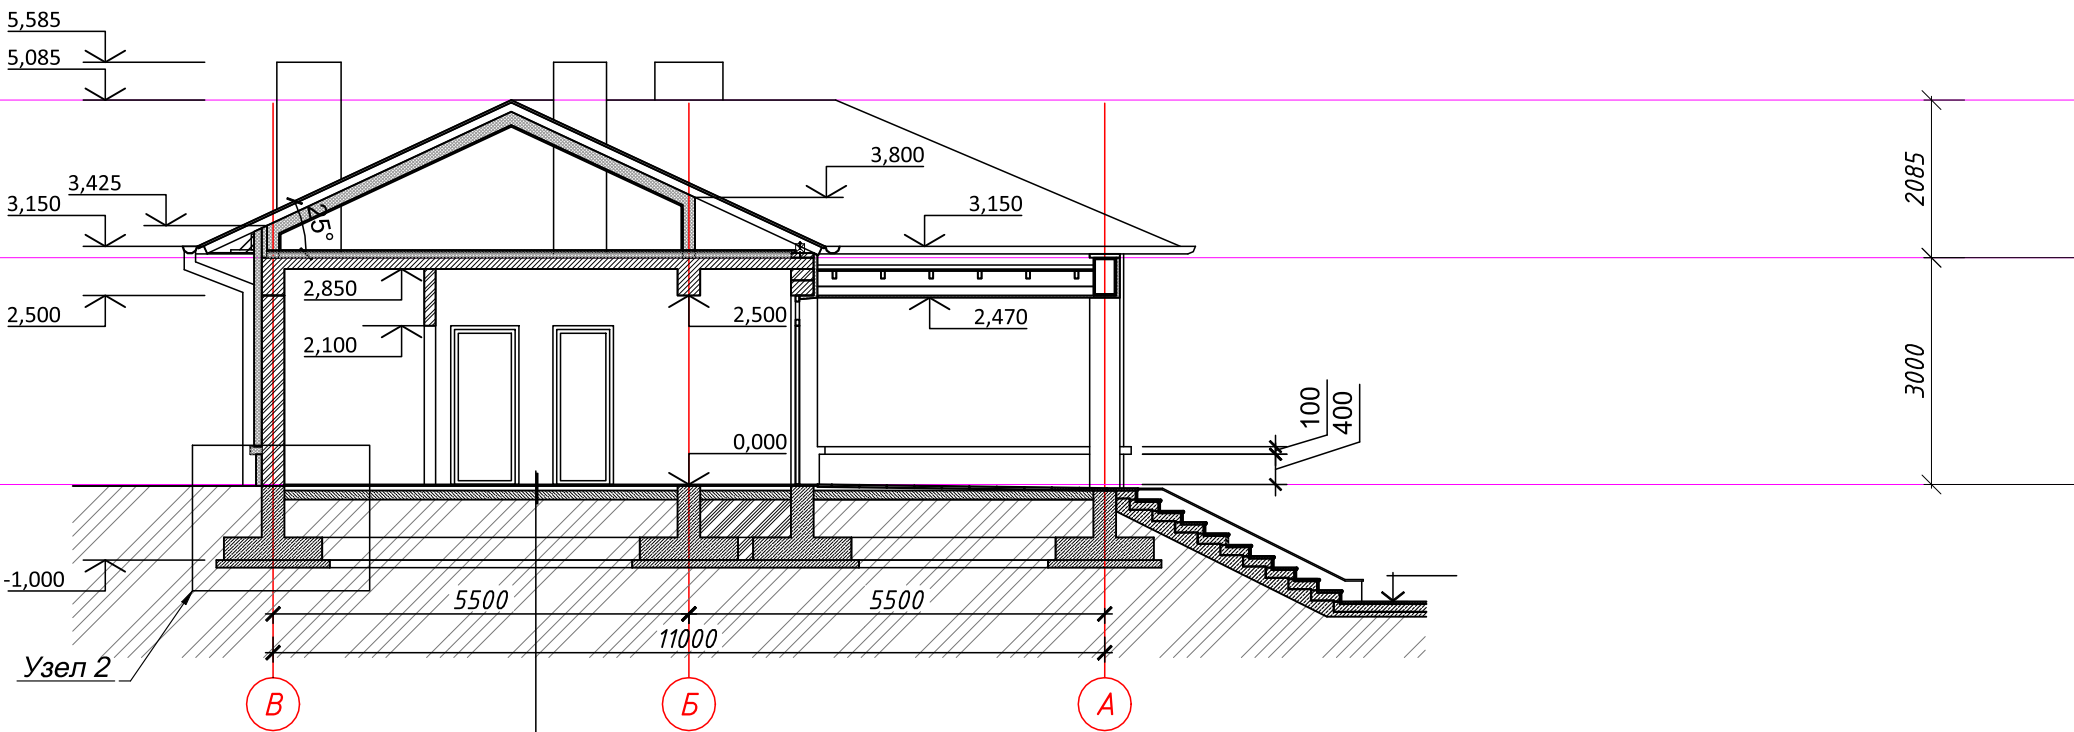


- Керамическая плитка на клею, 20мм
- Монолитная стяжка с отопительной трубой, 70мм
- Защитная фольгированная пленка, отстенная изоляция
- Теплоизоляция из экструдированного пенополистирола
- Europlex, 100мм
- Бетонное основание, бетон В25, 100мм
- Гидроизоляционные бетонитовые
- маты Edilmodul®/мембрана Bitustick по грунтовке Ceresit BT 2,0мм
- Бетонная подготовка-бетон В25(армированная стальной оцинкованной сеткой 50мм
- Дренажная геомембрана ИЗОЛИТ
- Нетканый термически скрепленный
- геотекстиль Тураг® SF 56
- Уплотненный грунт основания

						02 - 2019 - AP			
						Индивидуальный жилой дом, по адресу: Республика Крым, Муниципальное образование городской округ Алушта, п. Розовый			
Изм.	Кол.	Лист	№ док.	Подпись	Дата				
						Индивидуальный жилой дом	Стадия	Лист	Листов
							P	10	
ГИП		Голенкова				Разрез 4-4			
Разработ.		Гемдицкий							
Н. контр.		Коломиец							


Согласовано			
Взам. инв. №			
Подпись. Дата			
Инв. № подл.			

Разрез 5-5

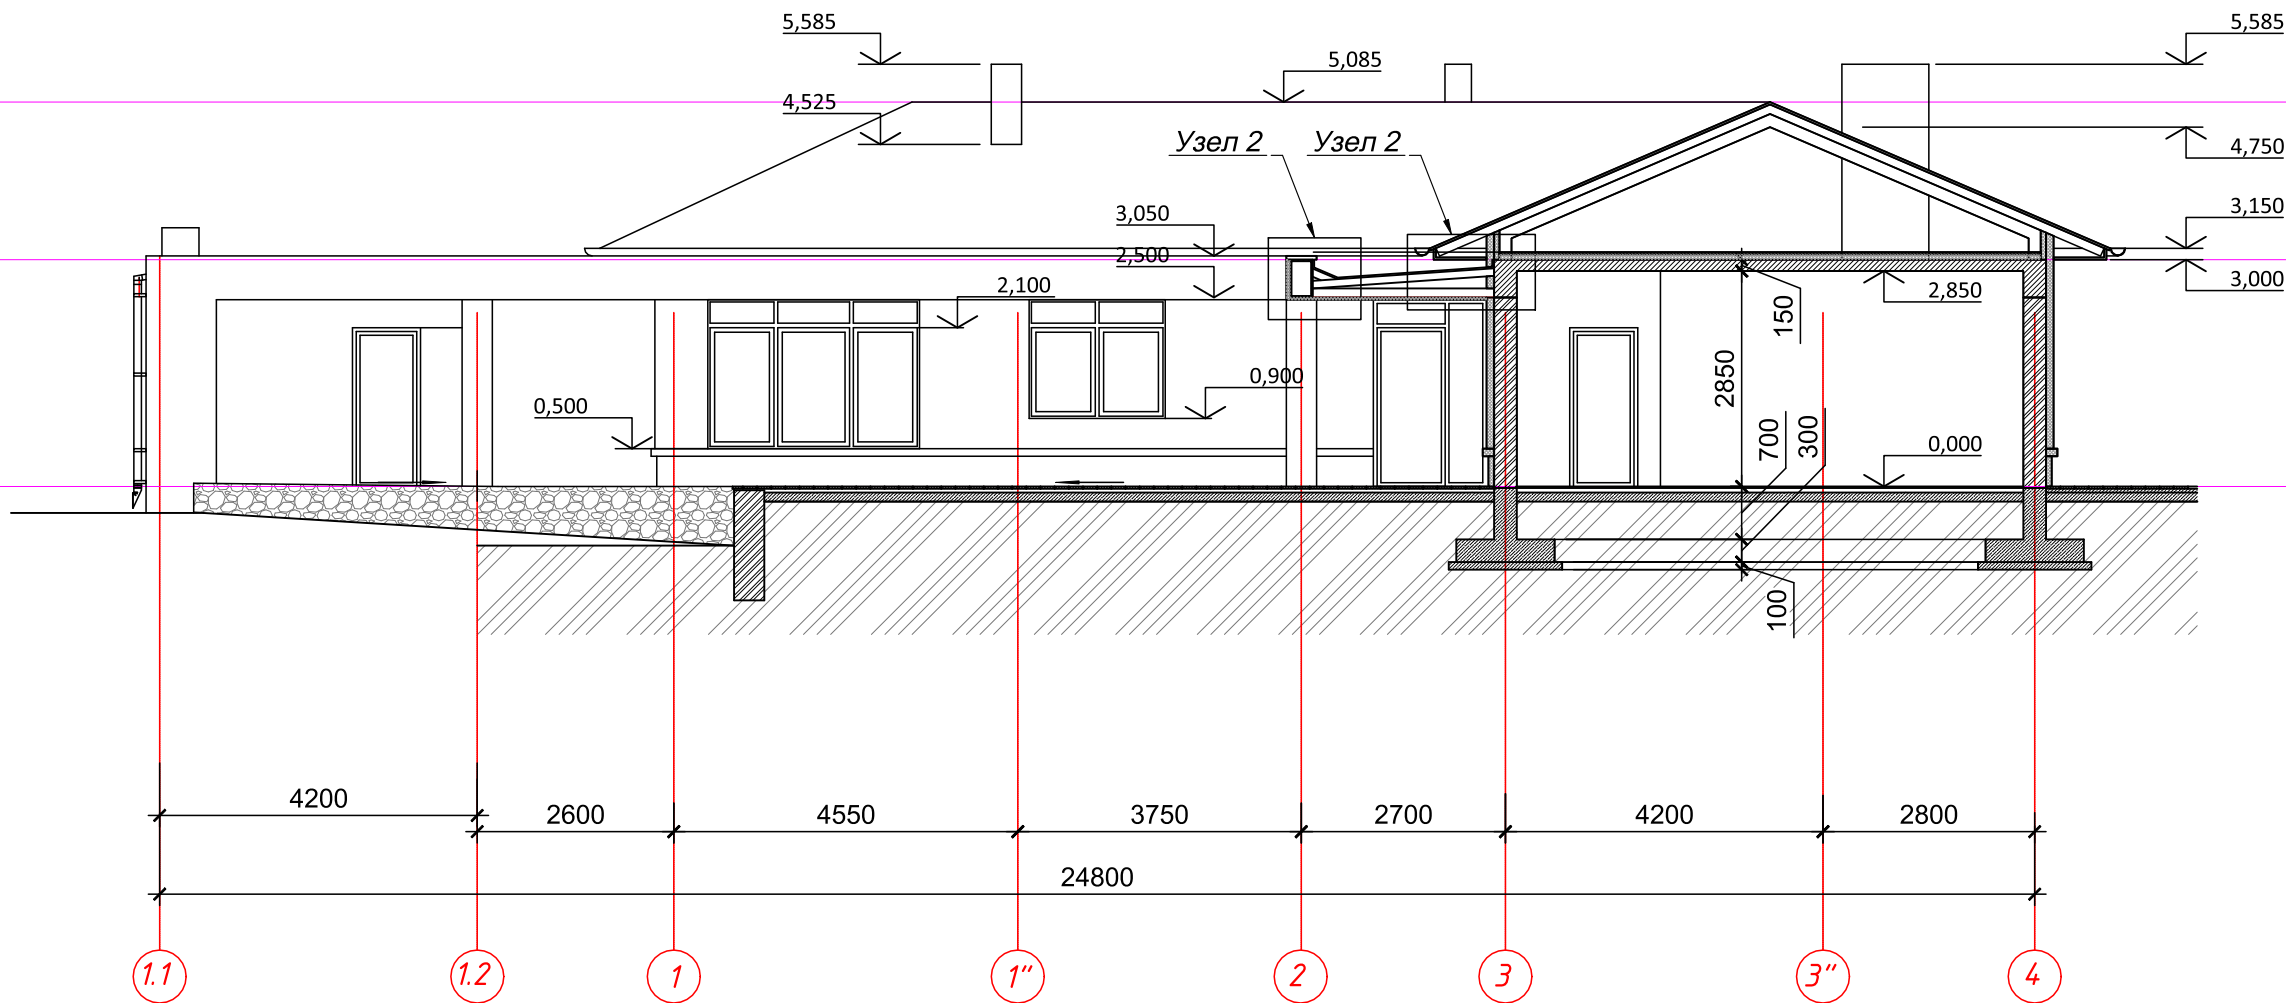

						02 - 2019 - AP		
						Индивидуальный жилой дом, по адресу: Республика Крым, Муниципальное образование городской округ Алушта, п. Розовый		
Изм.	Кол.	Лист	№ док.	Подпись	Дата	Индивидуальный жилой дом	Стадия	Лист
							P	11
ГИП		Голенкова				Разрез 5-5		Индивидуальный Предприниматель Голенкова А.В. ОГРНИП 314910223200051
Разработ.		Гемдицкий						
Н. контр.		Коломиец						


Согласовано			
Взам. инв. №			
Подпись. Дата			
Инв. № подл.			

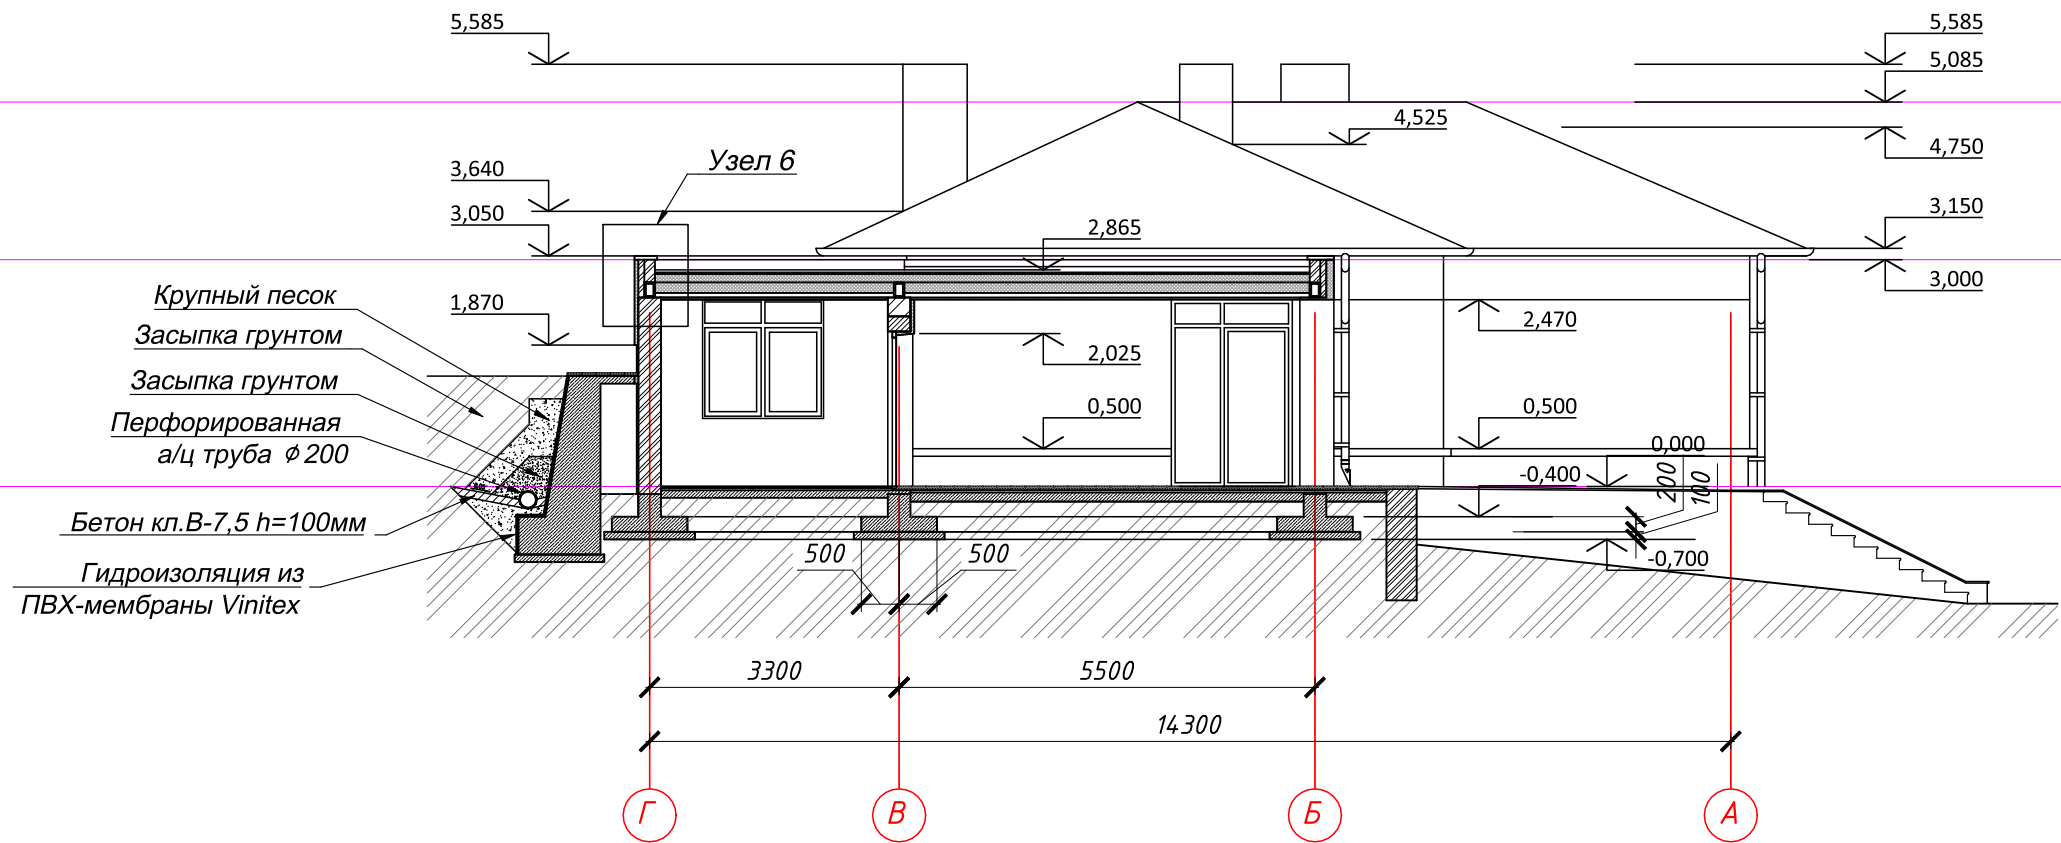

						02 - 2019 - AP			
						Индивидуальный жилой дом, по адресу: Республика Крым, Муниципальное образование городской округ Алушта, п. Розовый			
Изм.	Кол.	Лист	№ док.	Подпись	Дата				
						Индивидуальный жилой дом	Стадия	Лист	Листов
							P	12	
ГИП		Голенкова				Разрез 6-6			
Разработ.		Гемдицкий							
Н. контр.		Коломиец							


Узел 1
М 1:10

Грунт обратной засыпки
Защитный слой из излопробивного геотекстиля Tippiex BS 25
Гидроизоляция из ПВХ-мембраны Vinitex
Разделительный слой из излопробивного геотекстиля Tippiex BS 16
Теплоизоляция из экструдированного пенополистирола Europlex
Ж/б стена фундамента

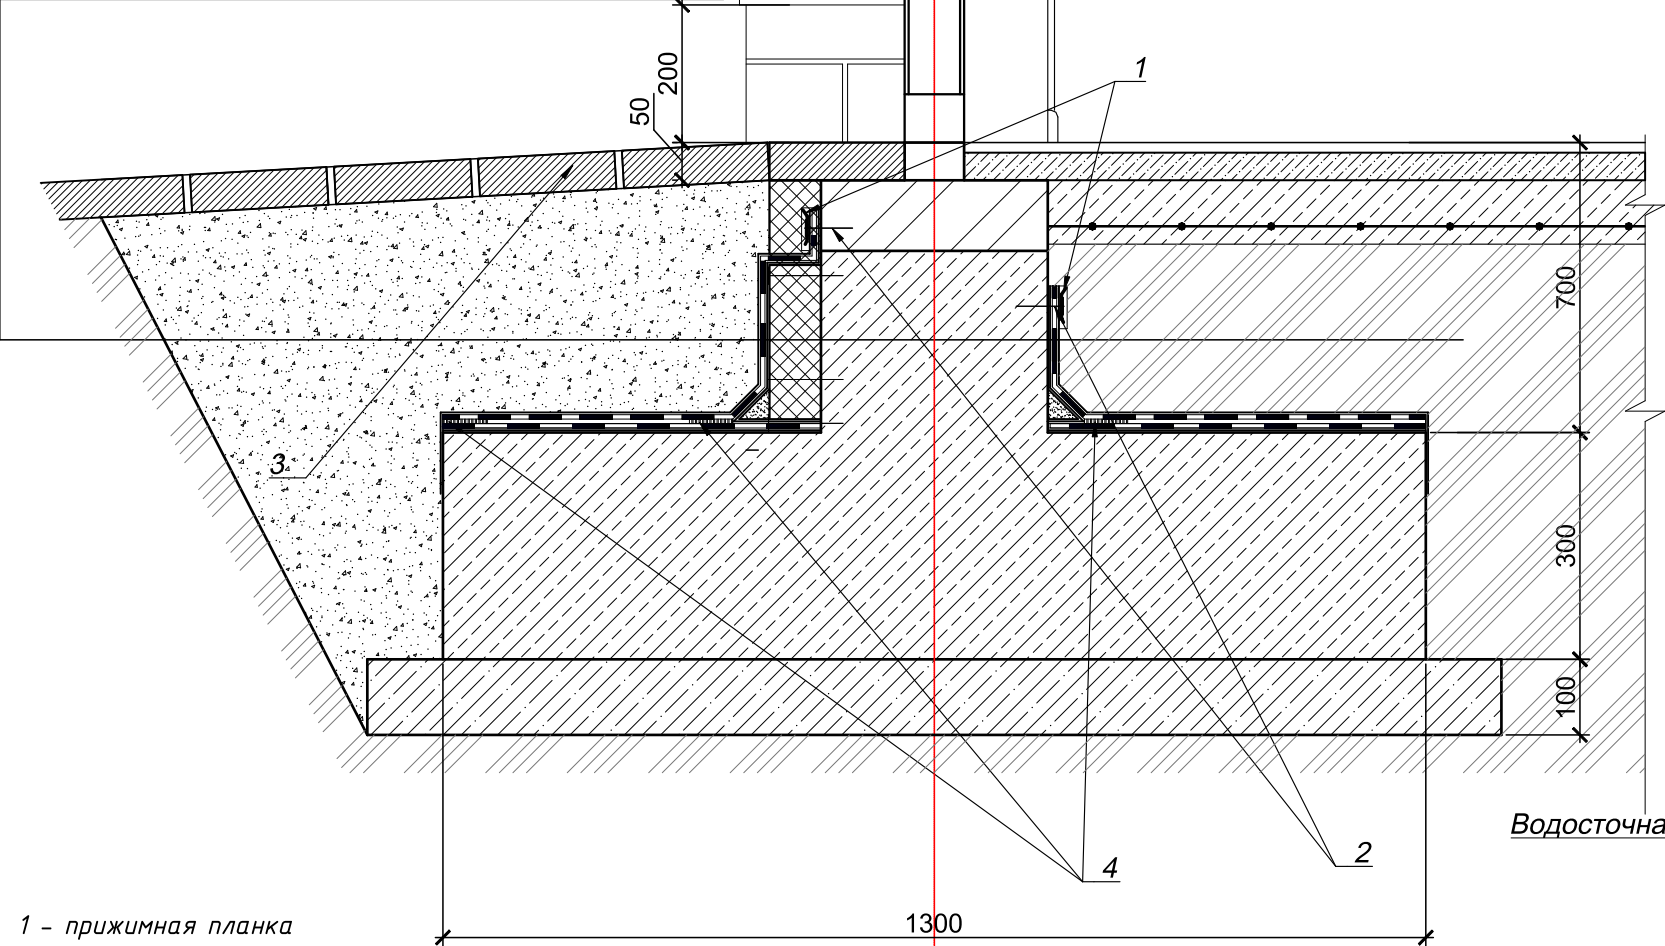

- 1 - прижимная планка
2 - механический крепеж
3 - Плитка тротуарная
4 - сварной шов


Узел оконного проема

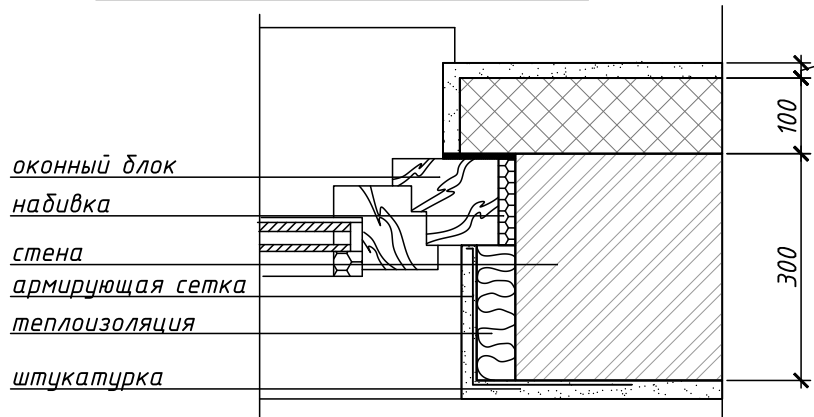

Узел 5.
М1:20

Воронка парпетная ТПЕ Ø100 мм

Балка из швеллеров 200x150 мм

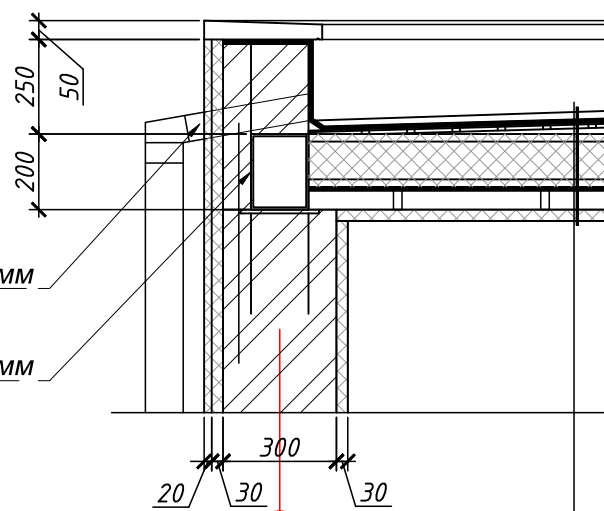

Битумная черепица

Подкладочный ковер

Сплошная обрешетка из влагостойкойфанеры или ОСП 30мм

Обрешетка деревянная по металлическомукаркасу 20x10мм

Утеплитель **SUPERROCK, ROCKMIN, DOMROCK** **
толщиной 200 мм между балками и каркасом обрешетки

Металлическая балка из швеллера 140мм

Пароизоляция

Элемент для крепления гипсокартонных листов

Подшивной потолок из гипсокартона 30мм

Узел 4.
М1:20

Водосточная система

Пирог кровли


Уголок металлический для крепления элементов кровли

Металлическая балка из двух швелеров

Деревянный брусок для
крепления пирога кровли

Закладная деталь

Монолитная ж/б балка

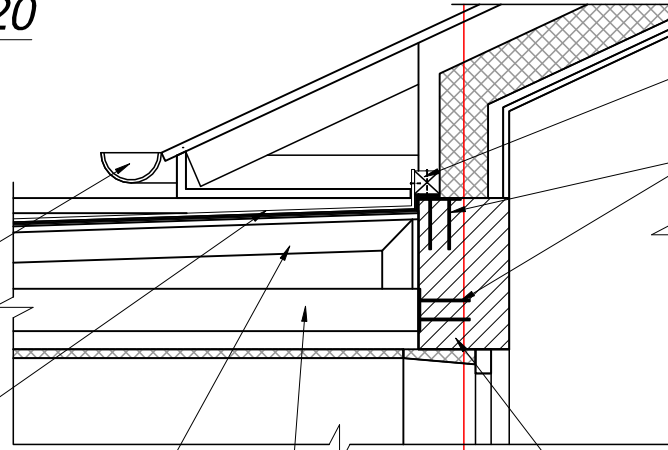

02 - 2019 - AP

Индивидуальный жилой дом, по адресу: Республика Крым,
Муниципальное образование городской округ Алушта,
п. Розовый

Индивидуальный жилой дом


Стадия	Лист	Листов
Р	13	

Узлы и детали (начало)


самлайн
проект
инженерное обеспечение
зданий

Индивидуальный
Предприниматель
Голенкова А.В.
ОГРНИП
314910223200051


Узел 2 М 1:10

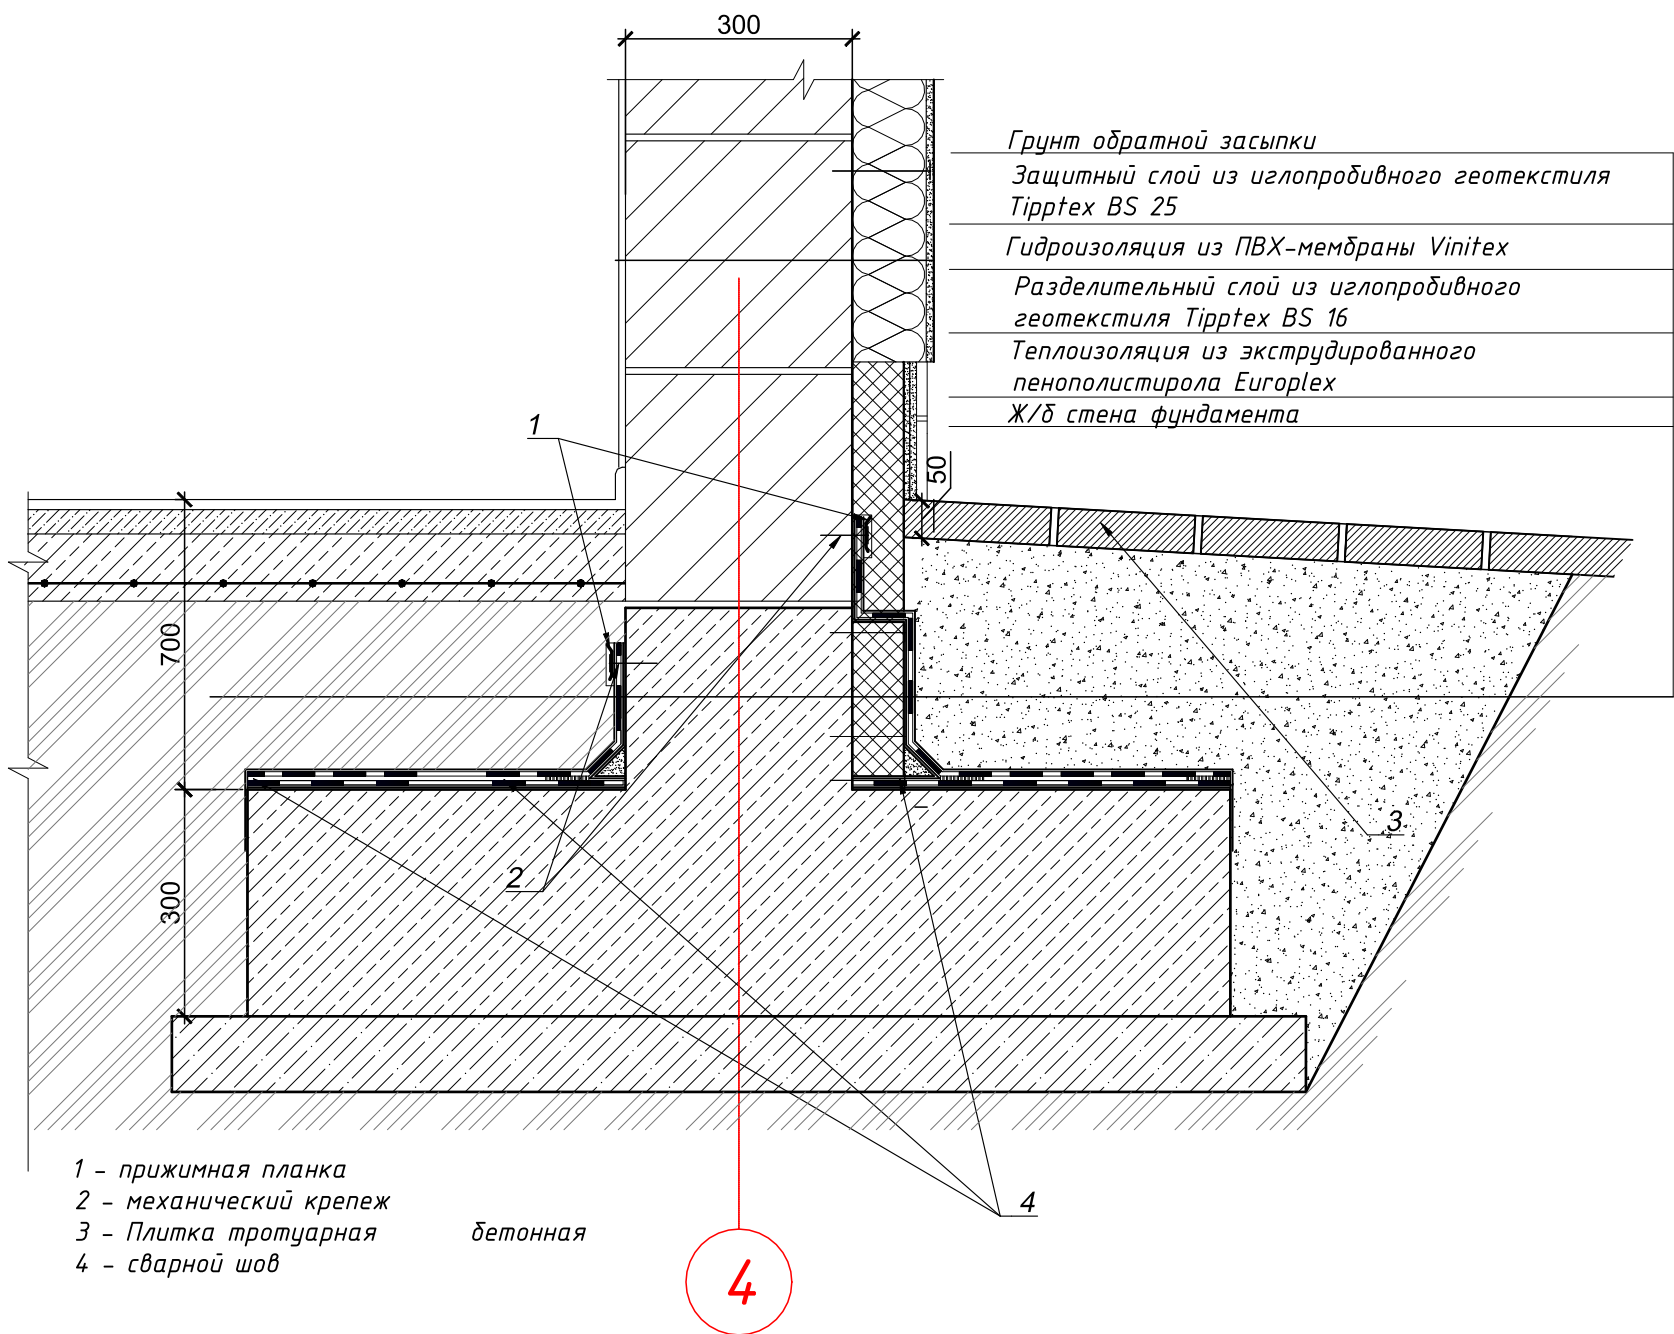

Узел 3 М 1:10

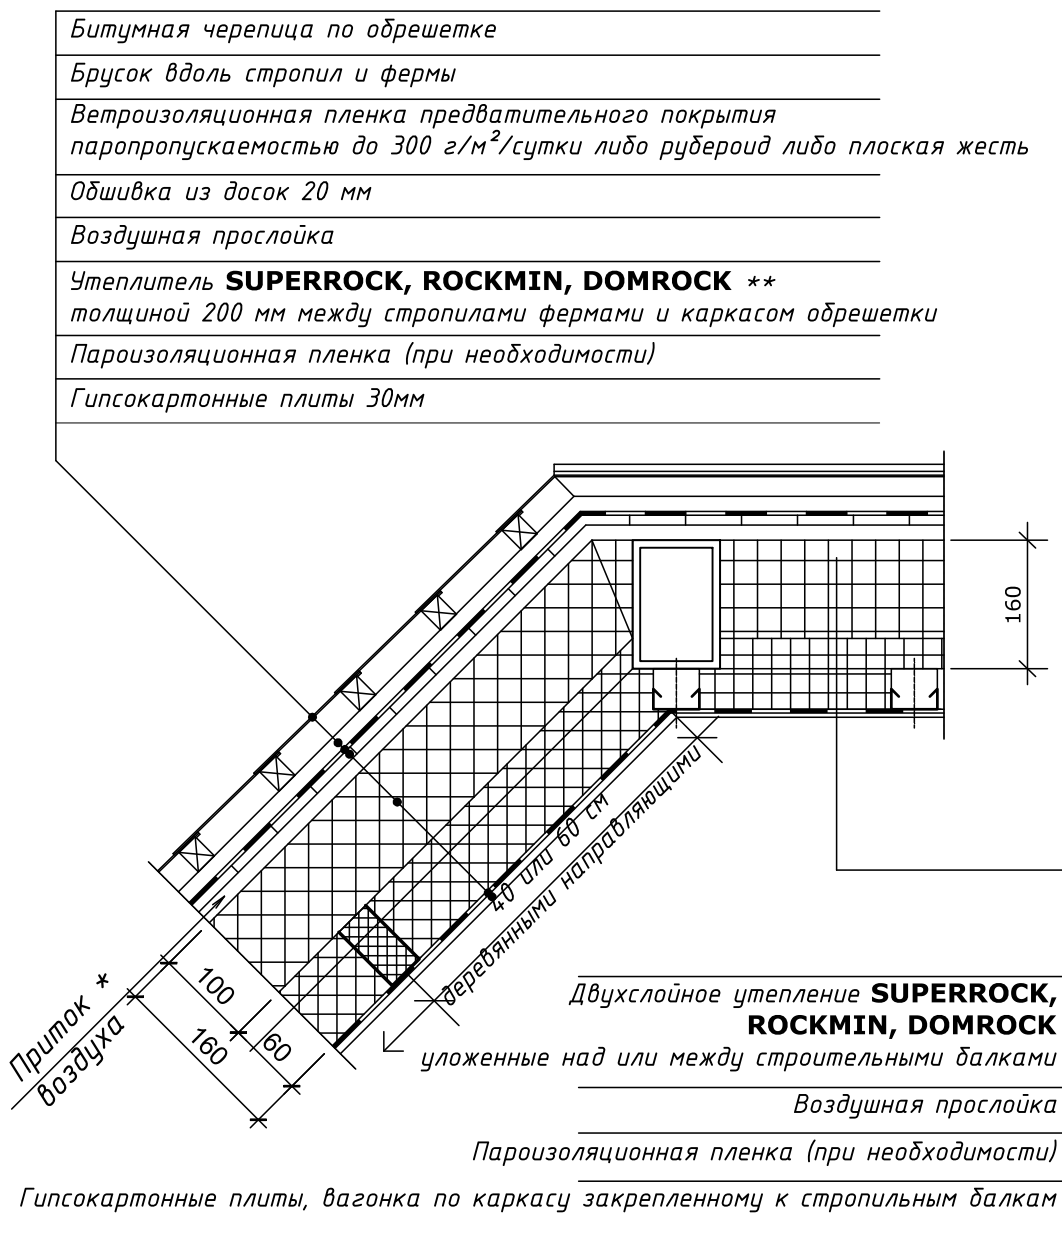

Узел крепления подвесного потолка

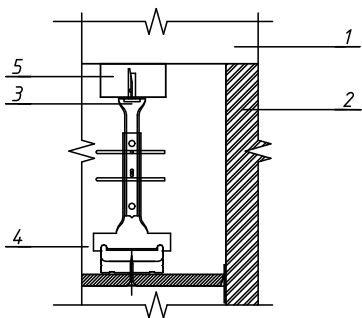


1. Металлическая балка
2. Стена здания
3. Конструкция крепления подвесного потолка из гипсокартона (поставляемая в наборе с гипсокартонными листами)
4. Подвесной потолок из гипсокартона
5. Деревянная балка для крепления элементов подвесного потолка

- * Для обеспечения циркуляции воздуха в вентилируемой прослойке суммарная площадь отверстий для притока воздуха под свесом должна составлять 0,002, а вылета в коньке или торцевых стенах 0,001 площади крыши чердака
- ** Все расширяемые (разжимные) маты, в том числе **DOMROCK** укладывать только в уровне стропильных балок.

						02 - 2019 - AP		
						Индивидуальный жилой дом, по адресу: Республика Крым, Муниципальное образование городской округ Алушта, п. Розовый		
Изм.	Кол.	Лист	№ док.	Подпись	Дата	Индивидуальный жилой дом	Стадия	Лист
							P	14
ГИП		Голенкова				Узлы и детали (окончание)		Индивидуальный Предприниматель Голенкова А.В. ОГРНИП 314910223200051
Разработ.		Гемдицкий						
Н. контр.		Коломиец						

Согласовано			
Взам. инв. №			
Подпись. Дата			
Инв. № подл.			


Фасад в осях 1-4

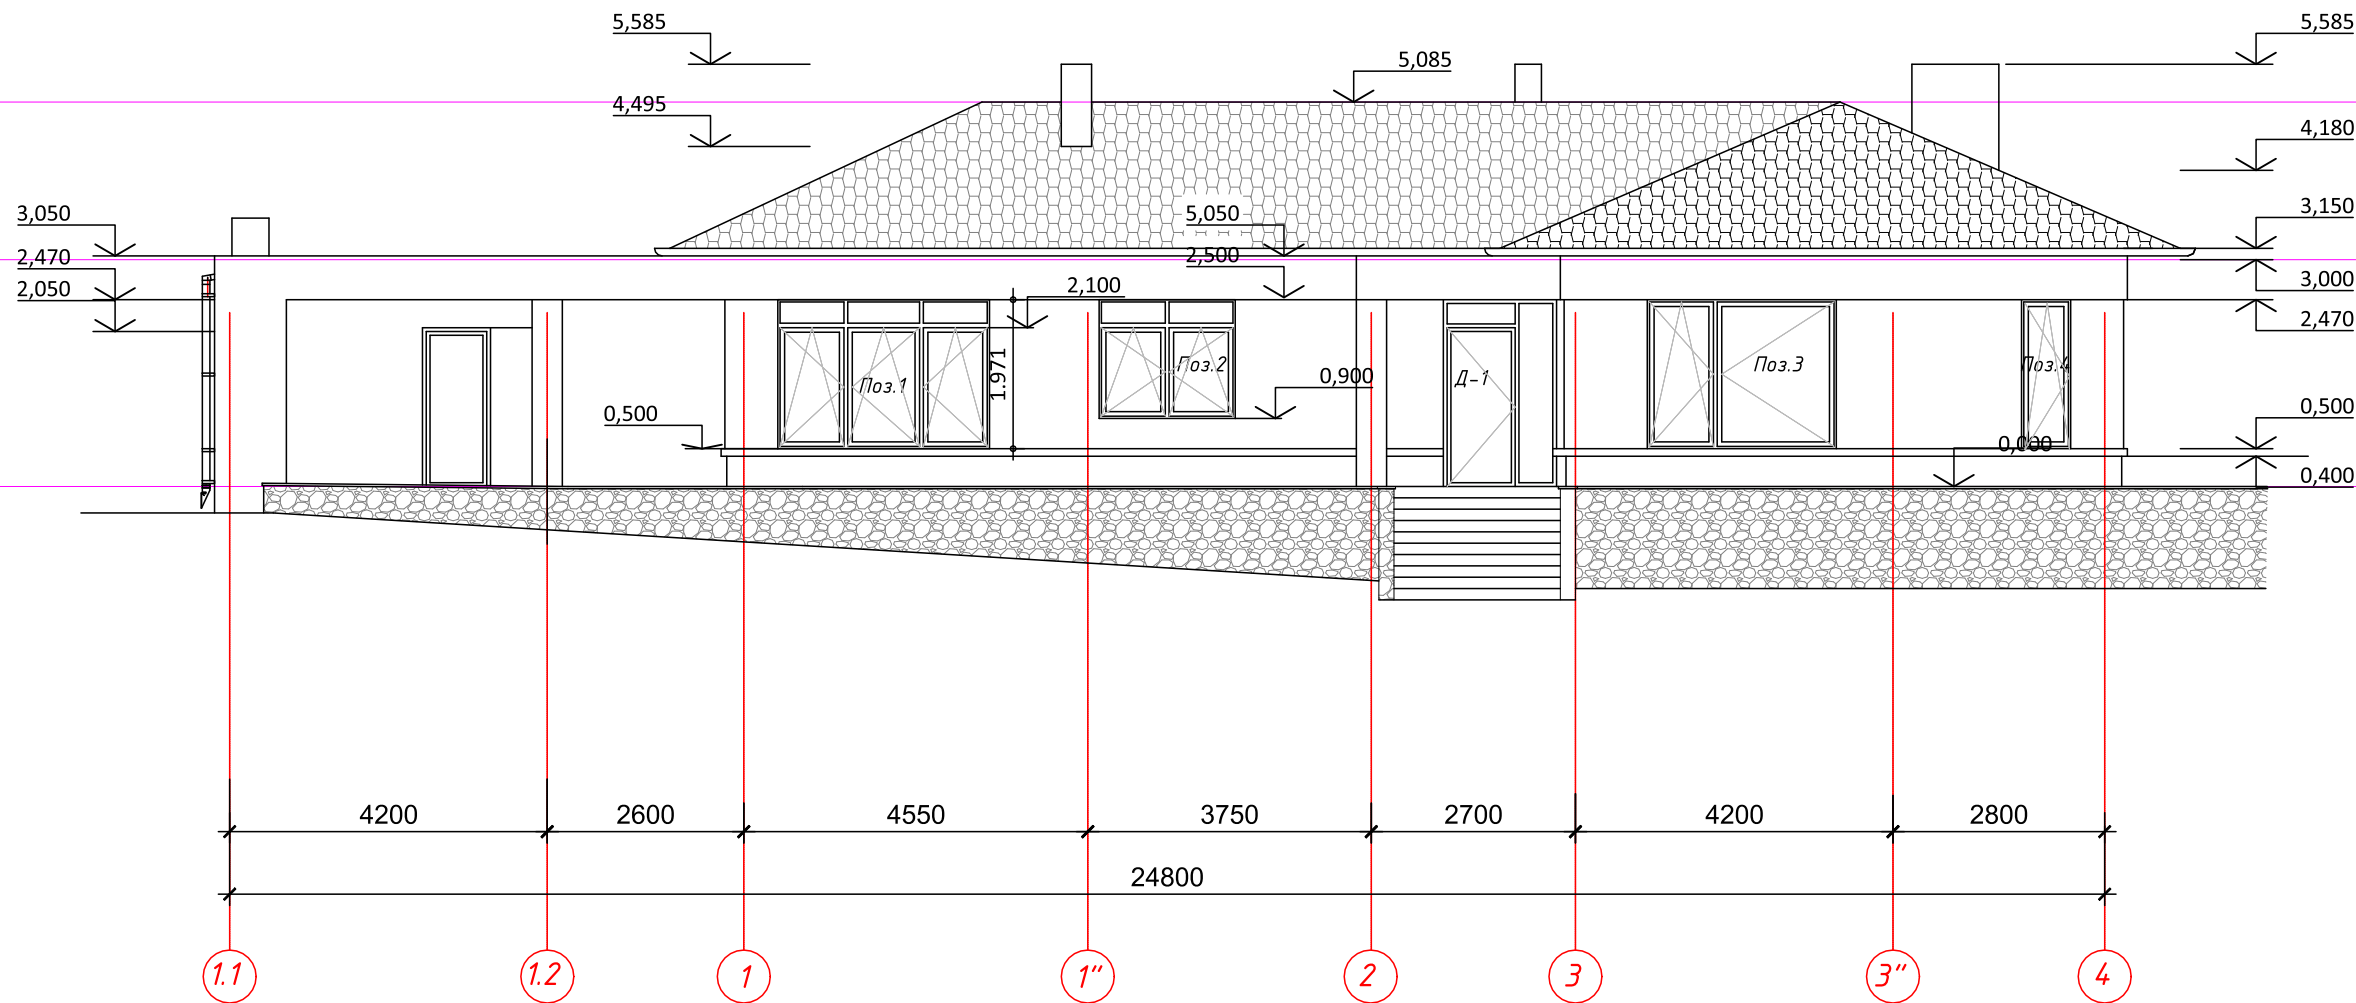

						02 - 2019 - AP			
						Индивидуальный жилой дом, по адресу: Республика Крым, Муниципальное образование городской округ Алушта, п. Розовый			
Изм.	Кол.	Лист	№ док.	Подпись	Дата				
						Индивидуальный жилой дом	Стадия	Лист	Листов
							P	15	
ГИП		Голенкова				Фасад в осях 1-4			
Разработ.		Гемдицкий							
Н. контр.		Коломиец							


Согласовано			
Взам. инв. №			
Подпись. Дата			
Инв. № подл.			

Фасад в осях 4-1

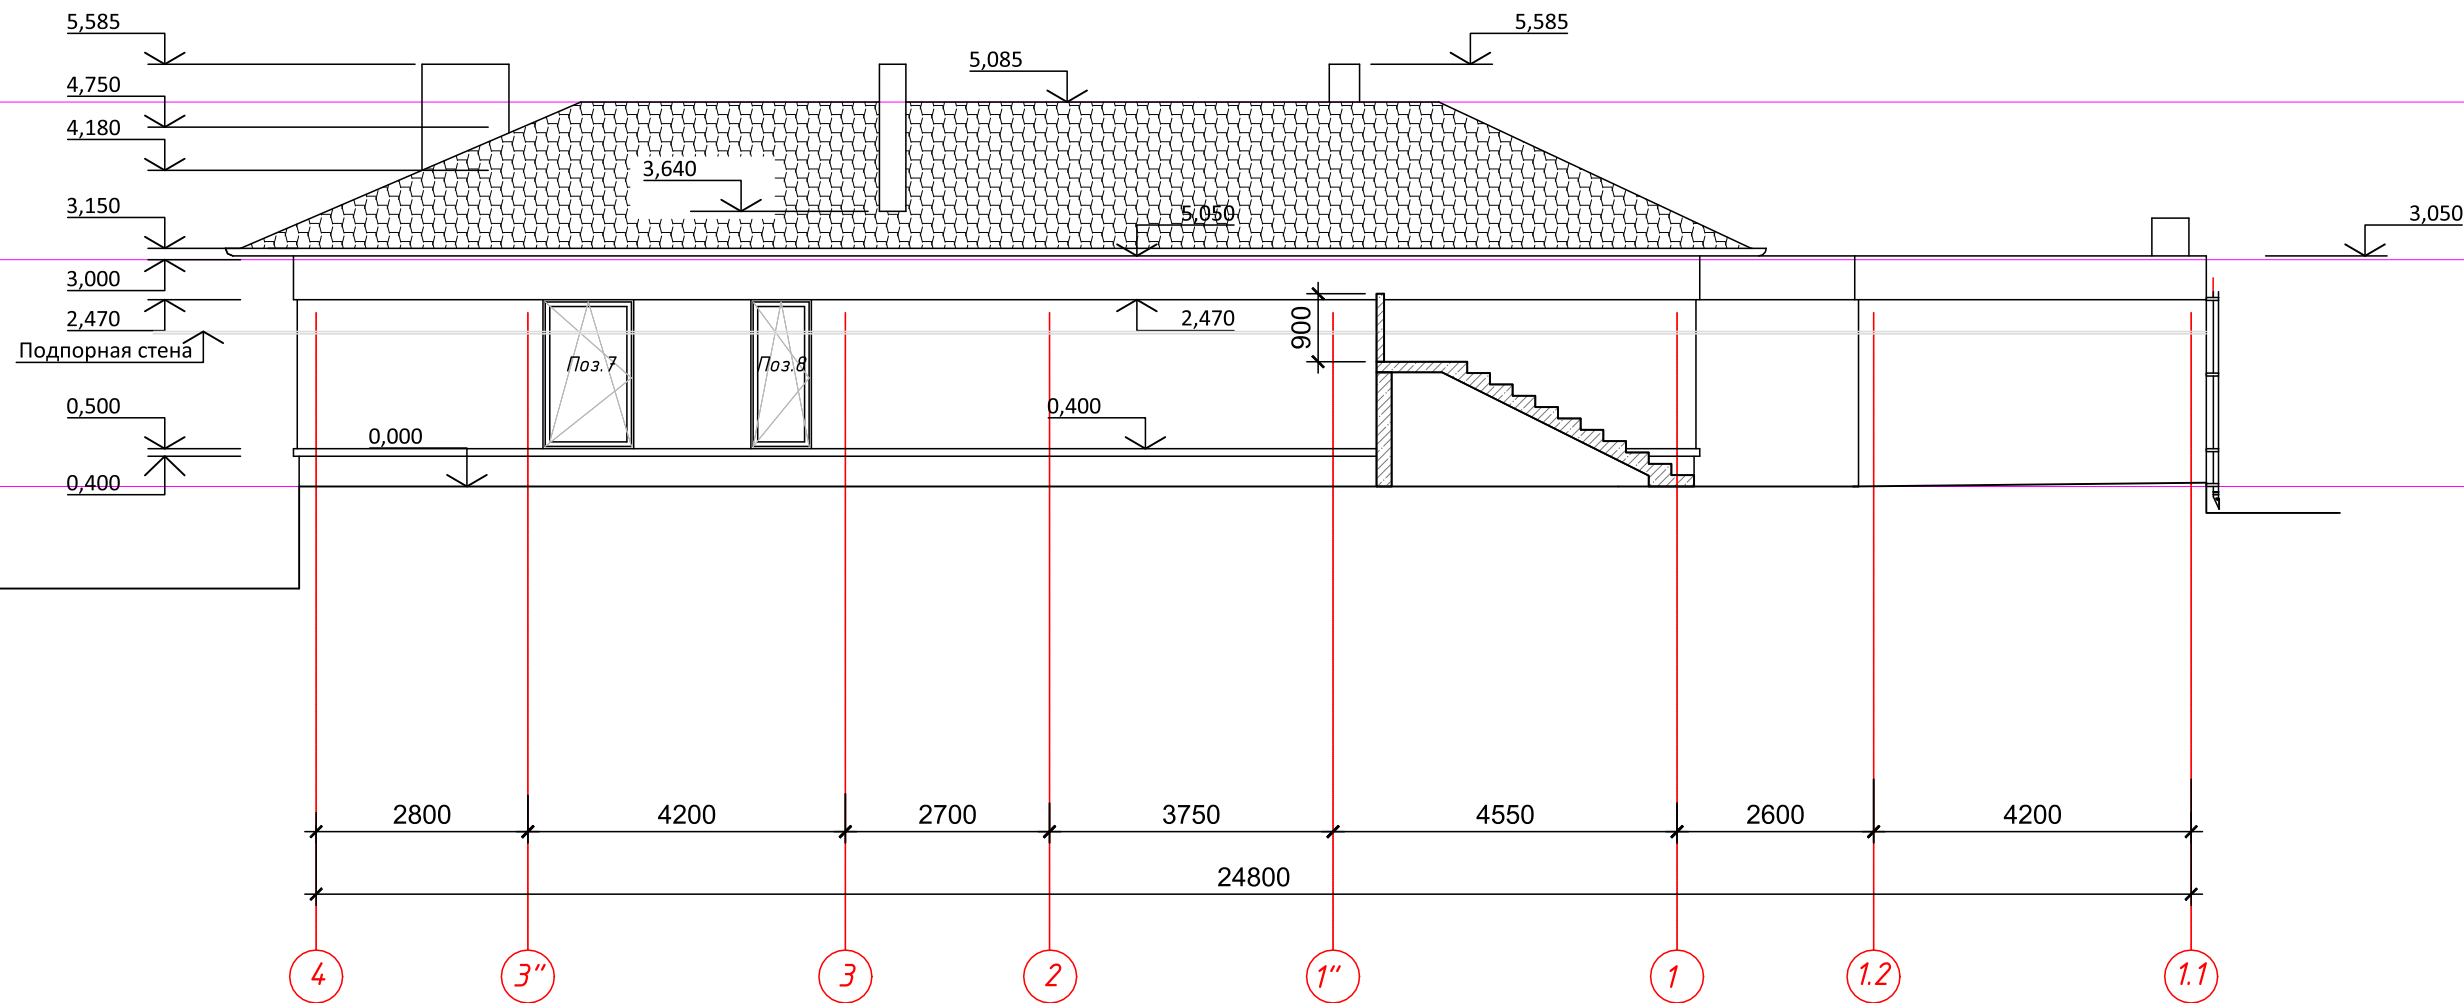


						02 - 2019 - AP			
						Индивидуальный жилой дом, по адресу: Республика Крым, Муниципальное образование городской округ Алушта, п. Розовый			
Изм.	Кол.	Лист	№ док.	Подпись	Дата				
						Индивидуальный жилой дом	Стадия	Лист	Листов
							P	16	
ГИП		Голенкова				Фасад в осях 4-1			
Разработ.		Гемдицкий							
Н. контр.		Коломиец							

Согласовано				
Взам. инв. №				
Подпись. Дата				
Инв. № подл.				

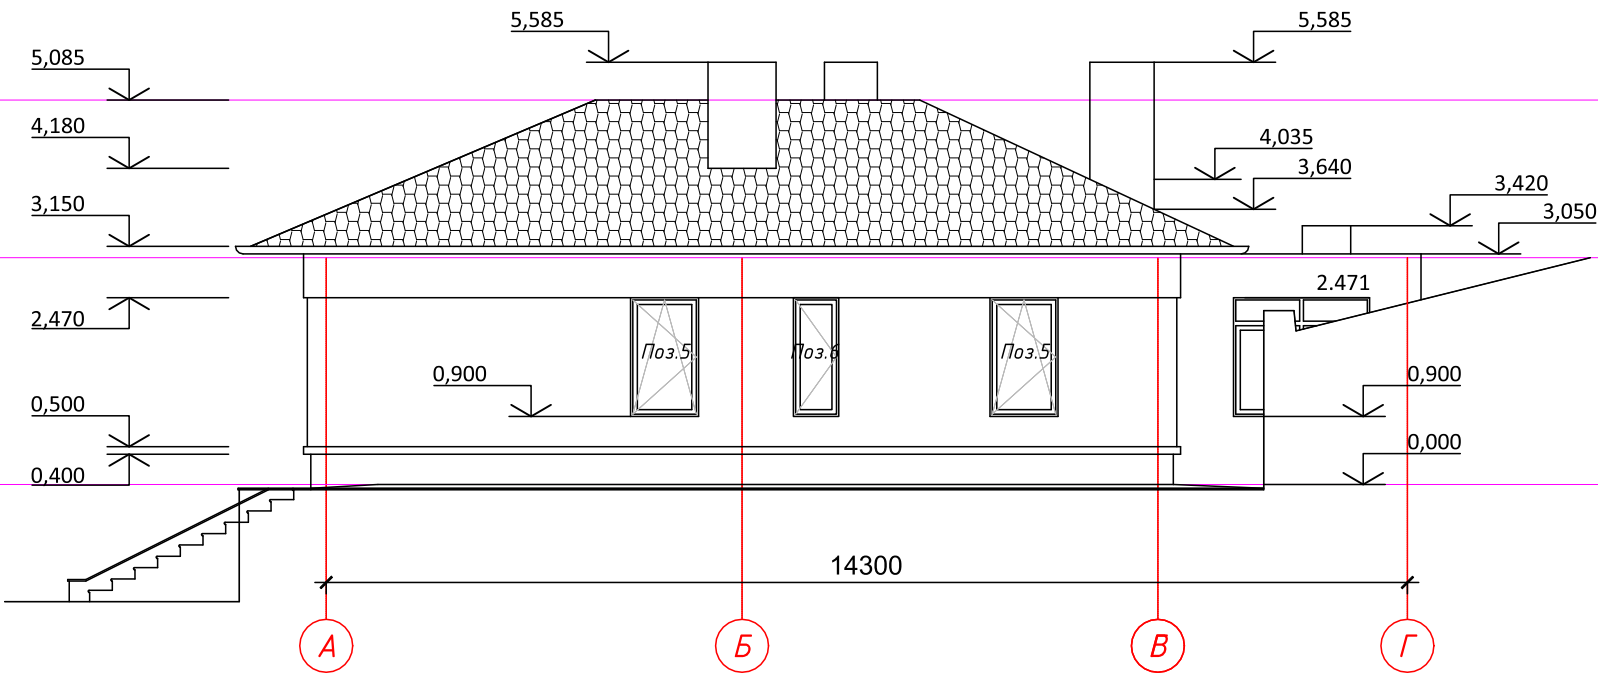


						02 - 2019 - AP			
						Индивидуальный жилой дом, по адресу: Республика Крым, Муниципальное образование городской округ Алушта, п. Розовый			
Изм.	Кол.	Лист	№ док.	Подпись	Дата				
						Индивидуальный жилой дом	Стадия	Лист	Листов
							P	17	
ГИП		Голенкова				Фасад в осях А-Г			
Разработ.		Гемдицкий							
Н. контр.		Коломиец							

Согласовано				
Взам. инв. №				
Подпись. Дата				
Инв. № подл.				

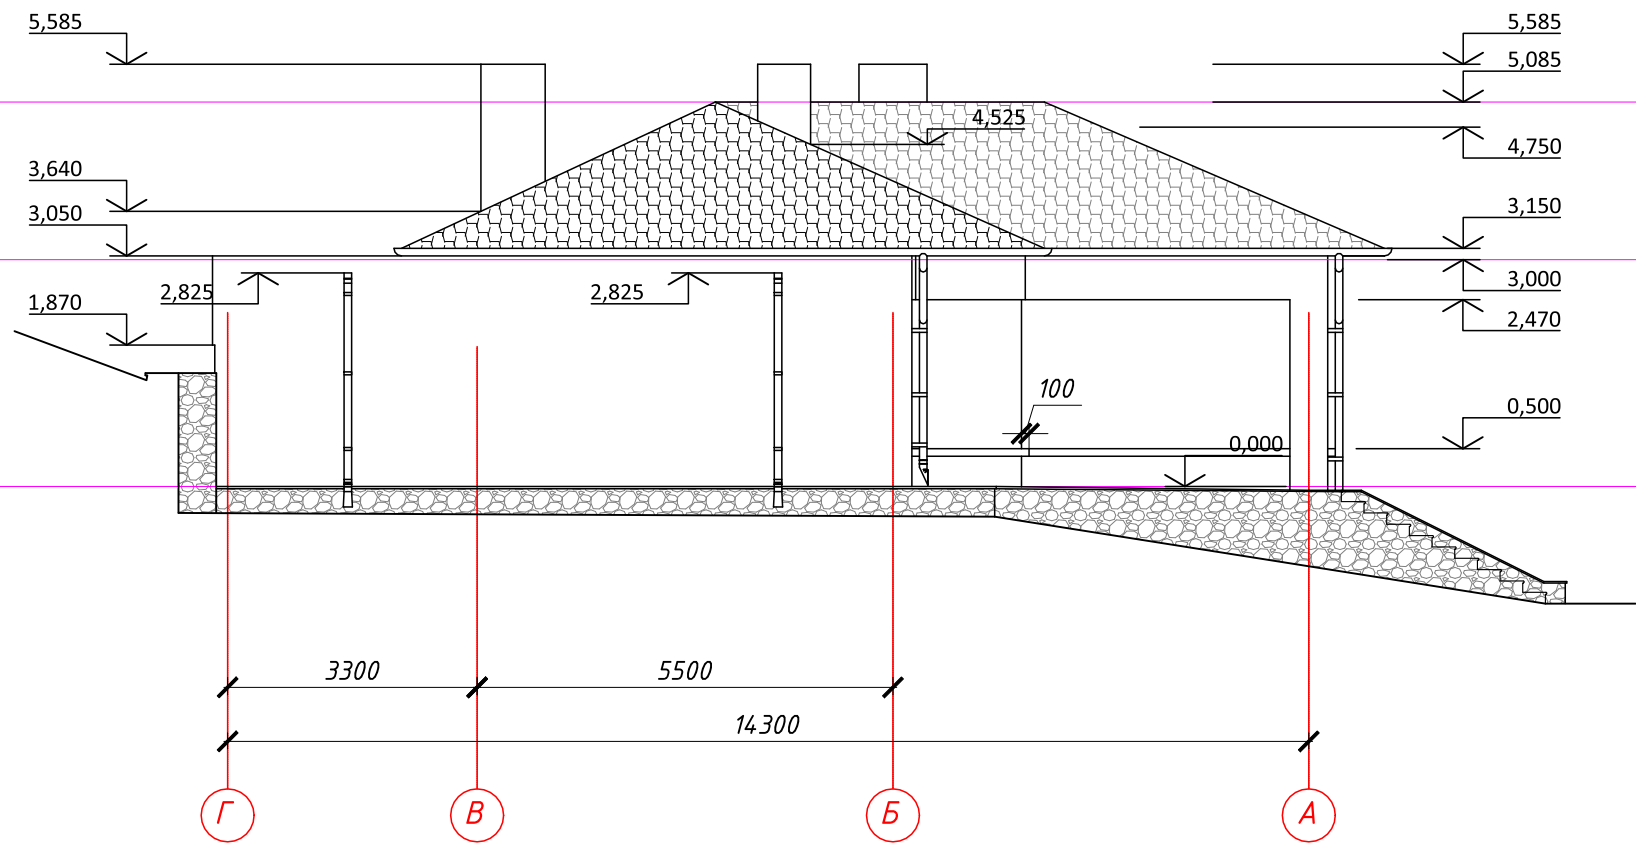


						02 - 2019 - AP		
						Индивидуальный жилой дом, по адресу: Республика Крым, Муниципальное образование городской округ Алушта, п. Розовый		
Изм.	Кол.	Лист	№ док.	Подпись	Дата			
						Индивидуальный жилой дом	Стадия	Лист
							P	18
ГИП		Голенкова				Фасад в осях Г-А	 самлайн проект инженерное обеспечение зданий	
Разработ.		Гемдицкий						
Н. контр.		Коломиец						
							Индивидуальный Предприниматель Голенкова А.В. ОГРНИП 314910223200051	


Согласовано			
Взам. инв. №			
Подпись. Дата			
Инв. № подл.			

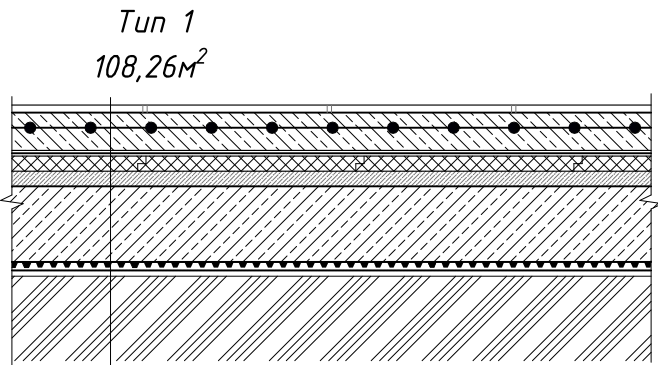


Керамическая плитка на клею	20мм
Монолитная стяжка с отопительной трубой	70мм
Защитная фольгированная пленка, отстенная изоляция	
Теплоизоляция из экструдированного пенополистирола	
Europlex	100мм
Бетонное основание, бетон В25	100мм
Гидроизоляционные бетонитовые маты Edilmodulo® / мембрана	
Bitustick по грунтовке Ceresit BT26, толщина 2,0 мм	
Бетонная подготовка-бетон В25,	
армированная стальной оцинкованной сеткой	50мм
Дренажная геомембрана ИЗОЛИТ	
Нетканый термически скрепленный геотекстиль Тураг® SF 56	
Уплотненный грунт основания	

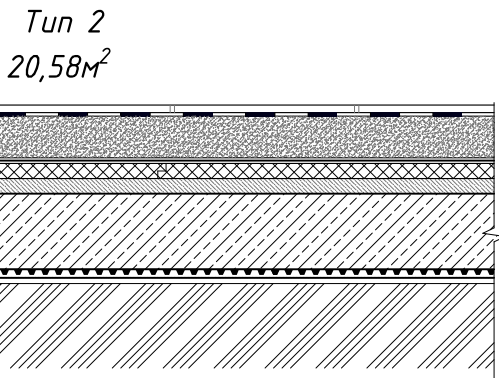

Керамическая плитка на клею	20мм
Обмазочная гидроизоляция на цементной основе	
Выравнивающая стяжка из ц/п р-ра М150	170мм
Бетонное основание, бетон В25	100мм
Гидроизоляционные бетонитовые маты Edilmodulo® / мембрана	
Bitustick по грунтовке Ceresit BT26, толщина 2,0 мм	
Бетонная подготовка-бетон В25,	
армированная стальной оцинкованной сеткой	50мм
Дренажная геомембрана ИЗОЛИТ	
Нетканый термически скрепленный геотекстиль Тураг® SF 56	
Уплотненный грунт основания	

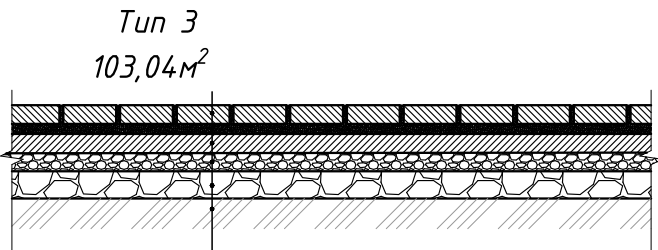

Бетонная плитка 300х300х50мм	
Цементно-песчаная смесь	-50мм
Монолитная ж/б подушка - бетон В15, сетка 50х50х4мм. ВР1.	-100мм
Мелкощебеночное основание фракции 5-10мм	- 100мм
Крупнощебеночная обратная засыпка фракции 20-40 мм	- 100мм
Уплотненный грунт основания	

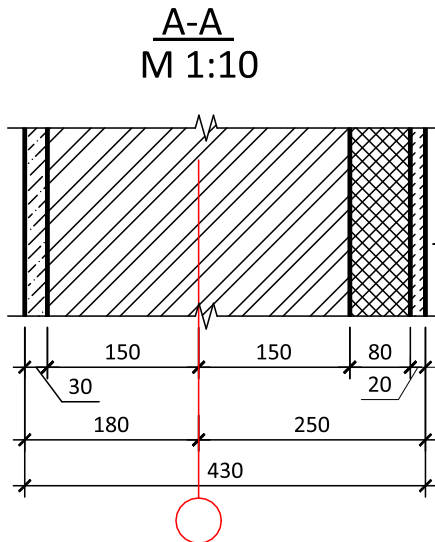

Декоративная фасадная штукатурка цементно-песчаным раствором М150 по сетке
Утеплитель-пенополистирол (j-600 кг/м куб)
Кладка из газоблока
Выравнивающая штукатурка из цементно-песчаного раствора М150


- Примечание
- Пол сауны вполнить по типу 1. Поверх уложенной плитки располагаются деревянные настилы из лиственных пород деревьев (осина, липа). В полу сауны выполнить трапы.
 - В полу сауны выполнить трап.
 - Обмазочную гидроизоляцию завести на стены на высоту 10см.
 - Выполнить заземление полов.

						02 - 2019 - AP			
						Индивидуальный жилой дом, по адресу: Республика Крым, Муниципальное образование городской округ Алушта, п. Розовый			
Изм.	Кол.	Лист	№ док.	Подпись	Дата				
						Индивидуальный жилой дом	Стадия	Лист	Листов
							Р	19	
ГИП		Голенкова				Элементы пола	 самлайн проект инженерное обеспечение зданий Индивидуальный Предприниматель Голенкова А.В. ОГРНИП 314910223200051		
Разработ.		Гемдицкий							
Н. контр.		Коломиец							


Спецификация элементов заполнения проемов

№	Наименование	Всего	Размеры проема. ВхН	Примечание
1	Оконный блок	1	2800х2000	с фрамугой 340мм
2	Оконный блок	1	1800х1600	с фрамугой 340мм
3	Оконный блок	1	2500х2000	
4	Оконный блок	1	650х2000	
5	Оконный блок	2	900х1800	
6	Оконный блок	1	600х1600	Окно сауны
7	Оконный блок	1	1200х2000	
8	Оконный блок	1	800х2000	
9	Оконный блок	1	1800х1600	с фрамугой 340мм


Позиция 1
Кол-во: 1шт

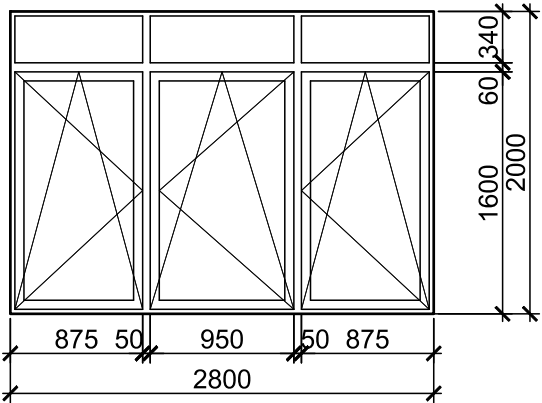


Позиция 2
Кол-во: 1шт

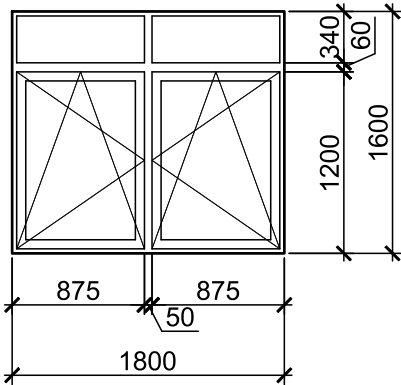


Позиция 3
Кол-во: 1шт

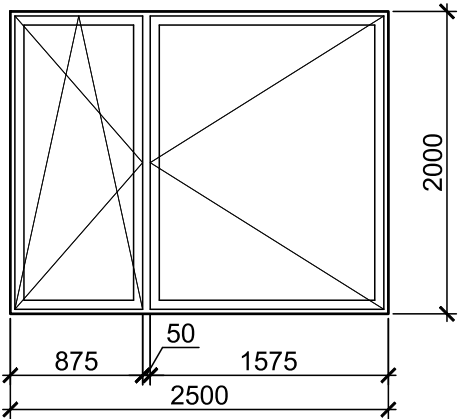


Позиция 4
Кол-во: 1шт

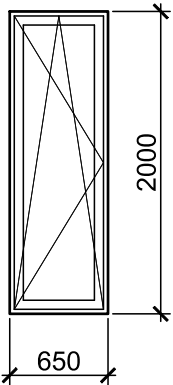


Позиция 5
Кол-во: 2шт

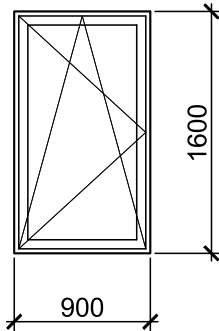


Позиция 6
Кол-во: 1шт

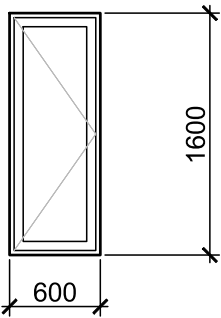


Позиция 7
Кол-во: 1шт

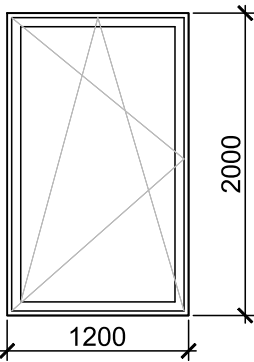

Позиция 8
Кол-во: 1шт

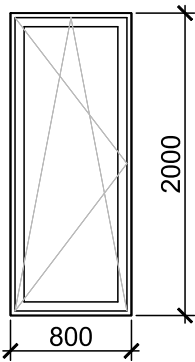

Позиция 9
Кол-во: 1шт

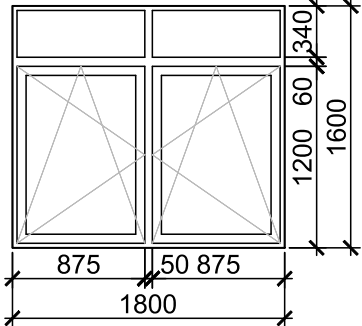

Примечания:


- перед заказом столярных изделий, проверить размеры проемов по-факту
- перед монтажом столярных изделий все проемы очистить от мусора и подготовить к установке.
- оконные и дверные системы должны соответствовать сопротивлению теплопередаче согласно СП 50.13330.2012
- формула сп должна соответствовать ветровым нагрузкам в данном регионе СП 20.13330.2011
- для изготовления оконных и дверных блоков рекомендуется использовать алюминиевый профиль Schüko AWS/ADS70HI, ASS70HI

						02 - 2019 - AP			
						Индивидуальный жилой дом, по адресу: Республика Крым, Муниципальное образование городской округ Алушта, п. Розовый			
Изм.	Кол.	Лист	№ док.	Подпись	Дата				
						Индивидуальный жилой дом	Стадия	Лист	Листов
							P	20	
ГИП		Голенкова				Эскизы заполнения оконных и дверных проемов (начало) Спецификация			
Разработ.		Гемдицкий							
Н. контр.		Коломиец							


Согласовано			
Взам. инв. №			
Подпись. Дата			
Инв. № подл.			

СПЕЦИФИКАЦИЯ ЭЛЕМЕНТОВ ЗАПОЛНЕНИЯ ПРОЕМОВ. ВЕДОМОСТЬ ПРОЕМОВ.						
Марка, поз.	Обозначение	Наименование	Кол-во на этаж	Всего	Размер проема, мм (Н x б)	Примечание
			отм. 0,00			
Д-1	Индивидуальный	ДГ25-15,П наружный дверной блок	1	1	2500 x 1500	Дверь глухая с боковым стеклом и фрамугой
Д-2	Индивидуальный	ДГ 21-9, Л дверной блок	2	2	2100 x 900	
Д-3	Индивидуальный	ДГ 21-8,П дверной блок	4	4	2100 x 800	
Д-4	Индивидуальный	ДО 21-7, Л дверной блок	1	1	2100 x 700	Дверь сауны (см. примечание)
Д-5	Индивидуальный	ДГ25-16,П наружный дверной блок	1	1	2500 x 1600	Дверь глухая с боковым стеклом и фрамугой
Д-6	Индивидуальный	ДГ21-9,Л наружный дверной блок	1	1	2100 x 900	

Д-1
Кол-во: 1шт

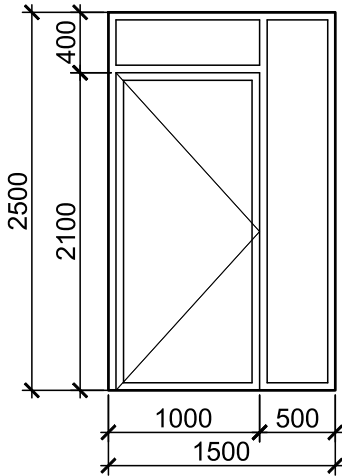

Д-5
Кол-во: 1шт

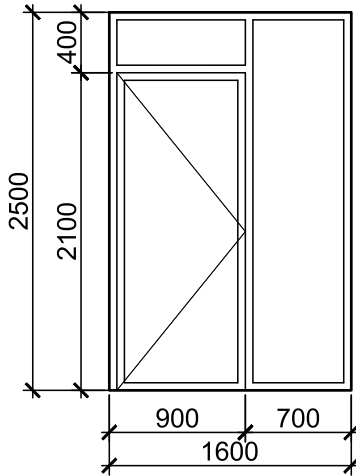

Примечания:

1.Дверь из жароустойчивого закаленного стекла триплекс толщиной 80-100 мм.

						02 - 2019 - АР		
						Индивидуальный жилой дом, по адресу: Республика Крым, Муниципальное образование городской округ Алушта, п. Розовый		
Изм.	Кол.	Лист	№ док.	Подпись	Дата			
						Индивидуальный жилой дом	Стадия	Лист
							Р	21
ГИП		Голенкова				Эскизы заполнения оконных и дверных проемов (окончание) Спецификация		Индивидуальный Предприниматель Голенкова А.В. ОГРНИП 314910223200051
Разработ.		Гемдицкий						
Н. контр.		Коломиец						

Согласовано			
Взам. инв. №			
Подпись. Дата			
Инв. № подл.			



Облицовка керамогранитом
Цвет - Brown Silver (Браун Сильвер)

Декоративная штукатурка. Покраска высококачественными
фасадными красками.
Цвет - бежевый

Облицовка декоративной керамической плиткой с эффектом кирпичной кладки
Цвет - кофейный

Декоративная штукатурка. Покраска высококачественными фасадными красками
Цвет - бежевый

						02 - 2019 - AP			
						Индивидуальный жилой дом, по адресу: Республика Крым, Муниципальное образование городской округ Алушта, п. Розовый			
Изм.	Кол.	Лист	№ док.	Подпись	Дата				
						Индивидуальный жилой дом	Стадия	Лист	Листов
							P	22	
ГИП		Голенкова				Отделка фасадов (Общий вид)	 самлайн проект инженерное обеспечение зданий Индивидуальный Предприниматель Голенкова А.В. ОГРНИП 314910223200051		
Разработ.		Гемдицкий							
Н. контр.		Коломиец							

Согласовано			
Взам. инв. №			
Подпись. Дата			
Инв. № подл.			



Кровля – мягкая черепица Shinglas
Цвет – коньячный

Декоративная штукатурка. Покраска высококачественными
фасадными красками.
Цвет – бежевый

Облицовка керамогранитом
Цвет – Brown Silver (Браун Сильвер)

Облицовка декоративной керамической плиткой с эффектом кирпичной кладки
Цвет – кофейный

						02 – 2019 – АР		
						Индивидуальный жилой дом, по адресу: Республика Крым, Муниципальное образование городской округ Алушта, п. Розовый		
Изм.	Кол.	Лист	№ док.	Подпись	Дата	Индивидуальный жилой дом	Стадия	Лист
							Р	23
ГИП		Голенкова				Отделка фасадов (Общий вид)		
Разработ.		Гемдицкий						
Н. контр.		Коломиец						

Согласовано			
Взам. инв. №			
Подпись. Дата			
Инв. № подл.			

Декоративная штукатурка. Покраска высококачественными
фасадными красками.
Цвет - бежевый



Облицовка декоративной керамической плиткой с эффектом кирпичной кладки
Цвет - кофейный

						02 - 2019 - AP			
						Индивидуальный жилой дом, по адресу: Республика Крым, Муниципальное образование городской округ Алушта, п. Розовый			
Изм.	Кол.	Лист	№ док.	Подпись	Дата				
						Индивидуальный жилой дом	Стадия	Лист	Листов
							P	24	
ГИП		Голенкова				Отделка фасадов (Общий вид)			
Разработ.		Гемдицкий							
Н. контр.		Коломиец							

Согласовано			
Взам. инв. №			
Подпись. Дата			
Инв. № подл.			



Облицовка травертином
Цвет - Brown Silver (Браун Сильвер)

Кровля - мягкая черепица Shinglas
Цвет - коньячный

Декоративная штукатурка. Покраска высококачественными
фасадными красками.
Цвет - бежевый

Облицовка декоративной керамической плиткой с эффектом кирпичной кладки
Цвет - кофейный

						02 - 2019 - AP			
						Индивидуальный жилой дом, по адресу: Республика Крым, Муниципальное образование городской округ Алушта, п. Розовый			
Изм.	Кол.	Лист	№ док.	Подпись	Дата				
						Индивидуальный жилой дом	Стадия	Лист	Листов
							P	25	
ГИП		Голенкова				Отделка фасадов (Общий вид)	 самлайн проект инженерное обеспечение зданий Индивидуальный Предприниматель Голенкова А.В. ОГРНИП 314910223200051		
Разработ.		Гемдицкий							
Н. контр.		Коломиец							

Согласовано			
Взам. инв. №			
Подпись. Дата			
Инв. № подл.			

ВЕДОМОСТЬ НАРУЖНОЙ ОТДЕЛКИ					
Номер пов-ности	Наименование поверхности	Вид отделки	Площадь, м кв.	Образец колера	Примечание
1	Цоколь	Облицовка керамогранитом под натуральный камень. Цвет - Brown Silver (Браун Сильвер)	52,92		
2	Стены	Облицовка декоративной керамической плиткой с эффектом кирпичной кладки Катгоск. Цвет - кофейный	86,91		Клинкерный кирпич, 34270
3	Стены, колонны и вентшахты	Декоративная штукатурка. Покраска высококачественными фасадными красками. Цвет - бежевый	120,95		
4	Потолок зоны дәрбәкә	Декоративная штукатурка. Покраска высококачественными фасадными красками. Цвет - бежевый	28,34		
5	Рамы оконных проемов	Металлопластик. Цвет - белый		Белый	
6	Кровля	Кровля - мягкая черепица Shinglas. Цвет - коньячный	230,00		Континент, цвет Европа Джаз, цвет Сицилия

Примечание.
1. За основу приняты выкраски альбома колеров RAL-K1(ORIGINAL) фирмы TEKNOS.
При использовании выкрасок других производителей, цветовое решение согласовать с автором проекта.

						02 - 2019 - AP			
						Индивидуальный жилой дом, по адресу: Республика Крым, Муниципальное образование городской округ Алушта, п. Розовый			
Изм.	Кол.	Лист	№ док.	Подпись	Дата				
						Индивидуальный жилой дом	Стадия	Лист	Листов
							P	26	
ГИП		Голенкова							
Разработ.		Гемдицкий				Ведомость наружной отделки	 самлайн проект инженерное обеспечение зданий Индивидуальный Предприниматель Голенкова А.В. ОГРНИП 314910223200051		
Н. контр.		Коломиец							