



ИП Голенкова Анна Владимировна
ИНН 910300016034 ОГРНИП 314910223200051
р/с 40802810642680100764 в РНКБ Банк (ПАО)
корр. счет №30101810335100000607, БИК 043510607
Юр. адрес: 298612, Республика Крым, г. Ялта, ул. Ореховая, 31/1/31
Факт. Адрес: 298612, Республика Крым, г. Ялта, ул. Московская, 43, офис 5
тел.: +7 978 750 47 55; +7 978 053-12-42

САМОРЕГУЛИРУЕМАЯ ОРГАНИЗАЦИЯ АССОЦИАЦИЯ
"МЕЖРЕГИОНАЛЬНОЕ ОБЪЕДИНЕНИЕ ПРОЕКТНЫХ ОРГАНИЗАЦИЙ"
СРО-П-014-05082009 Рег.№ 767-18 от 06.07.2018г.

Заказчик: **КОСЯКОВ А.Н.**

ИНДИВИДУАЛЬНЫЙ ЖИЛОЙ ДОМ, ПО АДРЕСУ:
РЕСПУБЛИКА КРЫМ, МУНИЦИПАЛЬНОЕ ОБРАЗОВАНИЕ
ГОРОДСКОЙ ОКРУГ АЛУШТА, п. РОЗОВЫЙ

РАБОЧАЯ ДОКУМЕНТАЦИЯ

Генеральный план

02-2019-ГП

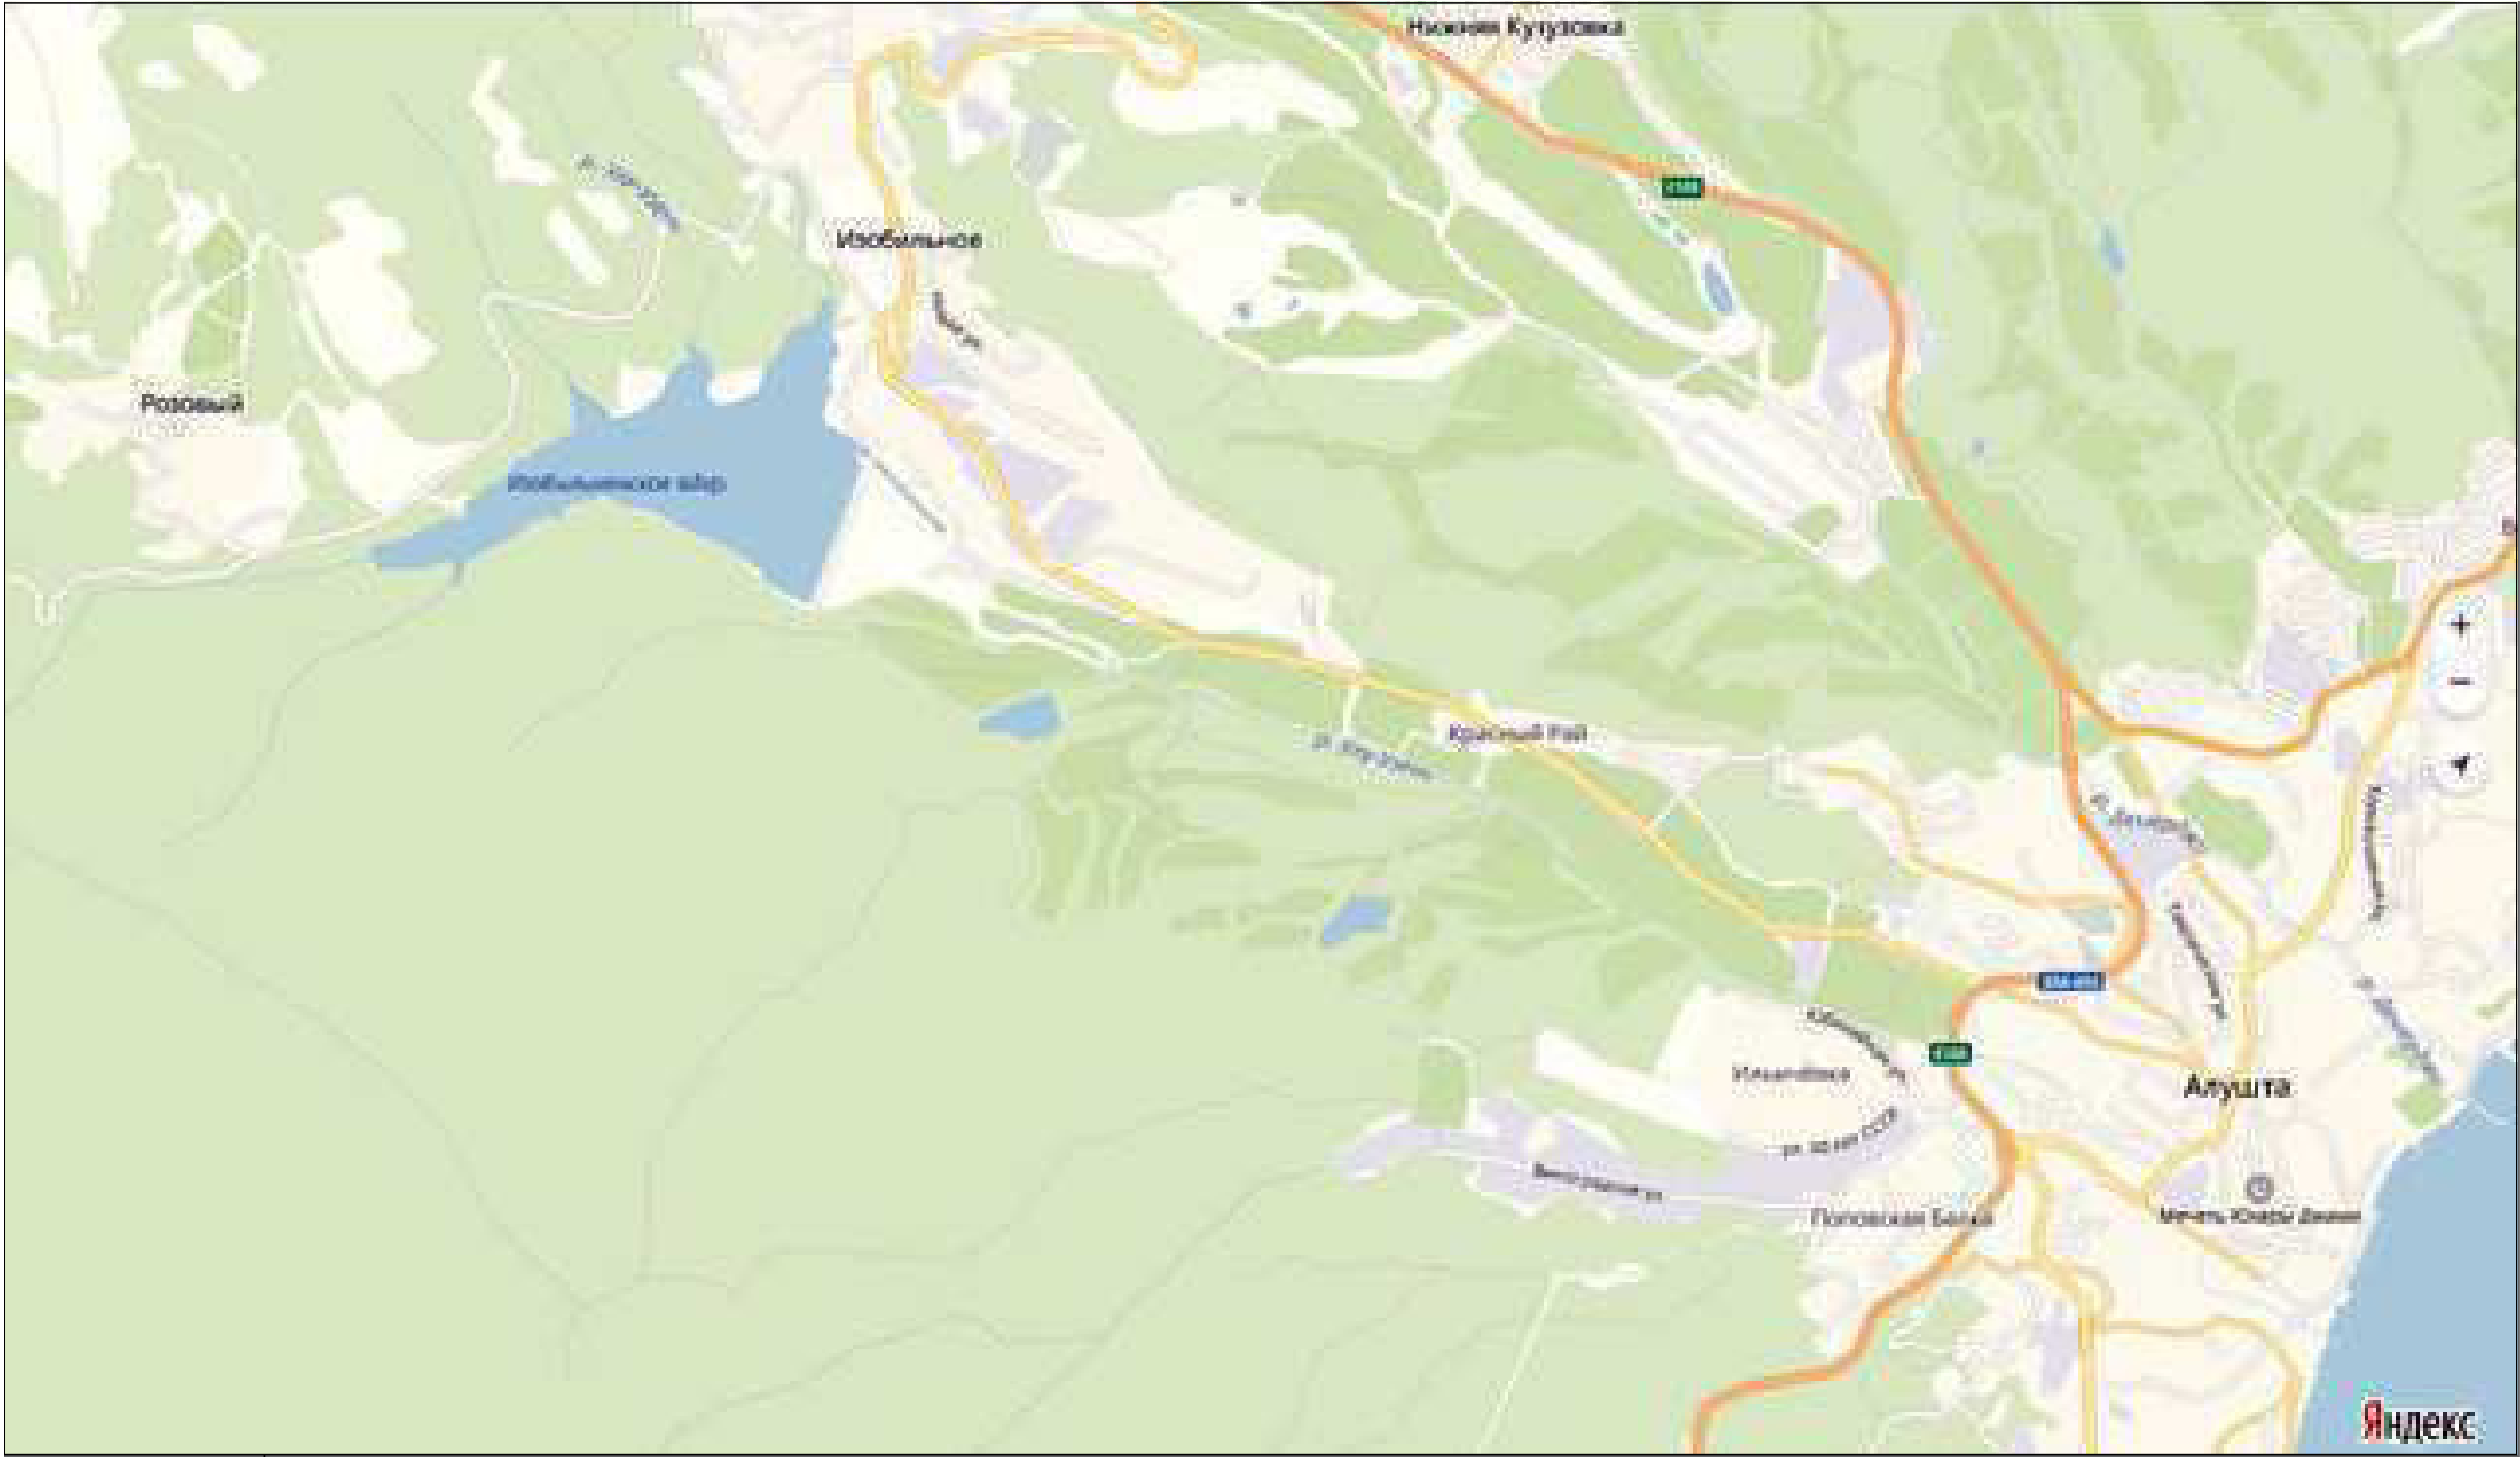
Главный инженер проекта

Голенкова А.В.

2019

Согласовано				
Взам. инв. №				
Подпись, Дата				
Инв. № подл.				

Согласовано					
Инв. № подл.	Взам. инв. №				
	Подпись. Дата				



Расположение участка







						02 - 2019 - ГП		
						Индивидуальный жилой дом, по адресу: Республика Крым, Муниципальное образование городской округ Алушта, п. Розовый		
Изм.	Кол.	Лист	№ док.	Подпись	Дата		Стадия	Лист
							Р	2
ГИП		Голенкова				Ситуационный план	 самлайн проект инженерное обеспечение зданий	Индивидуальный Предприниматель Голенкова А.В. ОГРНИП 314910223200051
Разработ.		Гемдицкий						
Н. контр.		Коломиец						

ОПОРНЫЙ ПЛАН М 1:200

ЭКСПЛИКАЦИЯ

№ по г. пл.	НАИМЕНОВАНИЕ	ПРИМЕЧАНИЯ
1	Существующий деревянный дом	
2	Существующий въезд на участок	
3	Орех сохраняемый	
4	Орех сохраняемый	
5	Куст кизила сохраняемый	
6	Разбираемая подпорная стена	
7	Разбираемая подпорная стена	
8	Глиняная дорога	

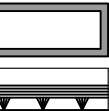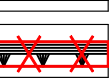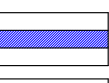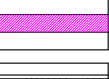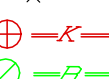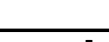УСЛОВНЫЕ ОБОЗНАЧЕНИЯ

- | | |
|---|--|
|  | • Разбираемые здания и сооружения |
|  | • Проектируемые здания и сооружения |
|  | • Существующие подпорные стены |
|  | • Разбираемые подпорные стены |
|  | • Проектируемые подпорные стены Тип 1 |
|  | • Проектируемые подпорные стены Тип 2 |
|  | • Проектируемые лестницы |
|  | • Ограждение |
|  | • Канализация |
|  | • Водопровод |
|  | • Электрический кабель 04 кВ |
|  | • Точки разбивки осей зданий и сооружений |
|  | • Условная граница проектируемого здания, сооружения |
|  | • Граница землепользования |

						02 - 2019 - ГП			
						Индивидуальный жилой дом, по адресу: Республика Крым, Муниципальное образование городской округ Алушта, п. Розовый			
Изм.	Кол.	Лист	№ док.	Подпись	Дата		Стадия	Лист	Листов
							Р	З	
ГИП	Голенкова					Опорный план М 1:200	 самлайн проект инженерное обеспечение зданий	Индивидуальный Предприниматель Голенкова А.В. ОГРНИП 314910223200051	
Разработ.	Гемдицкий								
Н. контр.	Коломиец								

ГЕНПЛАН М 1:200

ЭКСПЛИКАЦИЯ

№ по г. пл.	НАИМЕНОВАНИЕ	№ ТИП. ПРОЕКТ	ПЛОЩ. ЗАСТР. М. КВ.	СТР. ОБЪЕМ, М. КУБ.	ПРИМЕЧАНИЯ
1	Проектируемый жилой дом	Индив.	156,09	-	
2	Терраса		54,57	-	
3	Зона барбекю		37,48	-	
4	Мастерская		16,68	-	
5	Парковка		61,15	-	

ТЭП по генплану

- Площадь участка - 1016.00 м2 -100%
- Площадь застройки - 210.90 м2 -20.8%
дом - 156.00 м2
мастерская - 54,90 м2
- Площадь озеленения - 546.00 м2 -53.8%
- Площадь покрытий - 313.00 м2 -25.4%
- Навес с барбекю - 36.00 м2

ТЭП по зданию:

- Площадь застройки - 156.00 м2
- Этажность - 1 этаж
- Количество этажей - 1
- Общая площадь здания - 132.90 м2
- Общая площадь помещений - 119.27 м2
- Жилая площадь - 40.95 м2
- Количество комнат - 3
- Строительный объем - 700 м3

Условные обозначения

- Разбираемые здания и сооружения
- Проектируемые здания и сооружения
- Существующие подпорные стены
- Разбираемые подпорные стены
- Проектируемые подпорные стены Тип 1
- Проектируемые подпорные стены Тип 2
- Проектируемые лестницы
- Ограждение
- Канализация
- Водопровод
- Электрический кабель 04 кВ
- Граница землепользования

02 - 2019 - ГП

Индивидуальный жилой дом, по адресу: Республика Крым,
Муниципальное образование городской округ Алушта,
п. Розовый

Стадия	Лист	Листов
Р	4	

Генплан. М 1:200

самлайн проект
Индивидуальный
Предприниматель
Голенкова А.В.
ОГРНИП
314910223200051

Формат А3

Согласовано					
Взам. инв. №					
Подпись. Дата					
Инв. № подл.					


ПЛАН ОРГАНИЗАЦИИ РЕЛЬЕФА
М 1:200

ЭКСПЛИКАЦИЯ

№ по г. пл.	НАИМЕНОВАНИЕ	№ ТИП. ПРОЕКТ.	ПЛОЩ. ЗАСТР. М. КВ.	СТР. ОБЪЕМ, М. КУБ.	ПРИМЕЧАНИЯ
1	Проектируемый жилой дом	Индив.	156,09	-	
2	Терраса		54,57	-	
3	Зона барбекю		37,48	-	
4	Мастерская		16,68	-	
5	Парковка		61,15	-	

Условные обозначения

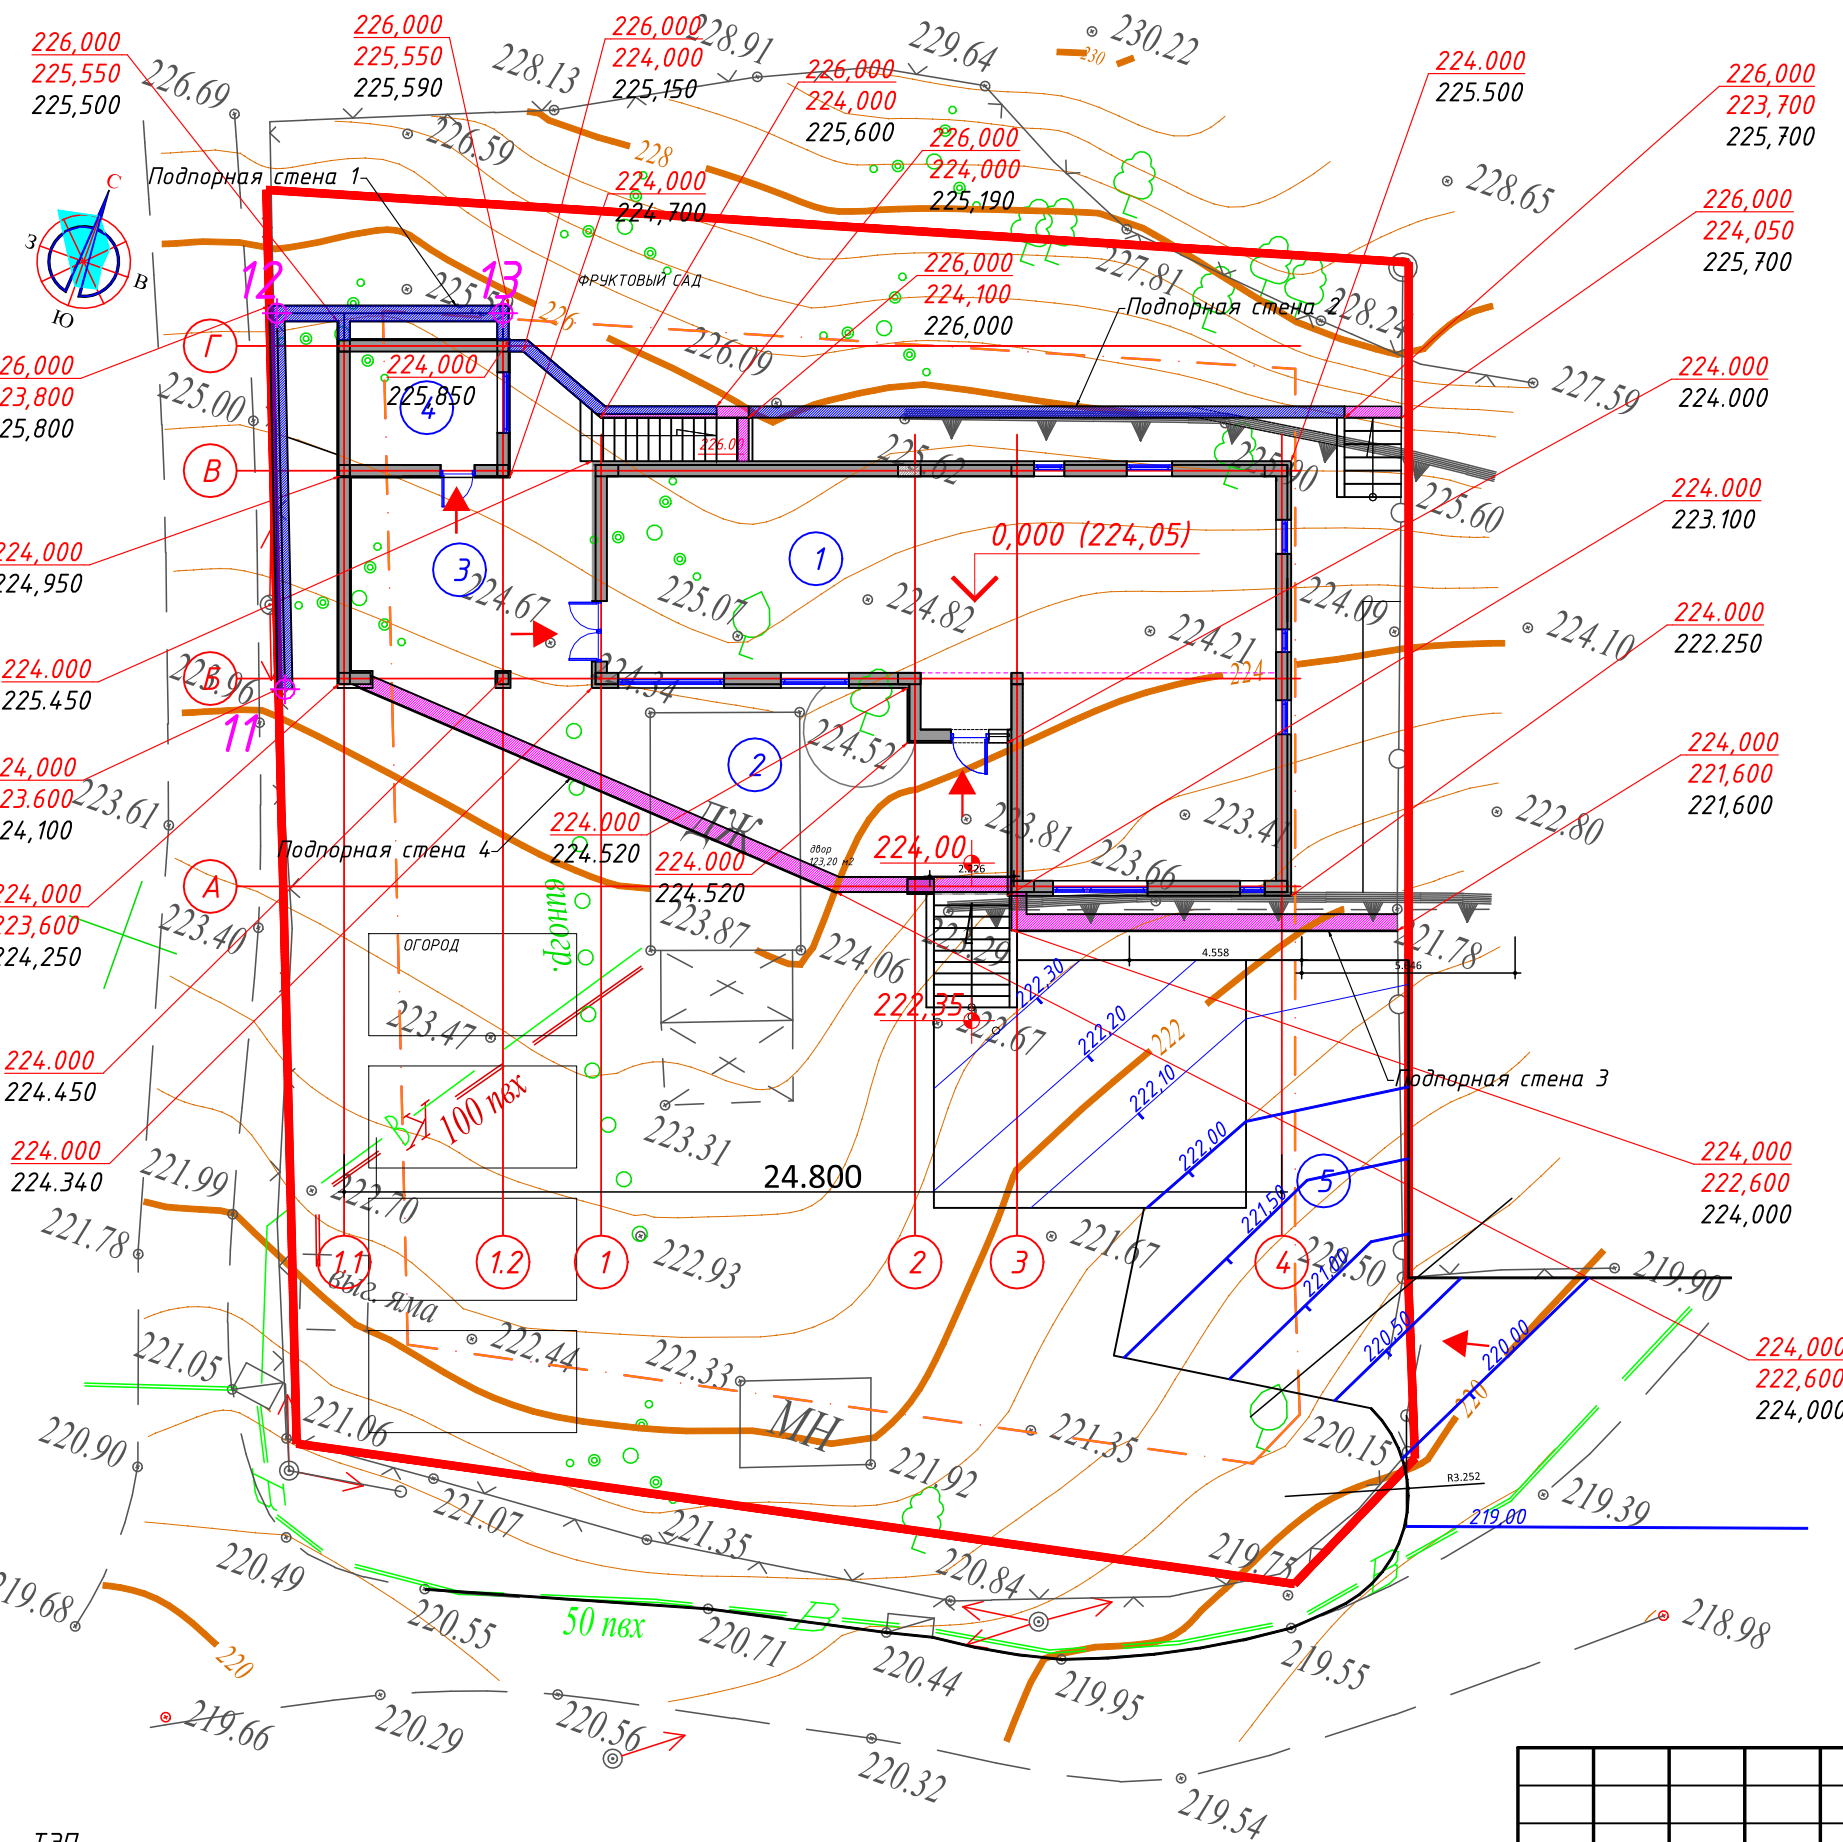- ✕ ✕ ✕ ✕ КН ✕ ✕ ✕ ✕ • Разбираемые здания и сооружения
- ▬ ▬ ▬ ▬ ▬ ▬ ▬ ▬ ▬ ▬ • Проектируемые здания и сооружения
- ▬ ▬ ▬ ▬ ▬ ▬ ▬ ▬ ▬ ▬ • Существующие подпорные стены
- ▬ ▬ ▬ ▬ ▬ ▬ ▬ ▬ ▬ ▬ • Разбираемые подпорные стены
- ▬ ▬ ▬ ▬ ▬ ▬ ▬ ▬ ▬ ▬ • Проектируемые подпорные стены Тип 1
- ▬ ▬ ▬ ▬ ▬ ▬ ▬ ▬ ▬ ▬ • Проектируемые подпорные стены Тип 2
- ▬ ▬ ▬ ▬ ▬ ▬ ▬ ▬ ▬ ▬ • Проектируемые лестницы
- — — — — — — — — — — — • Ограждение
- — — — — — — — — — — — • Канализация
- — — — — — — — — — — — • Водопровод
- — — — — — — — — — — — • Электрический кабель 04 кВ
- — — — — — — — — — — — • Граница землепользования
- 000,000 Проектируемая отметка верха
- 000,000 Проектируемая отметка низа
- 000,000 Существующая отметка




- ТЭП
- Площадь участка - 1015 м²
 - Площадь застройки - 210.25 м²
жилой дом - 156.09 м²
навес, мастерская - 54.16 м²
 - Площадь озеленения -
 - Площадь покрытий -
 - Общая площадь здания - 119.27 м²
 - Площадь мастерской - 16.68 м²

						02 - 2019 - ГП		
						Индивидуальный жилой дом, по адресу: Республика Крым, Муниципальное образование городской округ Алушта, п. Розовый		
						Стадия	Лист	Листов
						Р	5	
						План организации рельефа. М 1:200		
						самлайн проект Индивидуальный Предприниматель Голенкова А.В. ОГРНИП 314910223200051		
						Формат А3		






Согласовано					
Взам. инв. №					
Подпись. Дата					
Инв. № подл.					

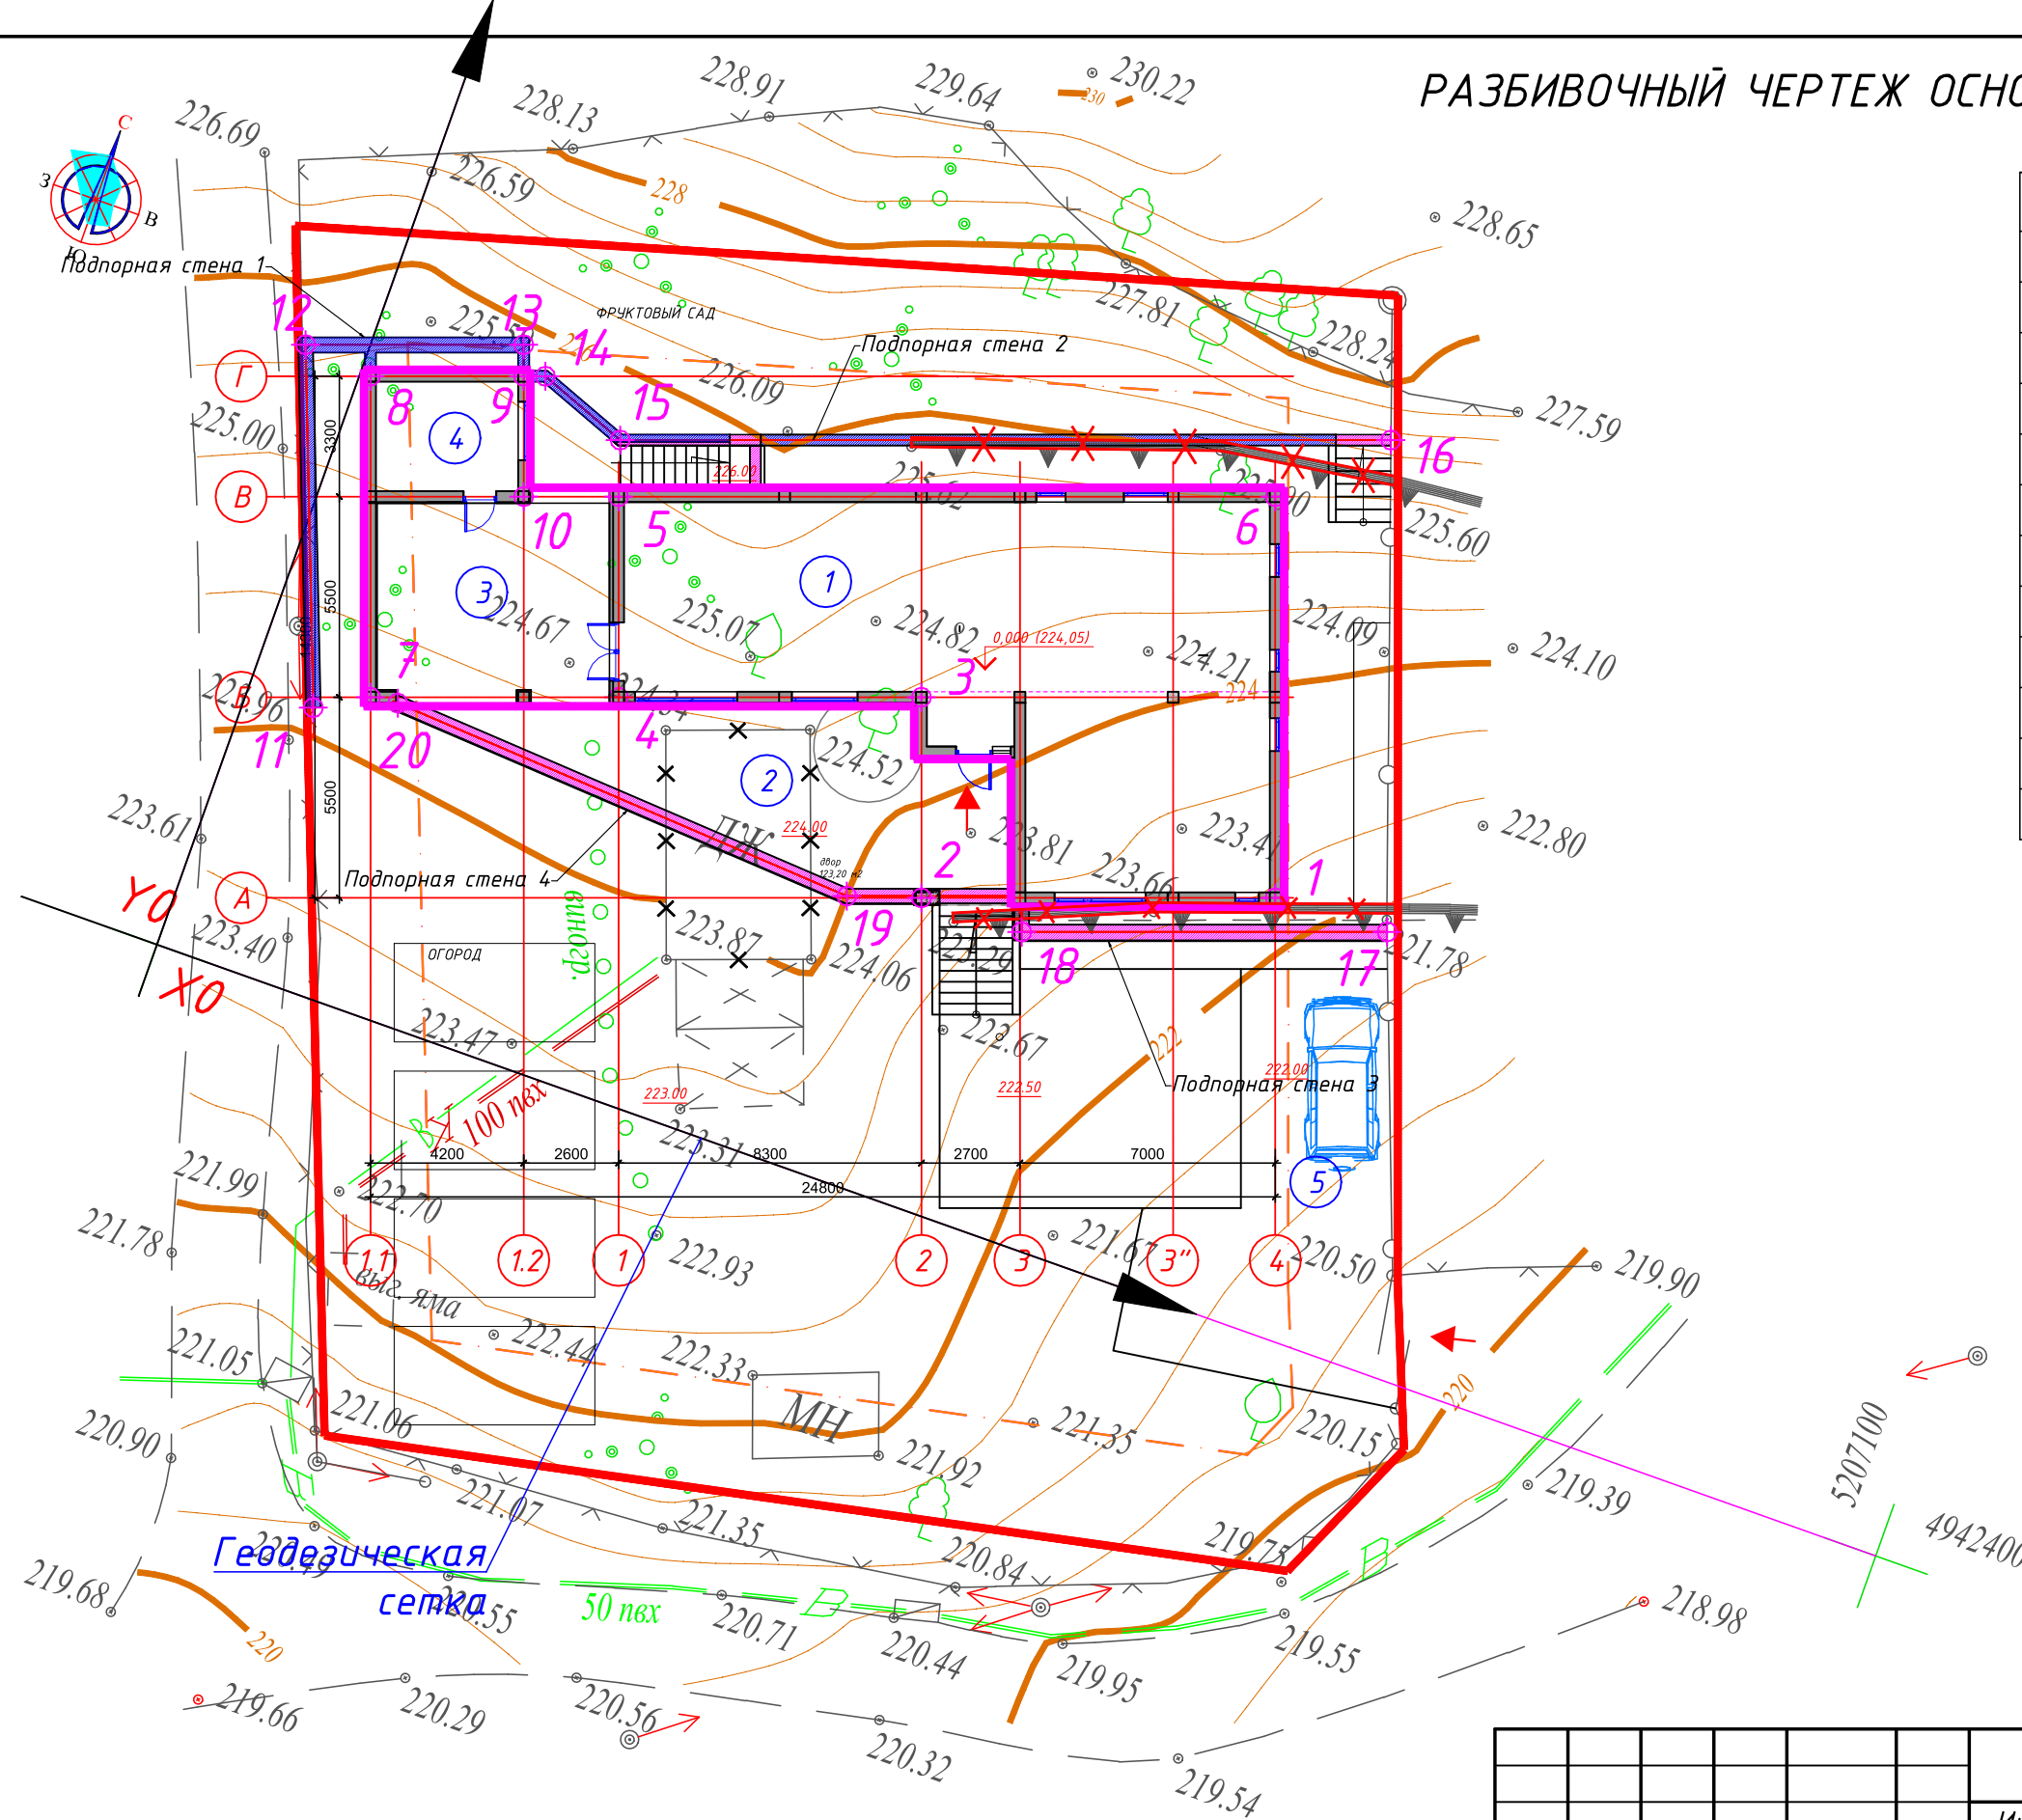РАЗБИВОЧНЫЙ ЧЕРТЕЖ ОСНОВНЫХ ОСЕЙ ЗДАНИЙ И СООРУЖЕНИЙ



№ п/п	Х	У	№ п/п	Х	У
жилой дом			подпорные стены		
1	28,448	11,481	11	1,859	7,558
2	19,309	8,230	12	-1,674	16,859
3	17,466	13,412	13	3,957	18,863
4	9,646	10,630	14	4,807	18,249
5	7,803	15,812	15	7,325	17,287
6	24,761	21,845	16	27,227	24,367
БАРБЕКЮ И МАСТЕРСКАЯ			17	31,643	11,626
7	3,239	8,351	18	22,213	8,271
8	0,290	16,642	19	17,366	7,592
9	4,247	18,049	20	4,000	8,450
10	5,353	14,940			

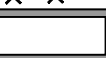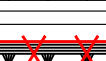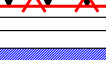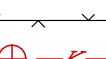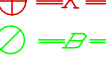УСЛОВНЫЕ ОБОЗНАЧЕНИЯ

-  • Разбираемые здания и сооружения
 -  • Проектируемые здания и сооружения
 -  • Существующие подпорные стены
 -  • Разбираемые подпорные стены
 -  • Проектируемые подпорные стены Тип 1
 -  • Проектируемые подпорные стены Тип 2
 -  • Проектируемые лестницы
 -  • Ограждение
 -  • Канализация
 -  • Водопровод
 -  • Электрический кабель 04 кВ
 -  • Точки разбивки осей зданий и сооружений
 -  • Условная граница проектируемого здания, сооружения
 - • Граница землепользования

ЭКСПЛИКАЦИЯ

№ ПО Г. ПЛ.	НАИМЕНОВАНИЕ	№ ТИП. ПРОЕКТ	ПЛОЩ. ЗАСТР. М КВ.	СТР. ОБЪЕМ, М КУБ.	ПРИМЕЧАНИЯ
1	Проектируемый жилой дом	Индив.	156,09	-	
2	Терраса		54,57	-	
3	Зона барбекю		37,48	-	
4	Мастерская		16,68	-	
5	Парковка		61,15	-	

Примечание:

1. Разбивку основных осей зданий производить относительно геодезической сетки

						02 - 2019 - ГП			
						Индивидуальный жилой дом, по адресу: Республика Крым, Муниципальное образование городской округ Алушта, п. Розовый			
Изм.	Кол.	Лист	№ док.	Подпись	Дата		Стадия	Лист	Листов
							Р	6	
ГИП		Голенкова				Разбивочный чертеж основных осей зданий и сооружений	 самлайн проект инженерное обеспечение зданий	Индивидуальный Предприниматель Голенкова А.В. ОГРНИП 314910223200051	
Разработ.		Гемдицкий							
Н. контр.		Коломиец							

РАЗБИВОЧНЫЙ ЧЕРТЕЖ 2
(Для разбивки вручную)

ЭКСПЛИКАЦИЯ

№ по г. пл.	НАИМЕНОВАНИЕ	№ ТИП. ПРОЕКТ.	ПЛОЩ. ЗАСТР. М. КВ.	СТР. ОБЪЕМ, М. КУБ.	ПРИМЕЧАНИЯ
1	Проектируемый жилой дом	Индив.	156,09	-	
2	Терраса		54,57	-	
3	Зона барбекю		37,48	-	
4	Мастерская		16,68	-	
5	Парковка		61,15	-	

УСЛОВНЫЕ ОБОЗНАЧЕНИЯ

- × × × ×

КН

• Разбираемые здания и сооружения
- Проектируемые здания и сооружения
- Существующие подпорные стены
- × × × ×

× × × ×

• Разбираемые подпорные стены
- Проектируемые подпорные стены Тип 1
- Проектируемые подпорные стены Тип 2
- Проектируемые лестницы
- × — ×

— × — ×

• Ограждение
- ⊕ — ⊕

— ⊕ — ⊕

• Канализация
- ⊙ — ⊙

— ⊙ — ⊙

• Водопровод
- × ← ×

→ × ← ×

• Электрический кабель 04 кВ
- ⊕ 3

⊕ 3




• Точки разбивки осей зданий и сооружений
- Условная граница проектируемого здания, сооружения
- Граница землепользования

Согласовано					
Взам. инв. №					
Подпись. Дата					
Инв. № подл.					










						02 - 2019 - ГП		
						Индивидуальный жилой дом, по адресу: Республика Крым, Муниципальное образование городской округ Алушта, п. Розовый		
Изм.	Кол.	Лист	№ док.	Подпись	Дата	Стадия	Лист	Листов
						Р	7	
ГИП		Голенкова				Разбивочный чертеж 2 (для разбивки вручную)		
Разработ.		Гемдицкий						
Н. контр.		Коломиец						
						самлайн проект инженерное обеспечение зданий Индивидуальный Предприниматель Голенкова А.В. ОГРНИП 314910223200051		

ПЛАН ПОКРЫТИЙ

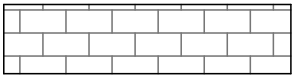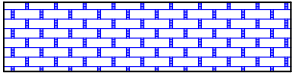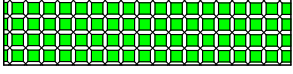Типы покрытий и площади

- 
 - Тип. 1. Покрытие из бетонной плитки 157,84 м.кв.
- 
 - Тип. 2. Покрытие из плитки 14,58 м.кв.
- 
 - Тип. 3. Покрытие из бетонной плитки 63,10 м.кв.
- 
 - Тип 4. Экологическое покрытие 51,36 м.кв.
- 
 - Грунтовое покрытие 524,18 м.кв.

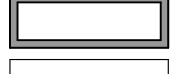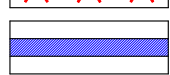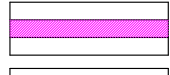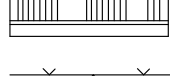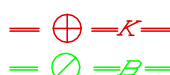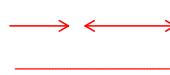 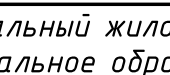 Условные обозначения

- 
 - Разбираемые здания и сооружения
- 
 - Проектируемые здания и сооружения
- 
 - Существующие подпорные стены
- 
 - Разбираемые подпорные стены
- 
 - Проектируемые подпорные стены Тип 1
- 
 - Проектируемые подпорные стены Тип 2
- 
 - Проектируемые лестницы
- 
 - Ограждение
- 
 - Канализация
- 
 - Водопровод
- 
 - Электрический кабель 04 кВ
- 
 - Граница землепользования


ЭКСПЛИКАЦИЯ

№ по Г. Пл.	НАИМЕНОВАНИЕ	№ ТИП. ПРОЕКТ.	ПЛОЩ. ЗАСТР. М КВ.	СТР. ОБЪЕМ, М КУБ.	ПРИМЕЧАНИЯ
1	Проектируемый жилой дом	Индив.	156,09	-	
2	Терраса		54,57	-	
3	Зона барбекю		37,48	-	
4	Мастерская		16,68	-	
5	Парковка		61,15	-	

						02 - 2019 - ГП		
						Индивидуальный жилой дом, по адресу: Республика Крым, Муниципальное образование городской округ Алушта, п. Розовый		
						Стадия	Лист	Листов
						Р	8	
						План покрытий		
						 самлайн проект Индивидуальный Предприниматель Голенкова А.В. ОГРНИП 314910223200051		


ТИПЫ ПОКРЫТИЙ СЕЧЕНИЯ

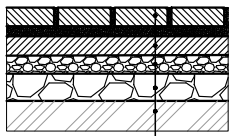Тип 1





Бетонная плитка 300x165x50мм	-50мм
Цементно-песчаная смесь	-50мм
Монолитная ж/б подушка - бетон В15. сетка 50x50x4мм. ВРІ.	-100мм
Мелкощебеночное основание фракции 5-10мм	-100мм
Крупнощебеночная обратная засыпка фракции 20-40 мм	- 100мм
Уплотненный грунт основания	

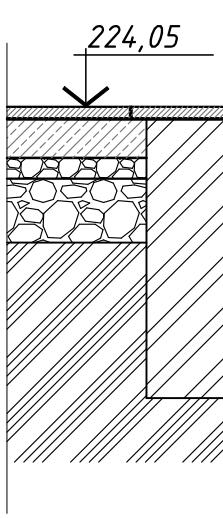Тип 2




Тип 4

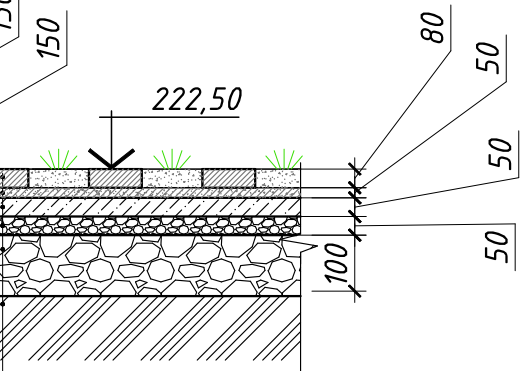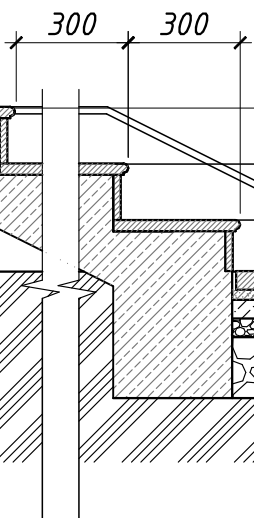


Газонная решётка Мёба Серый (толщина 100 мм)
Плодородный слой с семенами газона
Выравнивающий слой - смесь песка с цементом 20-30мм
Песчано-гравийная подушка 200-300мм
Уплотненный грунт основания

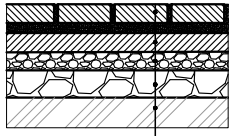Тип 3



Бетонная плитка 300x165x80мм	-80мм
Цементно-песчаная смесь	-50мм
Монолитная ж/б подушка - бетон В15. сетка 50x50x4мм. ВРІ.	-100мм
Мелкощебеночное основание фракции 5-10мм	-100мм
Крупнощебеночная обратная засыпка фракции 20-40 мм	- 100мм
Уплотненный грунт основания	

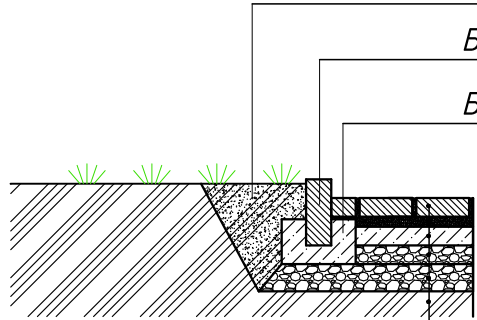A-A



Уплотненный грунт основания	
Бортовой гранитный камень 150х300мм	
Бетон В15 (М200)	
	
Бетонная плитка 300х165х80мм	-80мм
Цементно-песчаная смесь	-50мм
Монолитная ж/б подушка - бетон В15, сетка 50х50х4мм, ВРІ.	-100мм
Мелкощебеночное основание фракции 5-10мм	-100мм
Крупнощебеночная обратная засыпка фракции 20-40 мм	- 100мм
Уплотненный грунт основания	

Согласовано			
Взам. инв. №			
Подпись. Дата			
Инв. № подл.			


Примечание:
Данный лист см. совместно с листом №5 компл. 02 - 2019 - ГП

						02 - 2019 - ГП		
						Индивидуальный жилой дом, по адресу: Республика Крым, Муниципальное образование городской округ Алушта, п. Розовый		
Изм.	Кол.	Лист	№ док.	Подпись	Дата	Стадия	Лист	Листов
						Р	9	
ГИП				Голенкова		Типы покрытий сечения		
Разработ.				Гемдицкий				
Н. контр.				Коломиец				
						 самлайн проект инженерное обеспечение зданий Индивидуальный Предприниматель Голенкова А.В. ОГРНИП 314910223200051		

ПЛАН ЗЕМЛЯНЫХ МАСС
М 1:200

УСЛОВНЫЕ ОБОЗНАЧЕНИЯ

	Проектируемые объекты
	Проектируемые подпорные стены
	Проектируемые лестницы
	Граница участка землепользования
	$\frac{-4.30}{75.70} \quad \frac{80.00}{80.00}$ рабочая отметка проектная отметка земли существующая отметка земли
	± 30 объем насыпи (+), выемки (-), м ³ .
	насыпь
	граница нулевых работ
	выемка

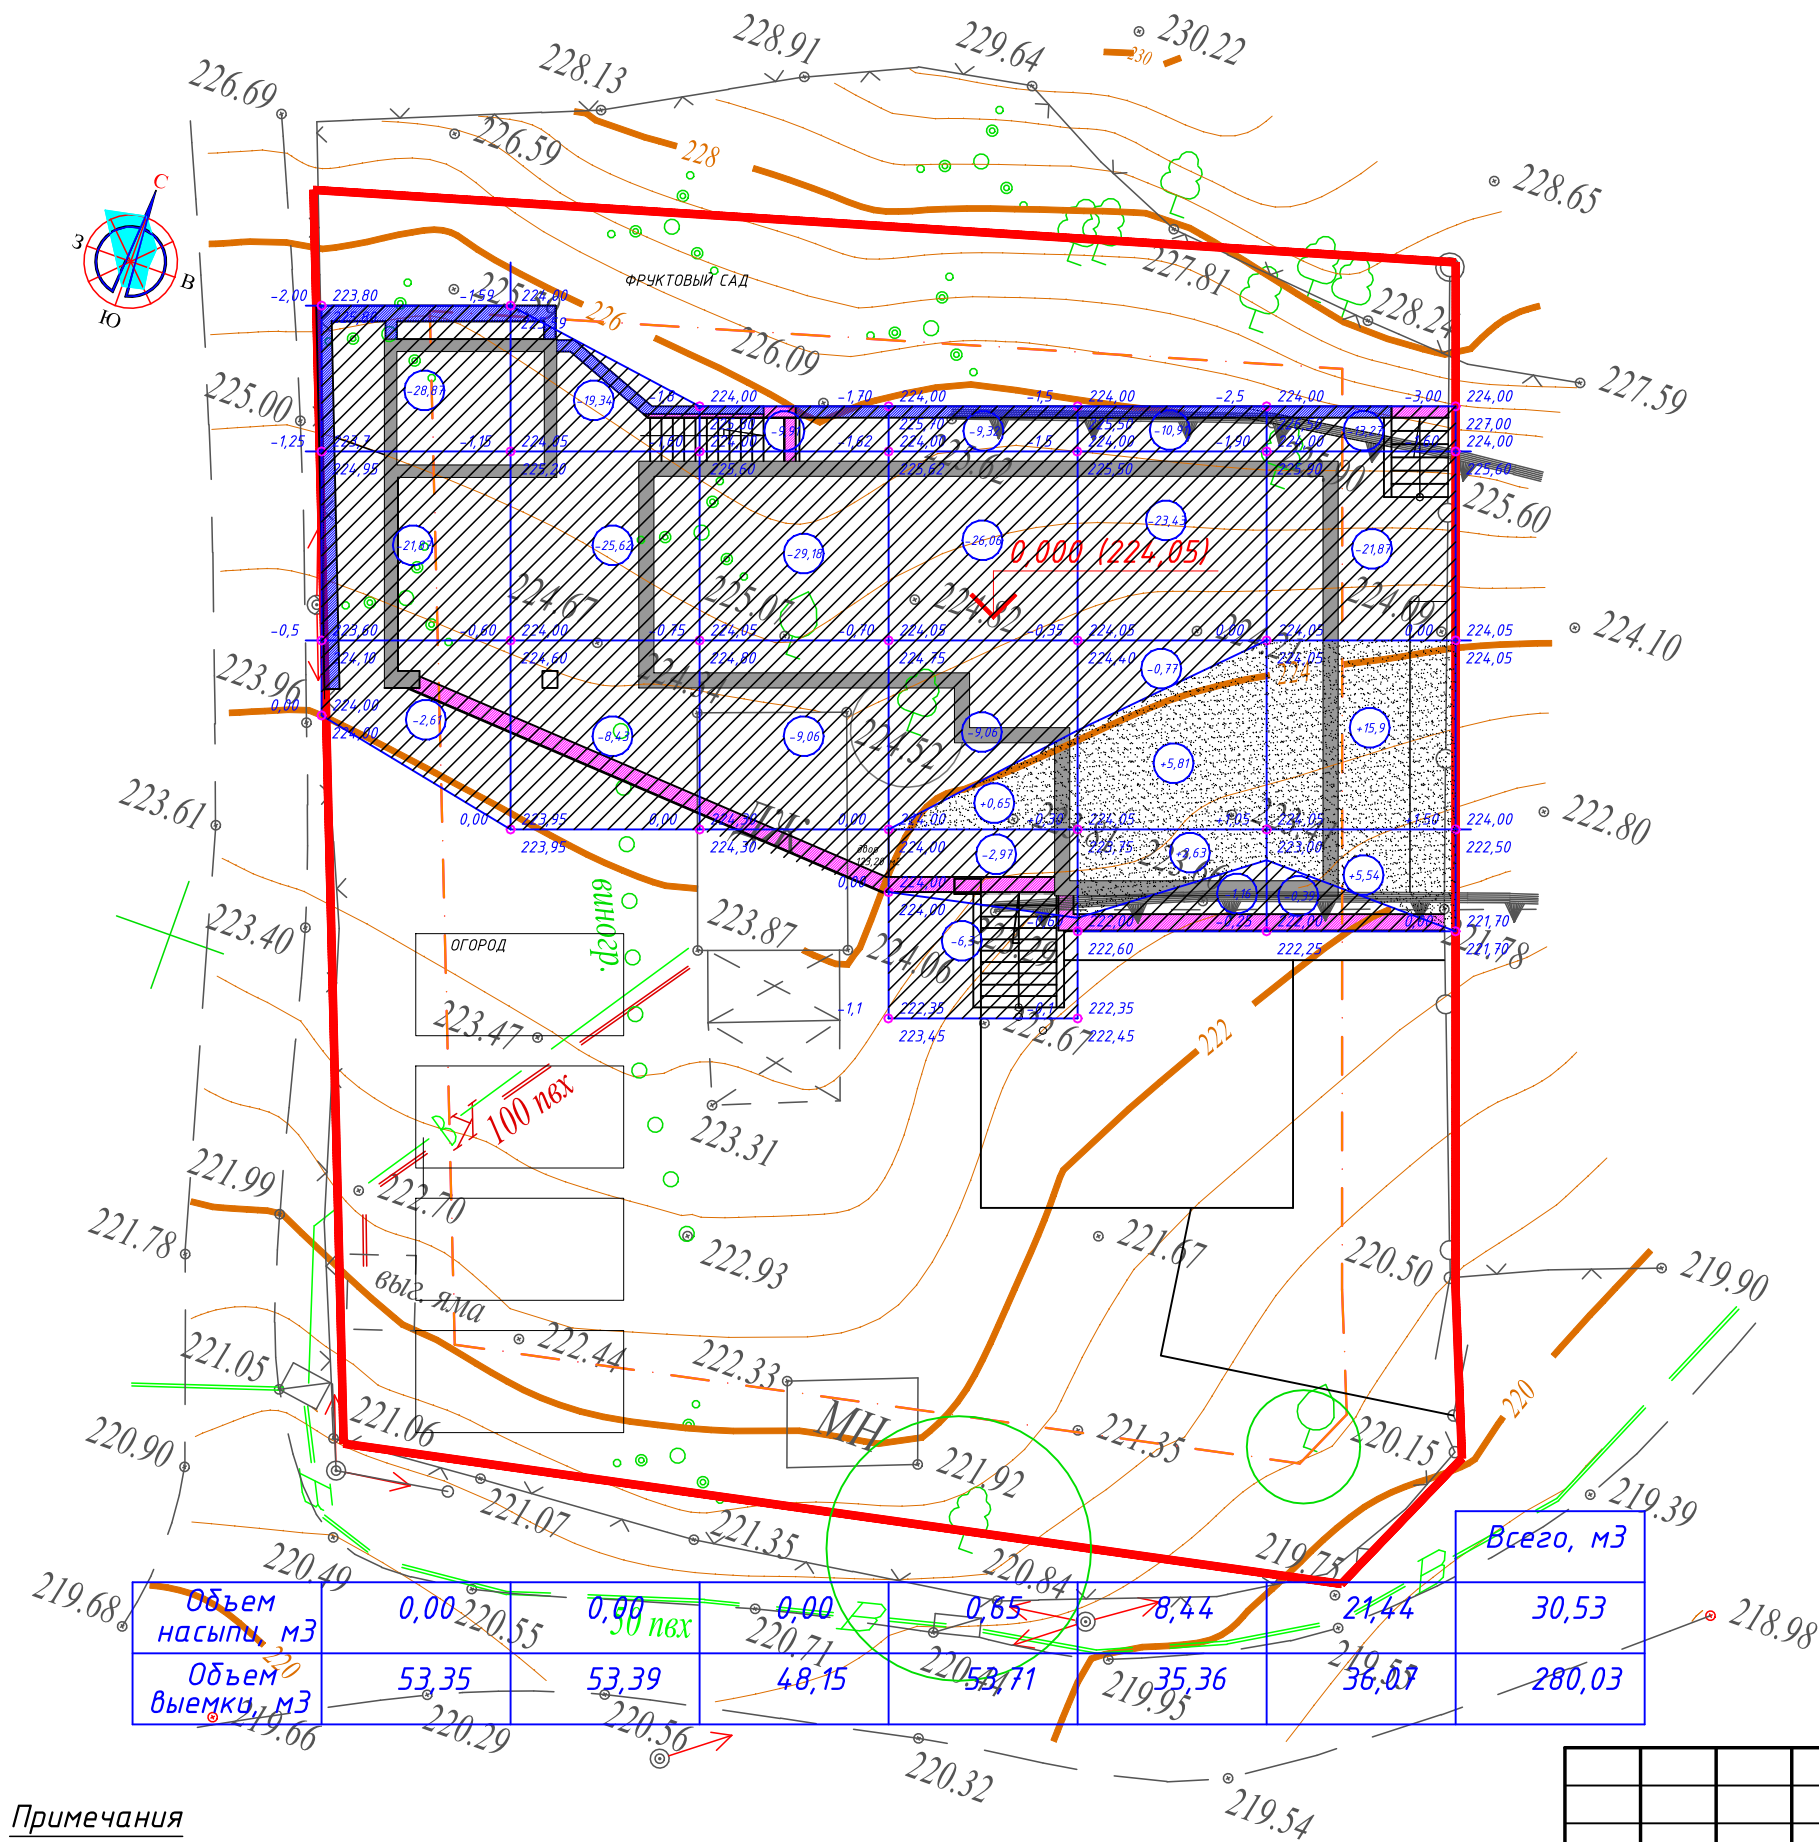


Примечания


- Опорный план разработан на основе топографической съемки, выполненной инженером-геодезистом.
- Площадь участка составляет 1015 м² = 0,1015 га
- За относительную отметку 0,000 принят уровень чистого пола первого этажа, что соответствует абсолютной отметке 224,05м над уровнем моря.
- Расчет объемов передвижения земляных масс дан без учета запаса 10%.

						02 - 2019 - ГП		
						Индивидуальный жилой дом, по адресу: Республика Крым, Муниципальное образование городской округ Алушта, п. Розовый		
Изм.	Кол.	Лист	№ док.	Подпись	Дата	Стадия	Лист	Листов
						Р	10	
ГИП		Голенкова				План земляных масс М 1:200		
Разработ.		Гемдицкий						
Н. контр.		Коломиец						
						 самлайн проект инженерное проектирование зданий		
						Индивидуальный Предприниматель Голенкова А.В. ОГРНИП 314910223200051		

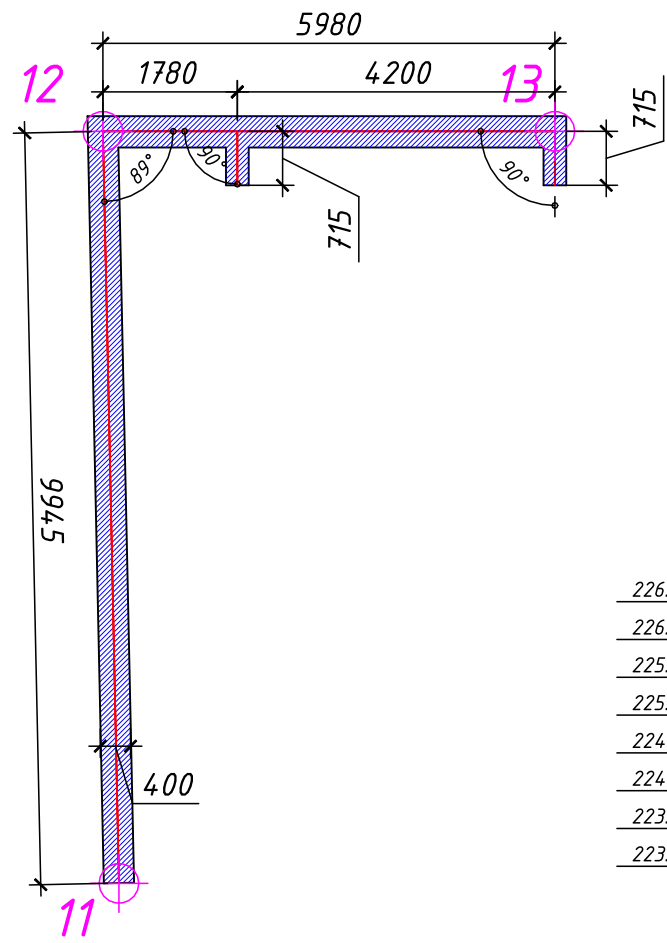Подпорная стена 1




226.50	
226.00	
225.50	
225.00	
224.50	
224.00	
223.50	
223.00	

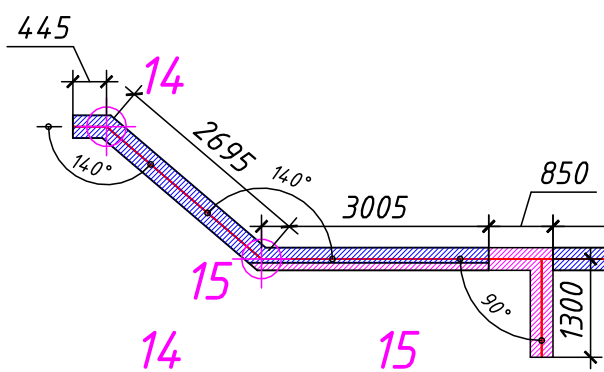


Подпорная стена 2

226.50	
226.00	
225.50	
225.00	
224.50	
224.00	
223.50	
223.00	

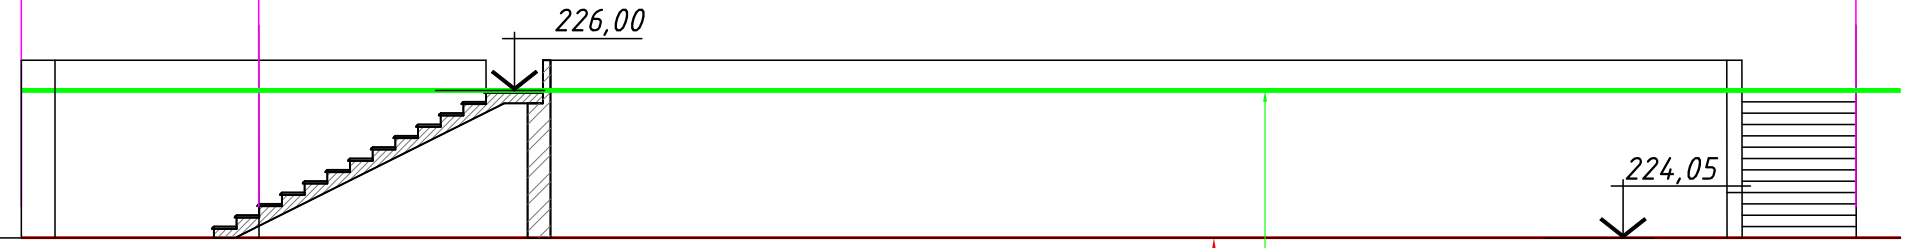


Подпорная стена 3

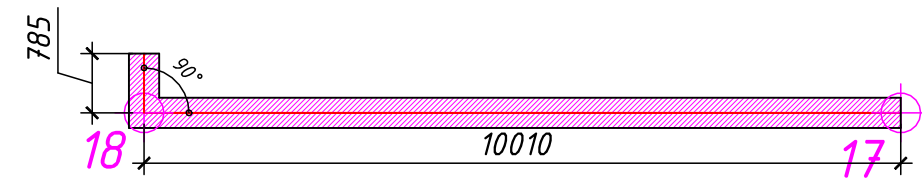

Подпорная стена 4

225.00	
224.50	
224.00	
223.50	
223.00	
222.50	

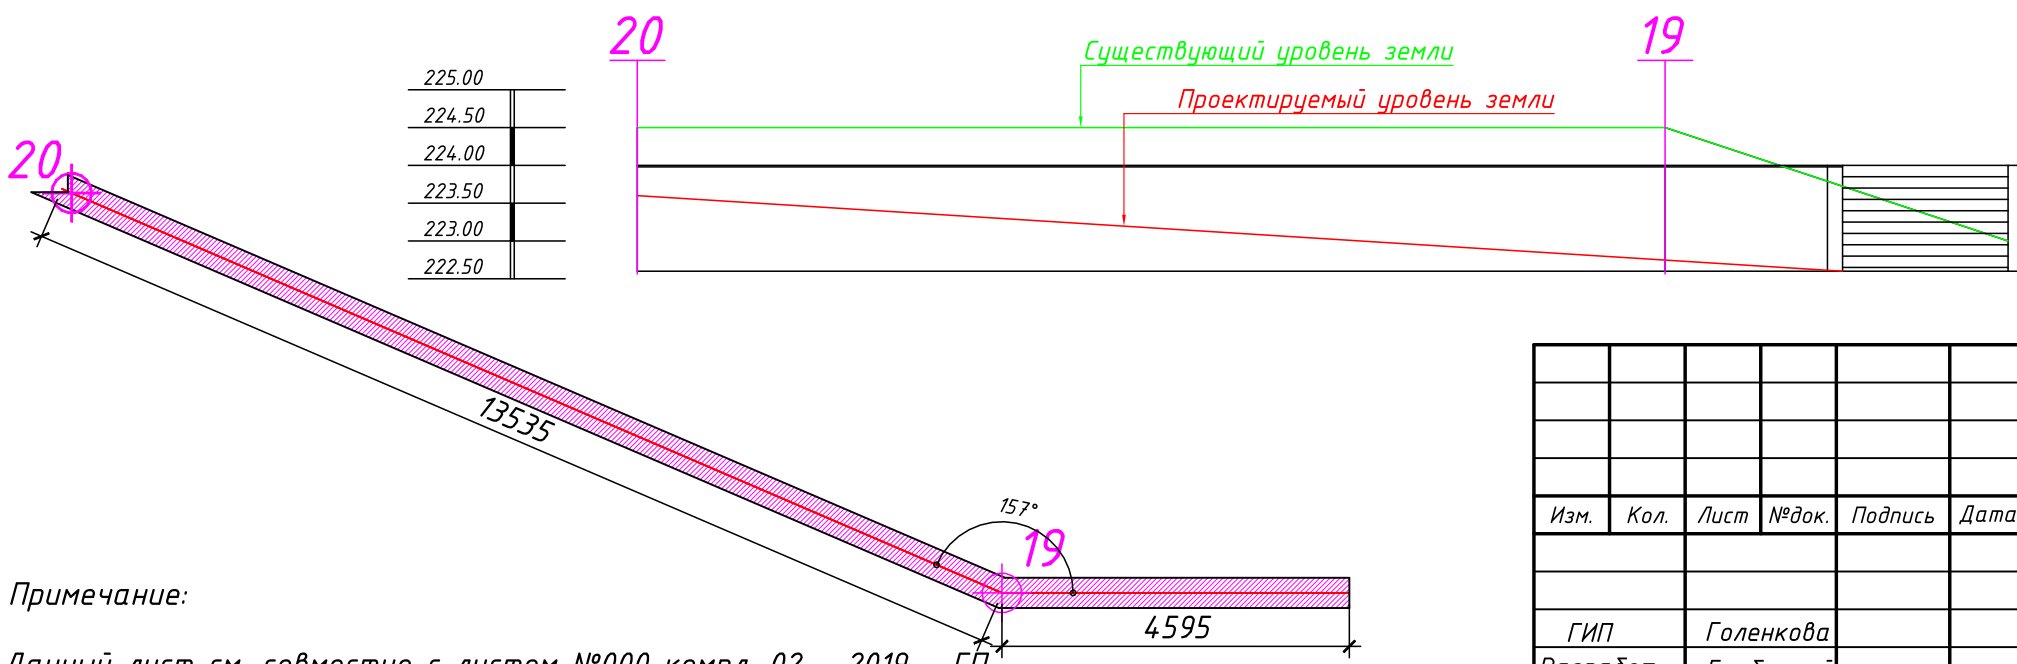

Примечание:

Данный лист см. совместно с листом №000 компл. 02 - 2019 - ГП

РАЗВЕРТКИ
ПОДПОРНЫХ СТЕН
М 1:100


Существующий уровень земли
Проектируемый уровень земли

Существующий уровень земли
Проектируемый уровень земли


Существующий уровень земли
Проектируемый уровень земли

						02 - 2019 - ГП		
						Индивидуальный жилой дом, по адресу: Республика Крым, Муниципальное образование городской округ Алушта, п. Розовый		
						Стадия	Лист	Листов
						Р	11	
						Развертки подпорных стен. М 1:100		
						самлайн проект Индивидуальный Предприниматель Голенкова А.В. ОГРНИП 314910223200051		


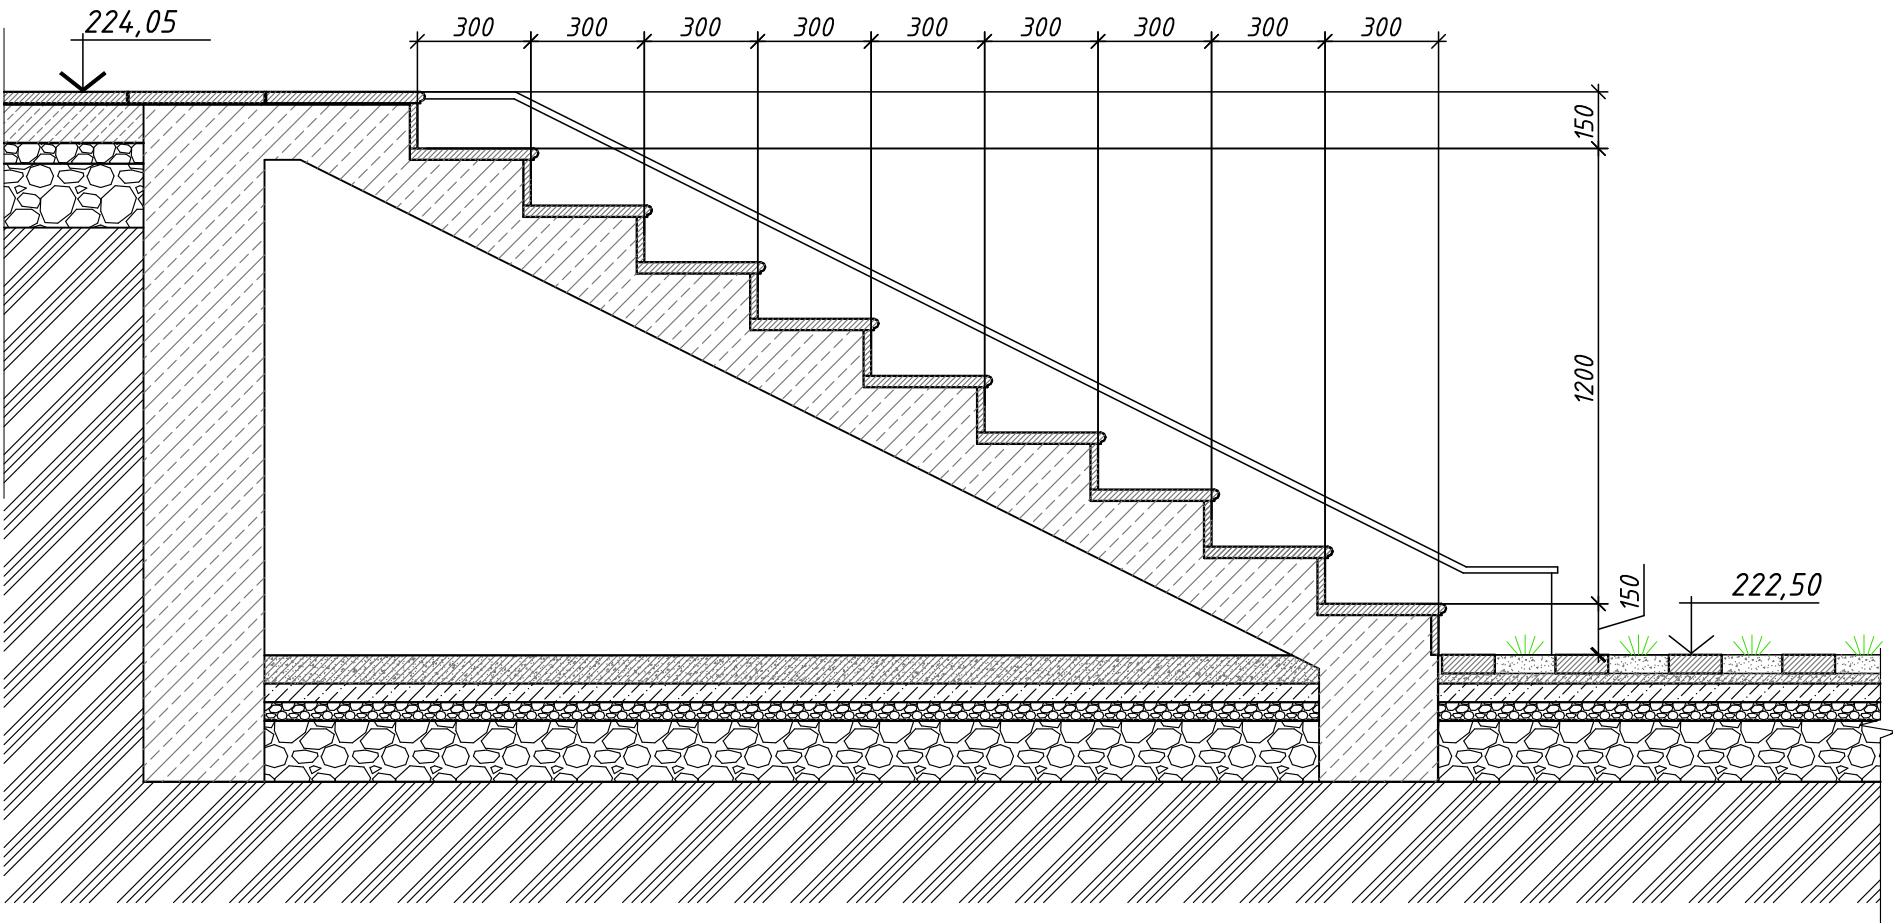
Лестница 1



НАРУЖНЫЕ ЛЕСТНИЦЫ
М 1:100

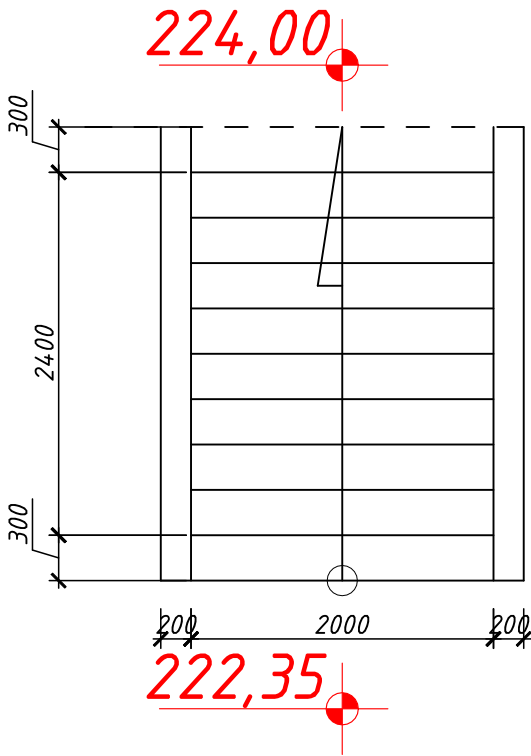

Лестница 2

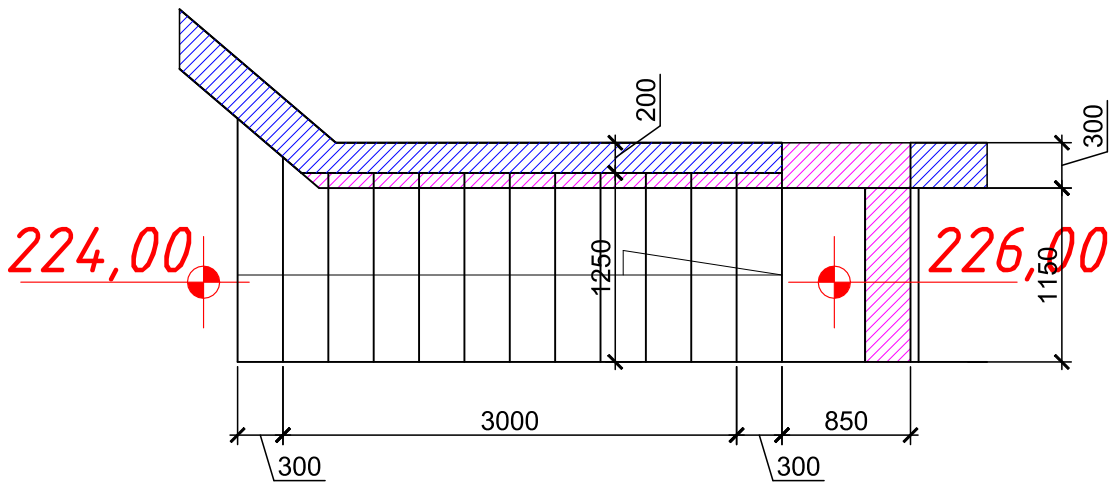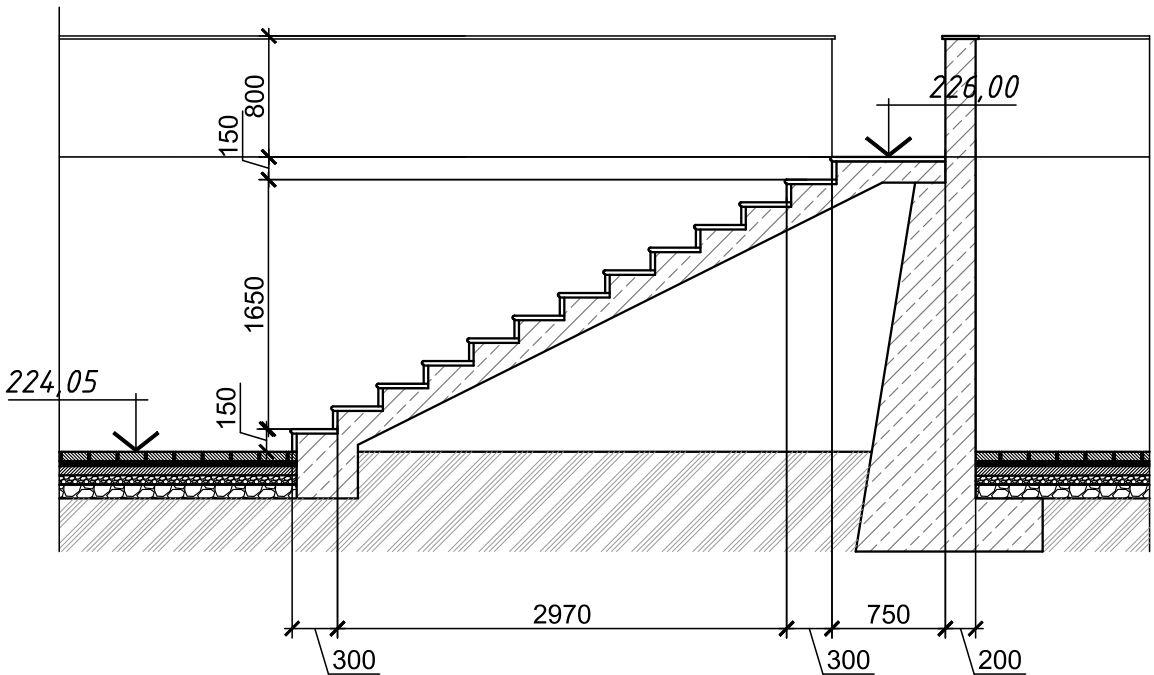

Согласовано					
Взам. инв. №					
Подпись. Дата					
Инв. № подл.					

						02 - 2019 - ГП		
						Индивидуальный жилой дом, по адресу: Республика Крым, Муниципальное образование городской округ Алушта, п. Розовый		
Изм.	Кол.	Лист	№ док.	Подпись	Дата	Стадия	Лист	Листов
						Р	12	
ГИП		Голенкова				Наружные лестницы М 1:100		
Разработ.		Гембицкий						
Н. контр.		Коломиец						
						 Индивидуальный Предприниматель Голенкова А.В. ОГРНИП 314910223200051		