

Ведомость рабочих чертежей основного комплекта		
Лист	Наименование	Примечание
1	Общие данные	
2	Гостиная. Вид 1, 2.	
3	Гостиная. Вид 3.	
4	Коридор. Вид 1, 2.	
5	Коридор. Вид 3	
6	Спальня. Вид 1, 2, 3.	
7	Спальня. Вид 1	
8	Санузел. Вид 1, 2.	
9	Санузел. Вид 3, 4.	
10	Обмерный план	
11	Разрез 1-1	
12	План монтируемых перегородок	
13	Разрез по лестнице	
14	План мебели и оборудования	
15	План заполнения дверных проемов	
16	План привязки сантехники	
17	План напольных покрытий	
18	План потолков	
19	План осветительного оборудования	
20	План осветительного оборудования с мебелью	
21	Привязка светильников и выключателей	
22	Привязка выключателей с мебелью	
23	План привязки розеток и выключателей	
24	Схема размещения розеток, выключателей и мебели	
25	План отделки стен	
26	Схема развертки стен	
27	Развертка Санузла	
28	Развертка Гостиной-Кухни	
29	Развертка Гостиной-Кухни	
30	Развертка Гостиной-Кухни	
31	Развертка Спальни	
32	Ведомость рекомендуемых отделочных материалов	

Дизайнер		г. Москва, Нижняя Красносельская, 26.7 кв.м.	Стадия	Лист	
Клиент		Общие данные	РП	1	




Дизайнер		г. Москва, Нижняя Красносельская, 26.7 кв.м.	Стадия	Лист	
Клиент		Гостиная. Вид 1, 2.	РП	2	




Дизайнер		г. Москва, Нижняя Красносельская, 26.7 кв.м.	Стадия	Лист	
Клиент		Гостиная. Вид 3.	РП	3	

Компьютерное моделирование. Коридор. Вид 1, 2.

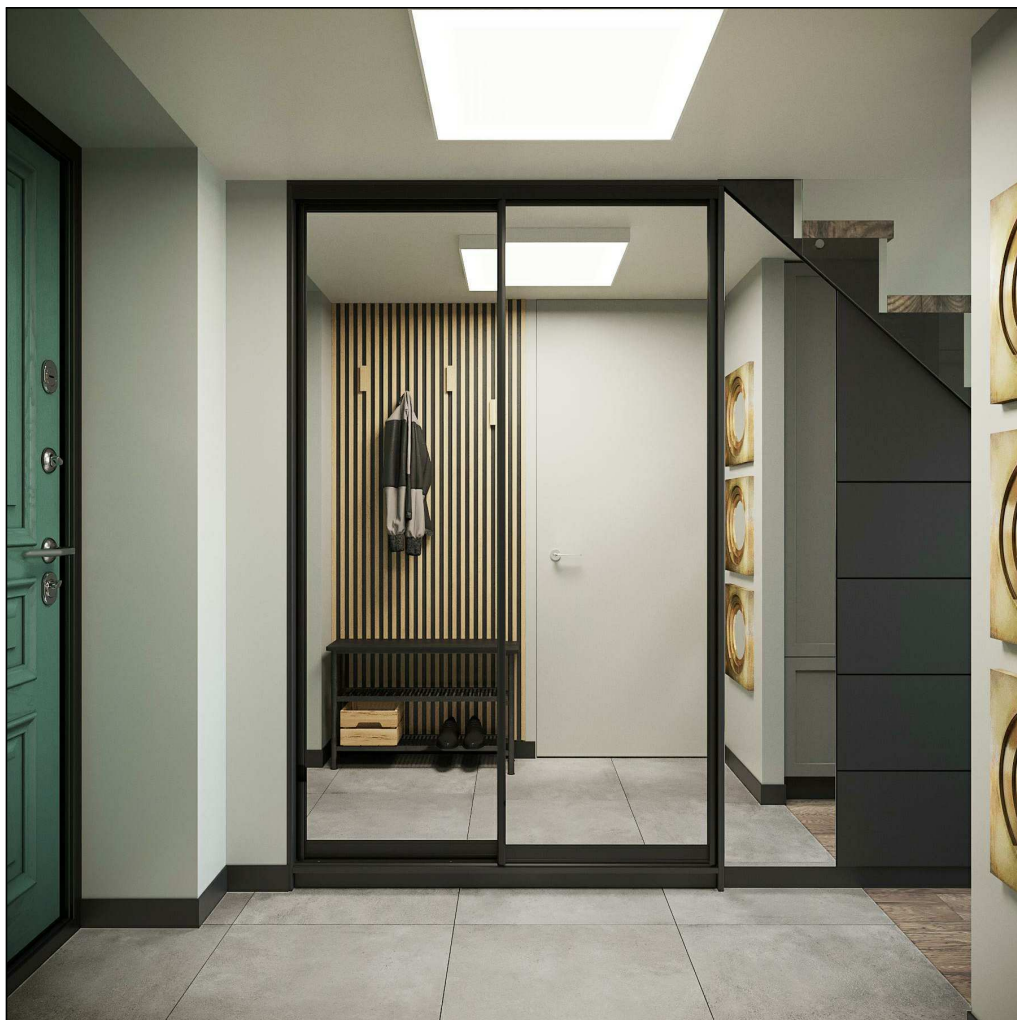



Дизайнер		г. Москва, Нижняя Красносельская, 26.7 кв.м.	Стадия	Лист	
Клиент		Коридор. Вид 1, 2.	РП	4	

Компьютерное моделирование. Коридор. Вид 3.

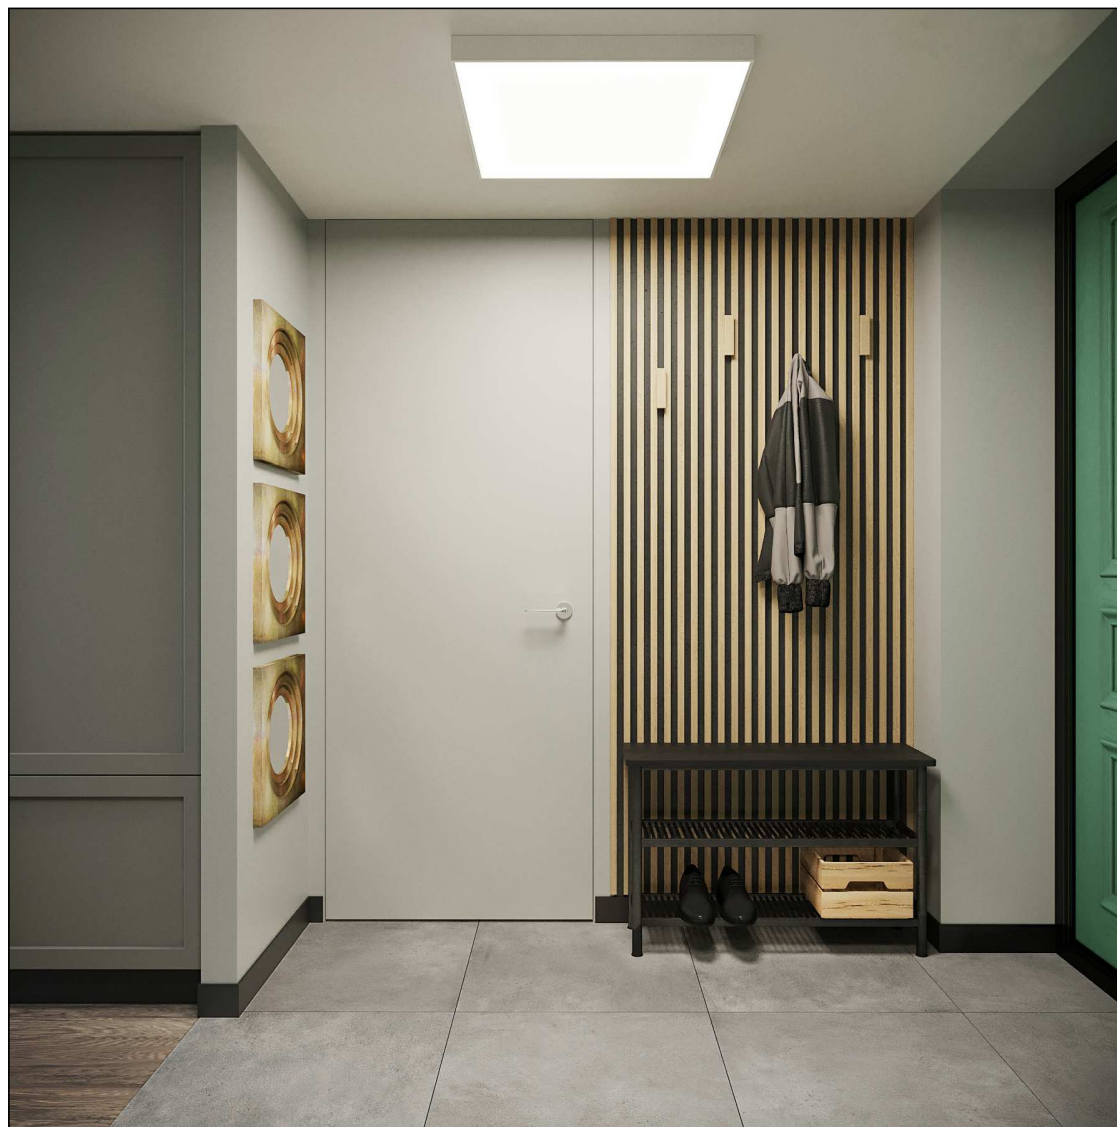


Дизайнер		г. Москва, Нижняя Красносельская, 26.7 кв.м.	Стадия	Лист	
Клиент		Коридор. Вид 3	РП	5	

Компьютерное моделирование. Спальня. Вид 1, 2, 3.

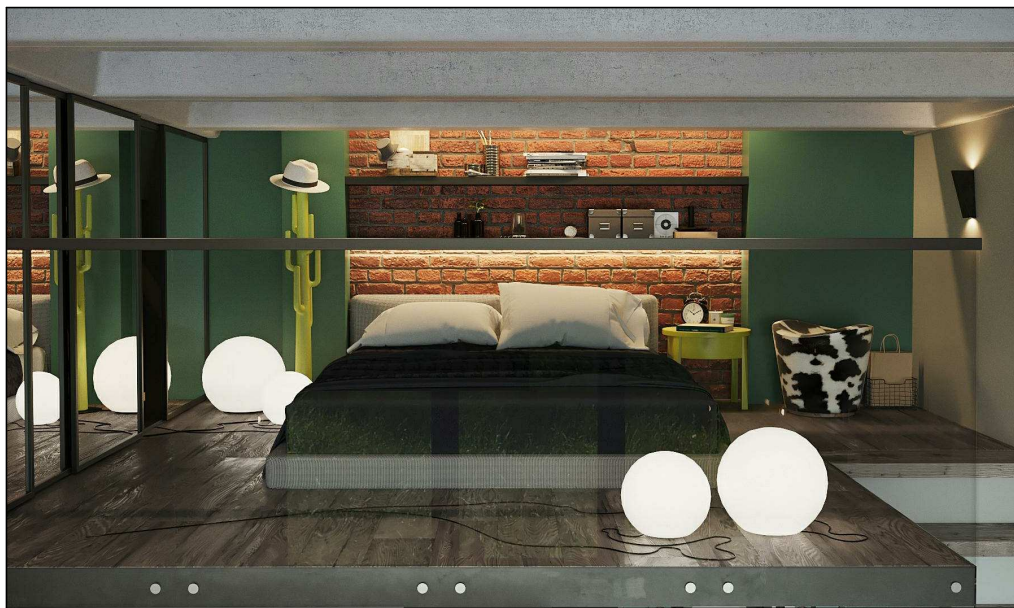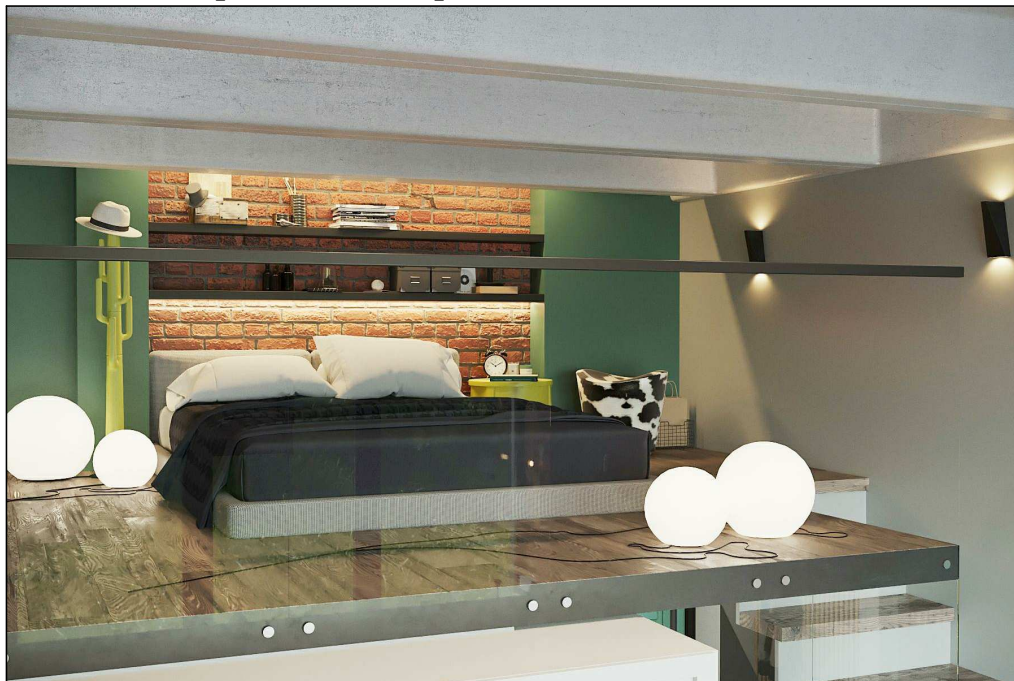

Дизайнер		г. Москва, Нижняя Красносельская, 26.7 кв.м.	Стадия	Лист	
Клиент		Спальня. Вид 1, 2, 3.	РП	6	

Компьютерное моделирование. Спальня. Вид 1.

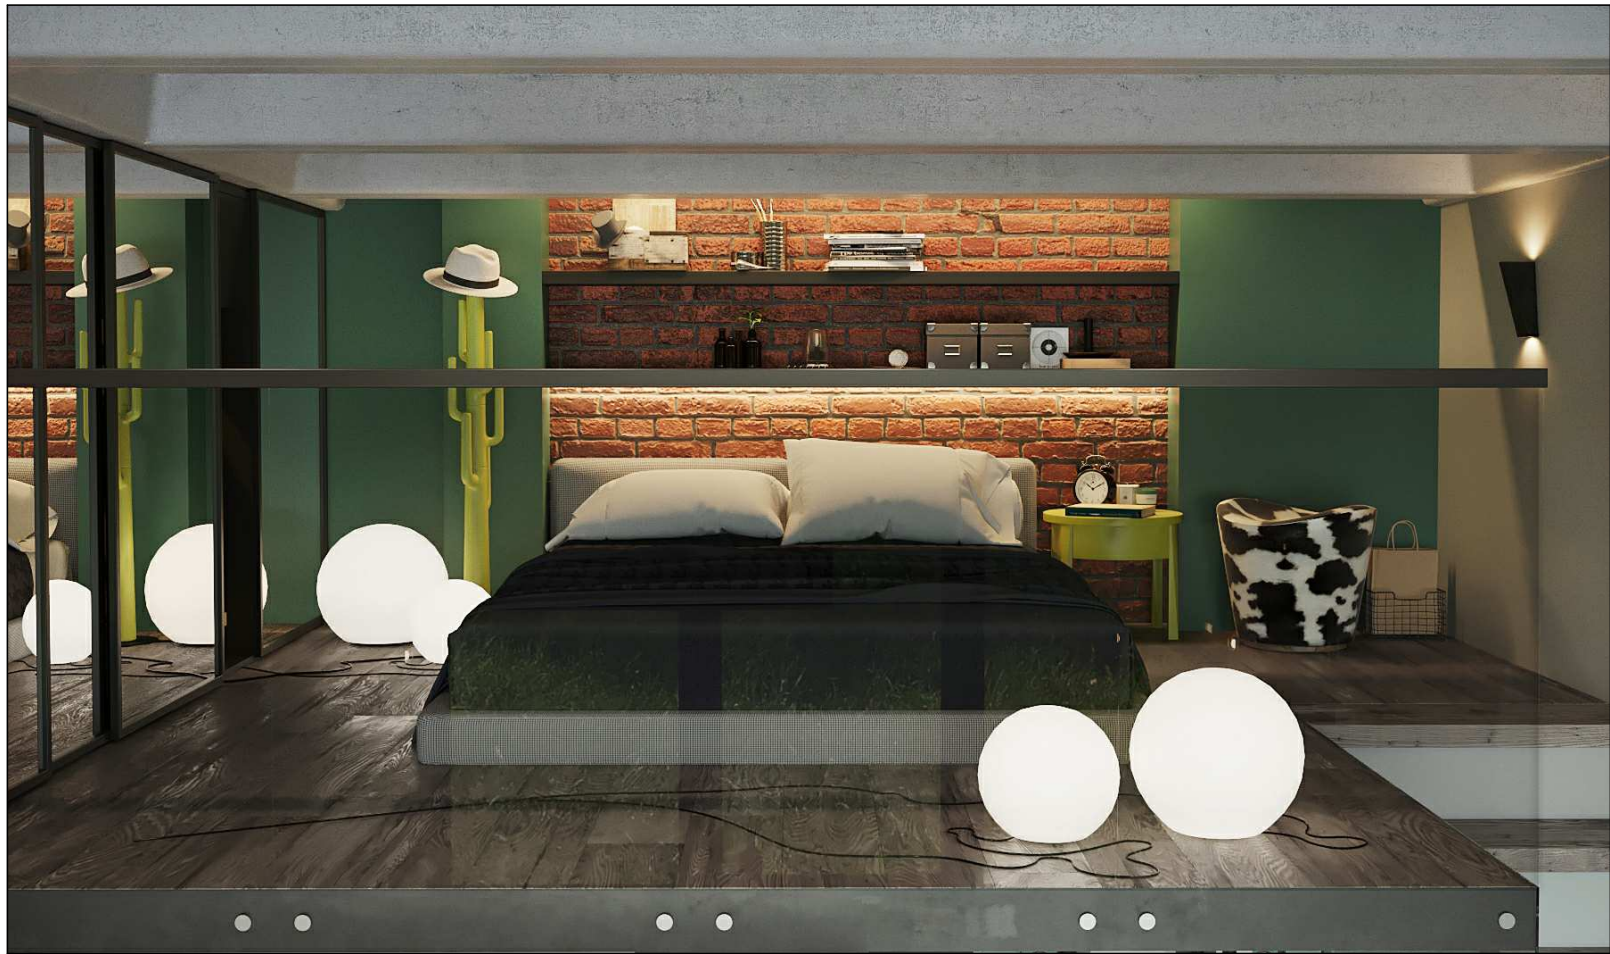

Дизайнер		г. Москва, Нижняя Красносельская, 26.7 кв.м.	Стадия	Лист	
Клиент		Спальня. Вид 1	РП	7	

Компьютерное моделирование. Санузел. Вид 1, 2.




Дизайнер		г. Москва, Нижняя Красносельская, 26.7 кв.м.	Стадия	Лист	
Клиент		Санузел. Вид 1, 2.	РП	8	

Компьютерное моделирование. Санузел. Вид 3, 4.




Дизайнер		г. Москва, Нижняя Красносельская, 26.7 кв.м.	Стадия	Лист	
Клиент		Санузел. Вид 3, 4.	РП	9	

Обмерный план. Москва, Нижняя
Красносельская, 26.7 кв.м.
1: 35

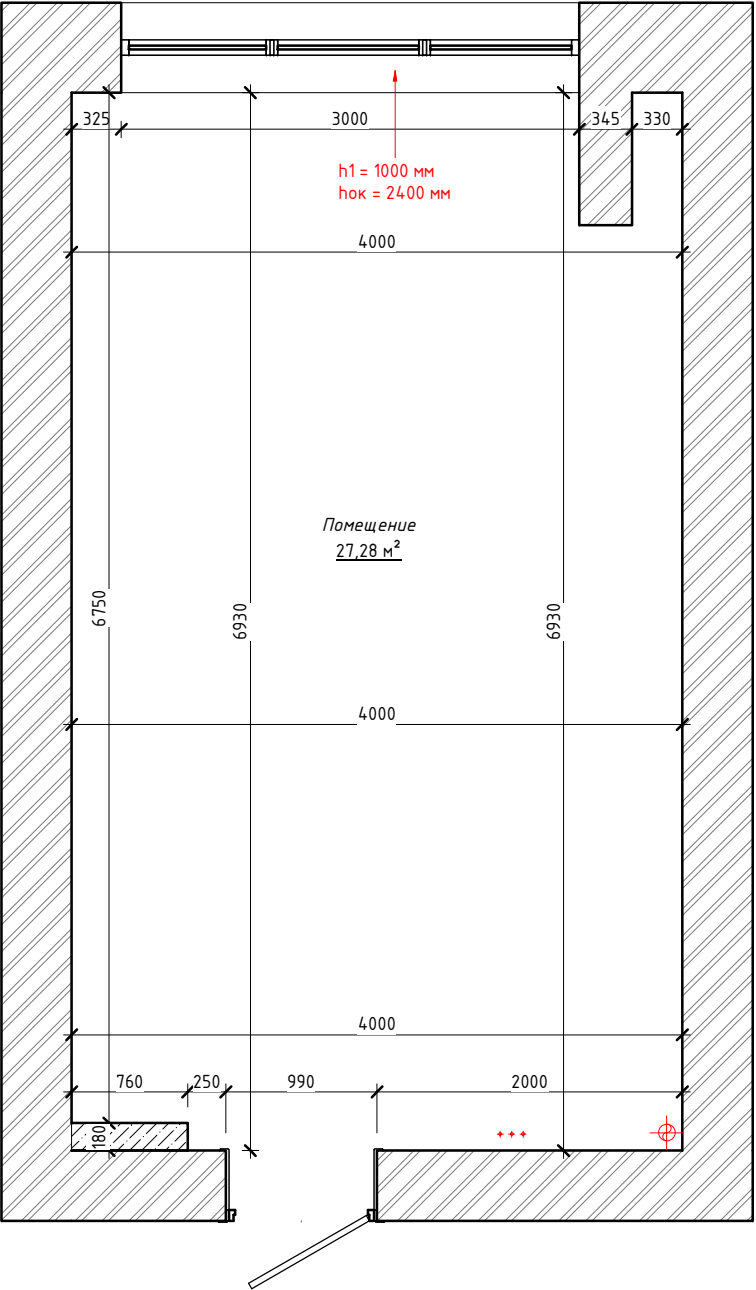

Обмерный план потолка
1: 35

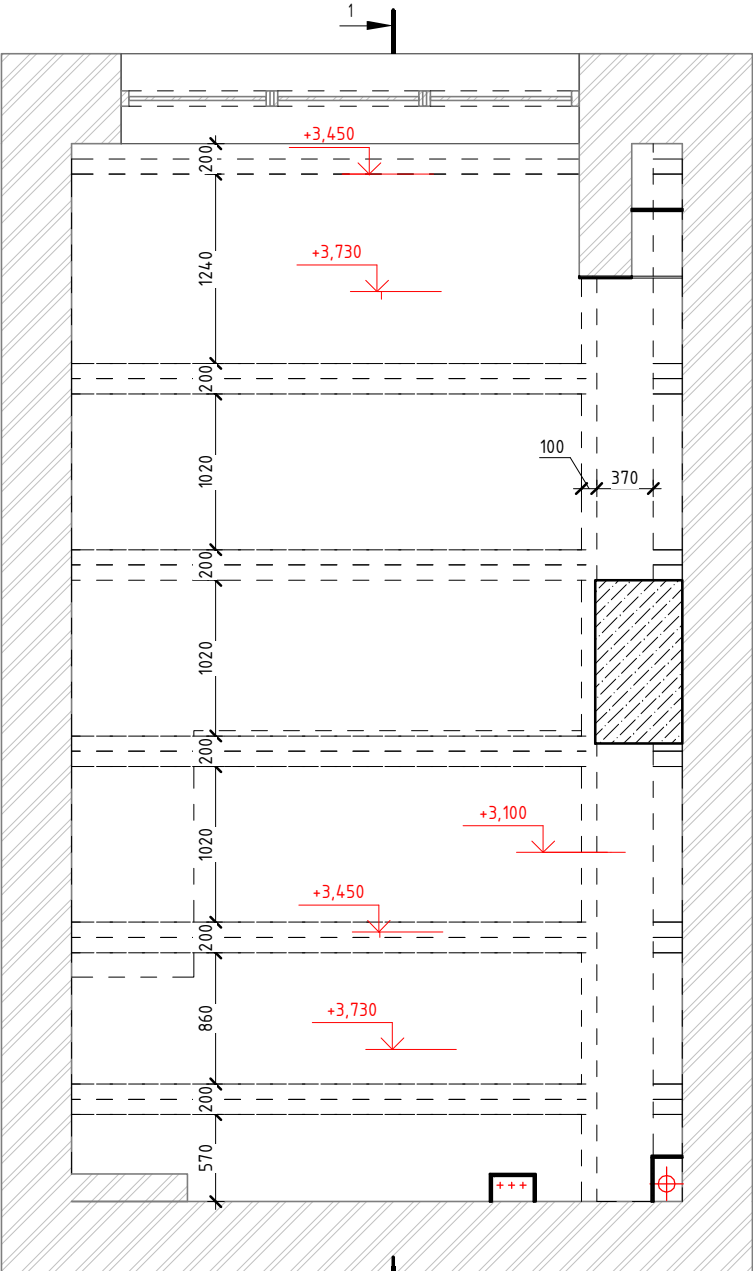


- Существующие стены, перегородки
- Стояк канализации / водопровода
- Радиатор отопления стальной, белый. Подключение вертикальное
- Шахта обменной вентиляции
- Отметка высоты по обмерам

Все привязки размеров даны по НЕштукатуренным стенам, необходимо учитывать погрешность

Дизайнер	г. Москва, Нижняя Красносельская, 26.7 кв.м.	Стадия	Лист
Клиент	Обмерный план	РП	10


Разрез 1-1
1: 25

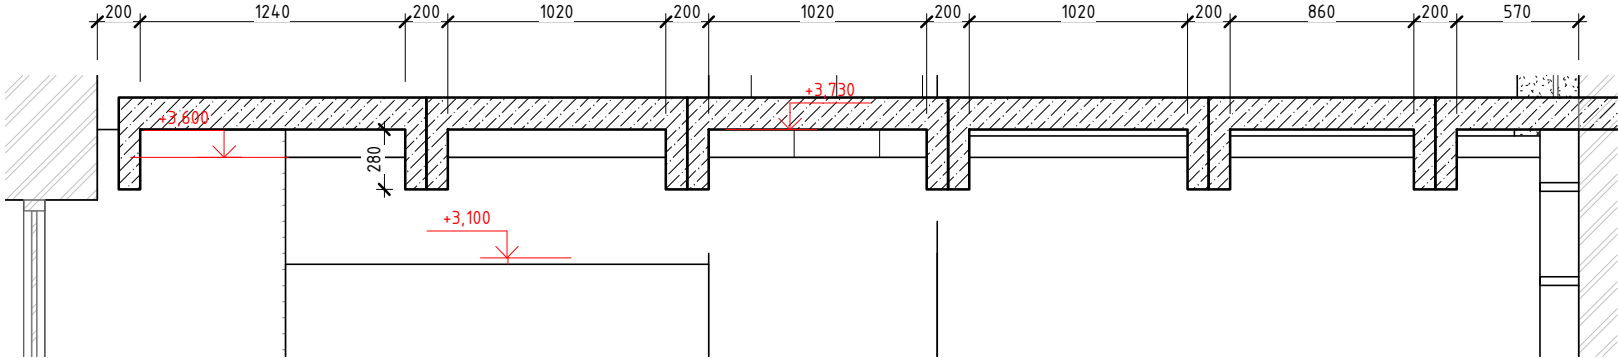

Дизайнер		г. Москва, Нижняя Красносельская, 26.7 кв.м.	Стадия	Лист	
Клиент		Разрез 1-1	РП	11	



План монтируемых перегородок. 1

этаж
1: 35

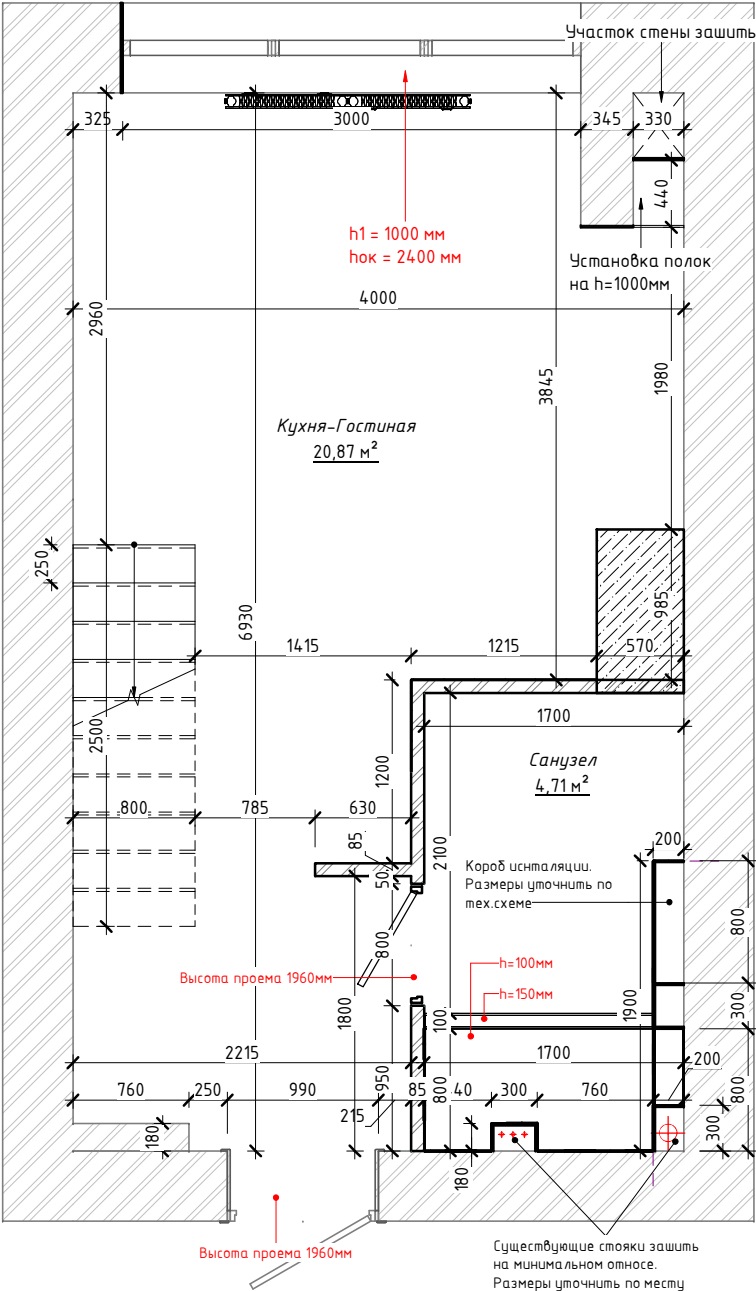

План монтируемых перегородок. 2

этаж
1: 35

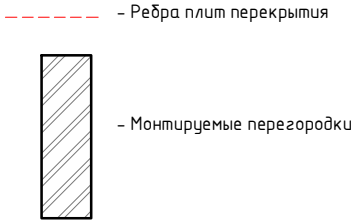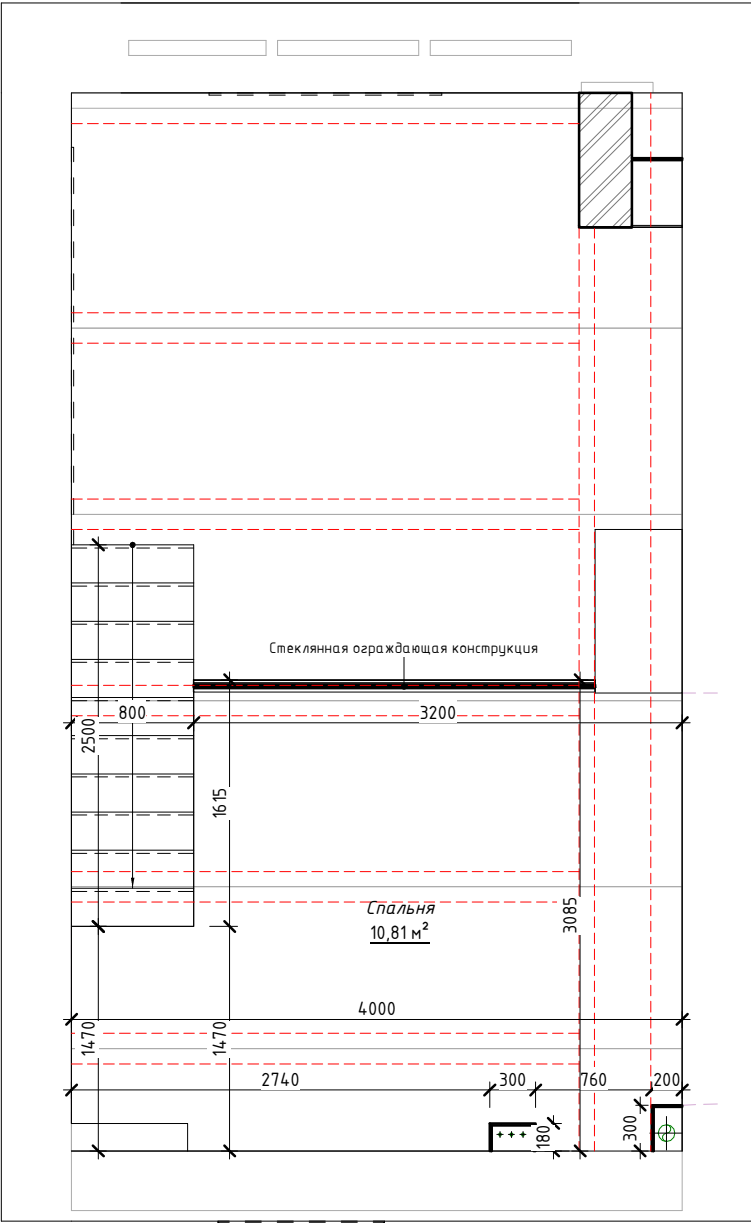


Экспликация помещений		
№ пом	Наименование	Площадь, м²
Этаж 1 (у.ч.п.)		
1	Кухня-Гостиная	20,87 м²
2	Санузел	4,71 м²
Этаж 1.5		
3	Спальня	10,81 м²
Общий итог: 3		36,39 м²

Примечание:
В проекте указаны монтажные размеры.
Высота потолков на момент замера - 3880мм


Дизайнер	г. Москва, Нижняя Красносельская, 26.7 кв.м.	Стадия	Лист
Клиент	План монтируемых перегородок	РП	12

Разрез по лестнице


1 : 30

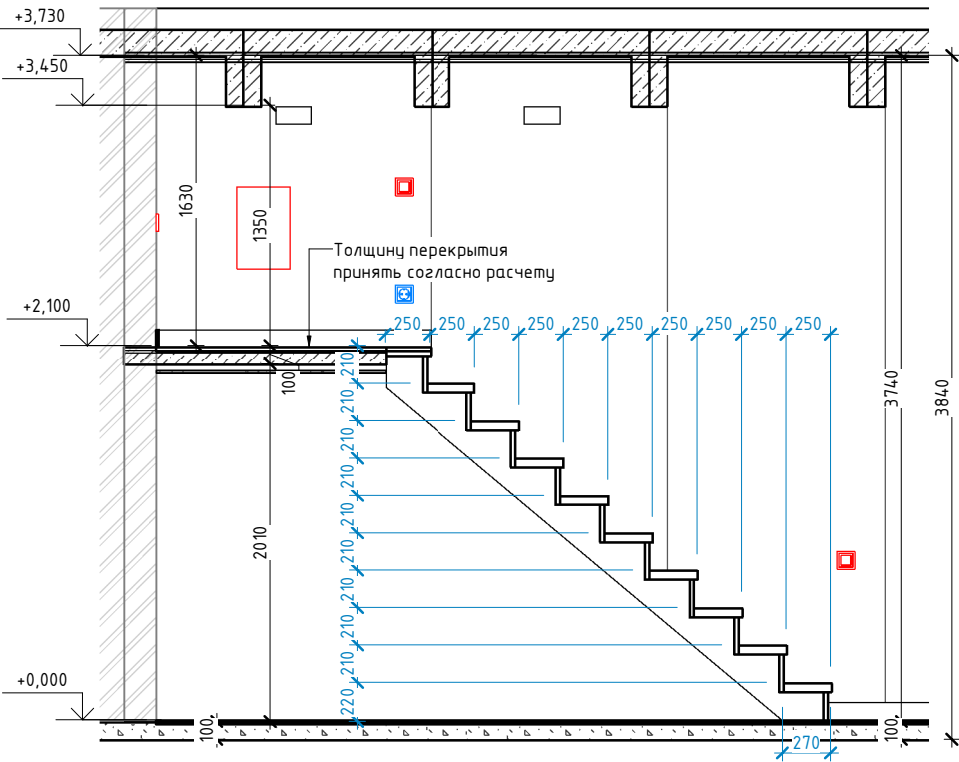

3D вид 1

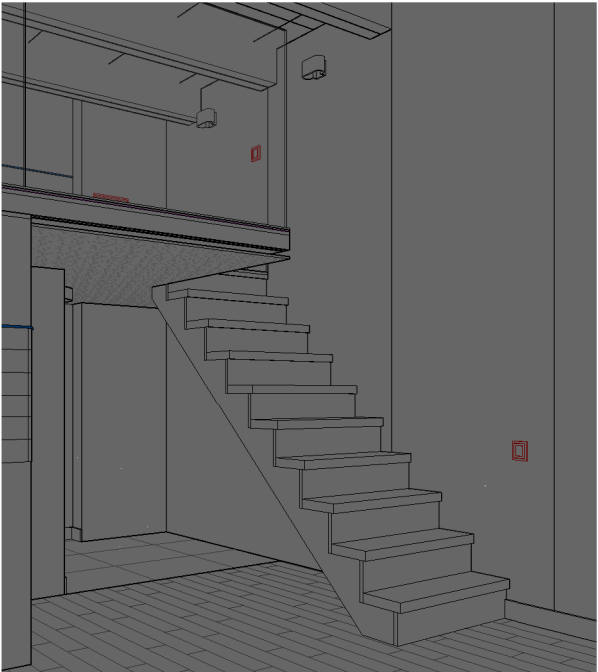

3D вид 2

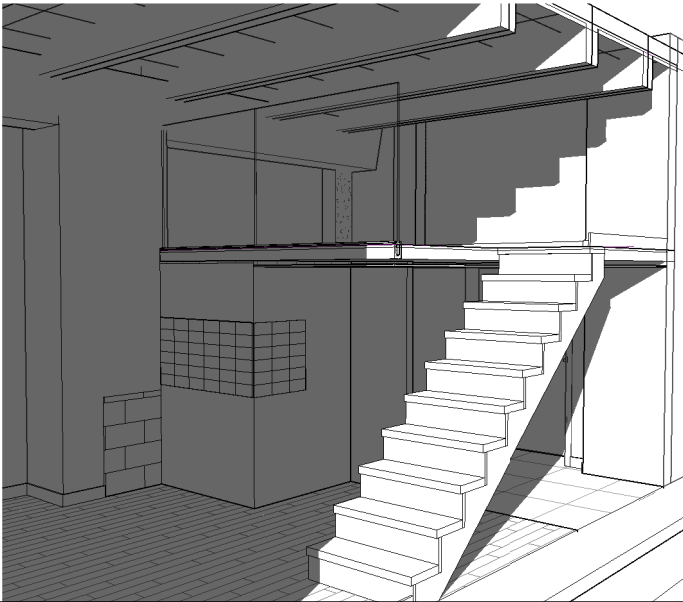


Дизайнер		г. Москва, Нижняя Красносельская, 26.7 кв.м.	Стадия	Лист
Клиент		Разрез по лестнице	РП	13

План мебели и оборудования 1

этажа


1:35

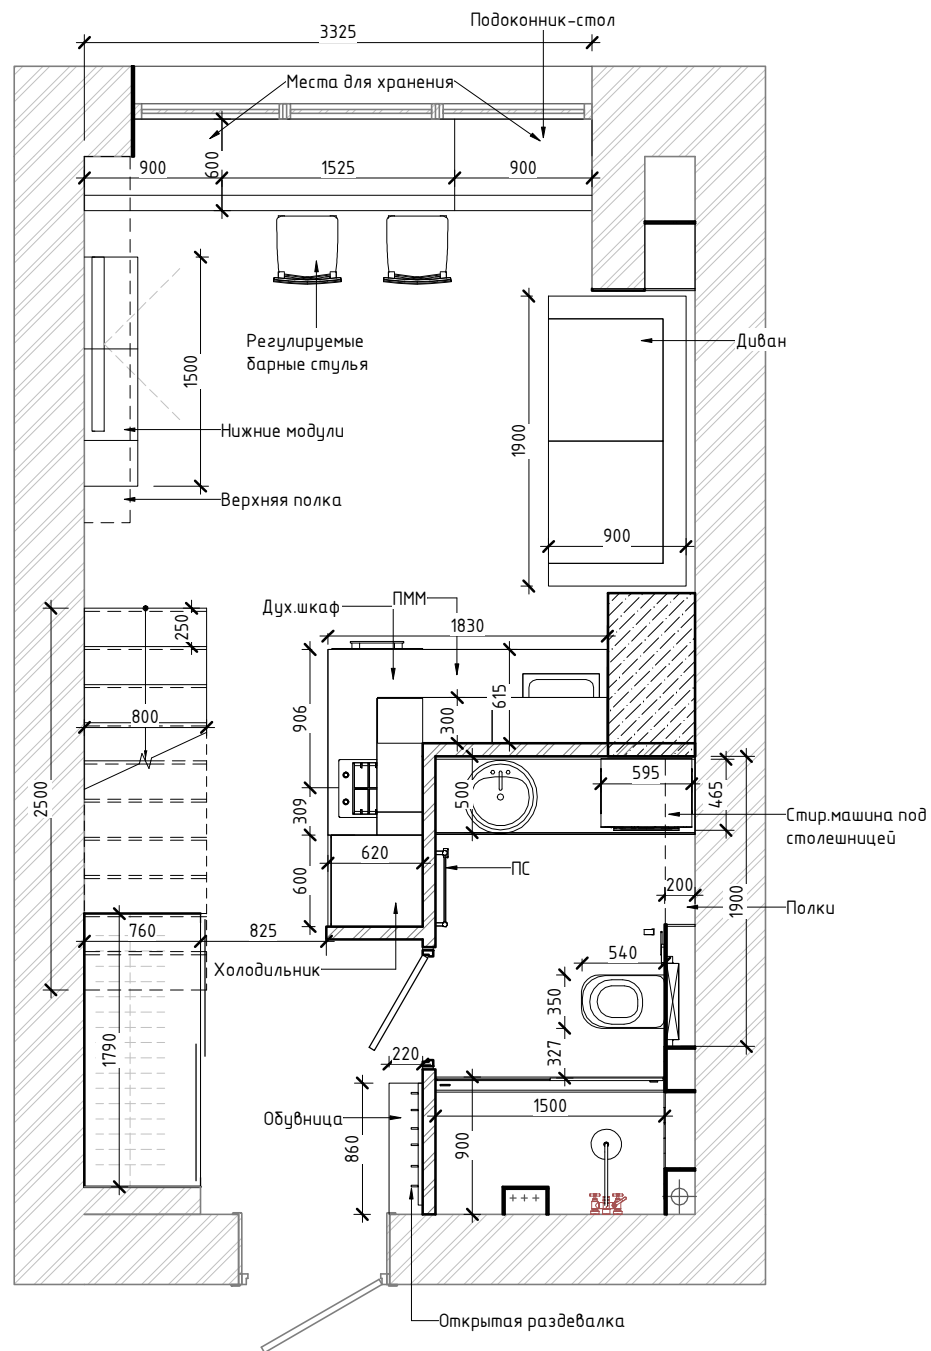

План мебели и оборудования. 2

этаж


1:35

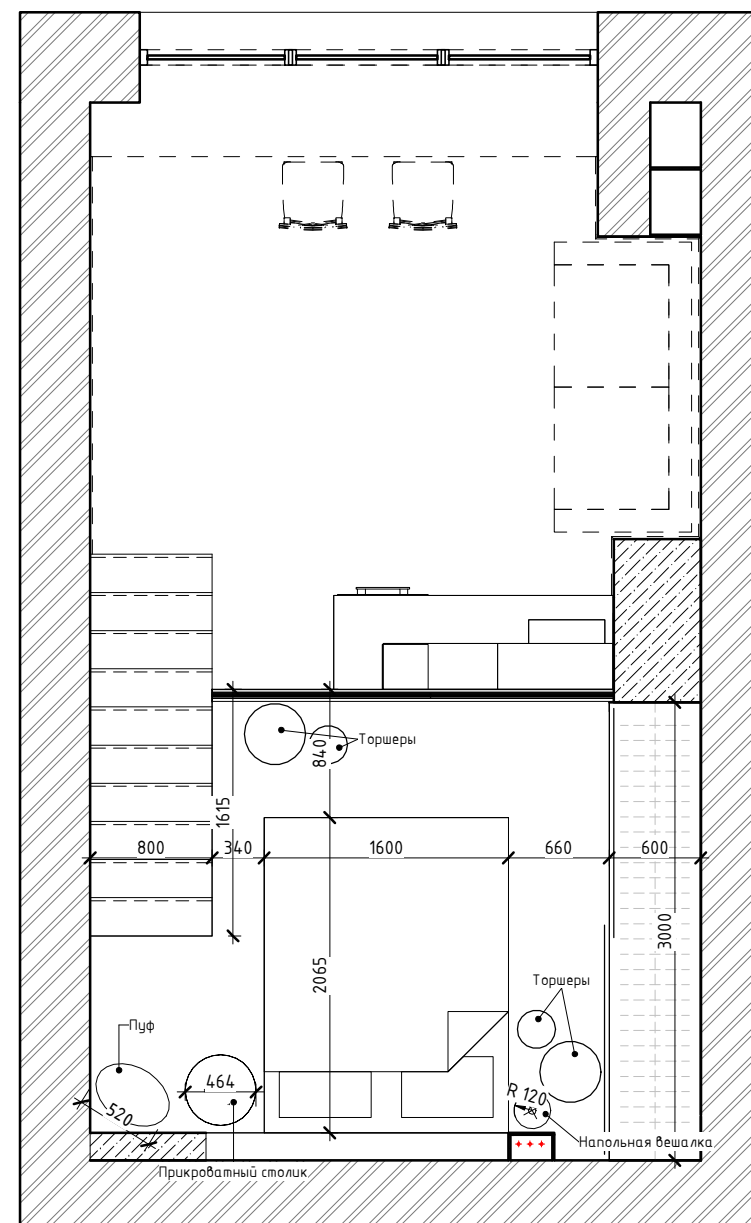

Дизайнер	г. Москва, Нижняя Красносельская, 26.7 кв.м.	Стадия	Лист
Клиент	План мебели и оборудования	РП	14

План заполнения дверных
проемов. 1 этаж


1:35

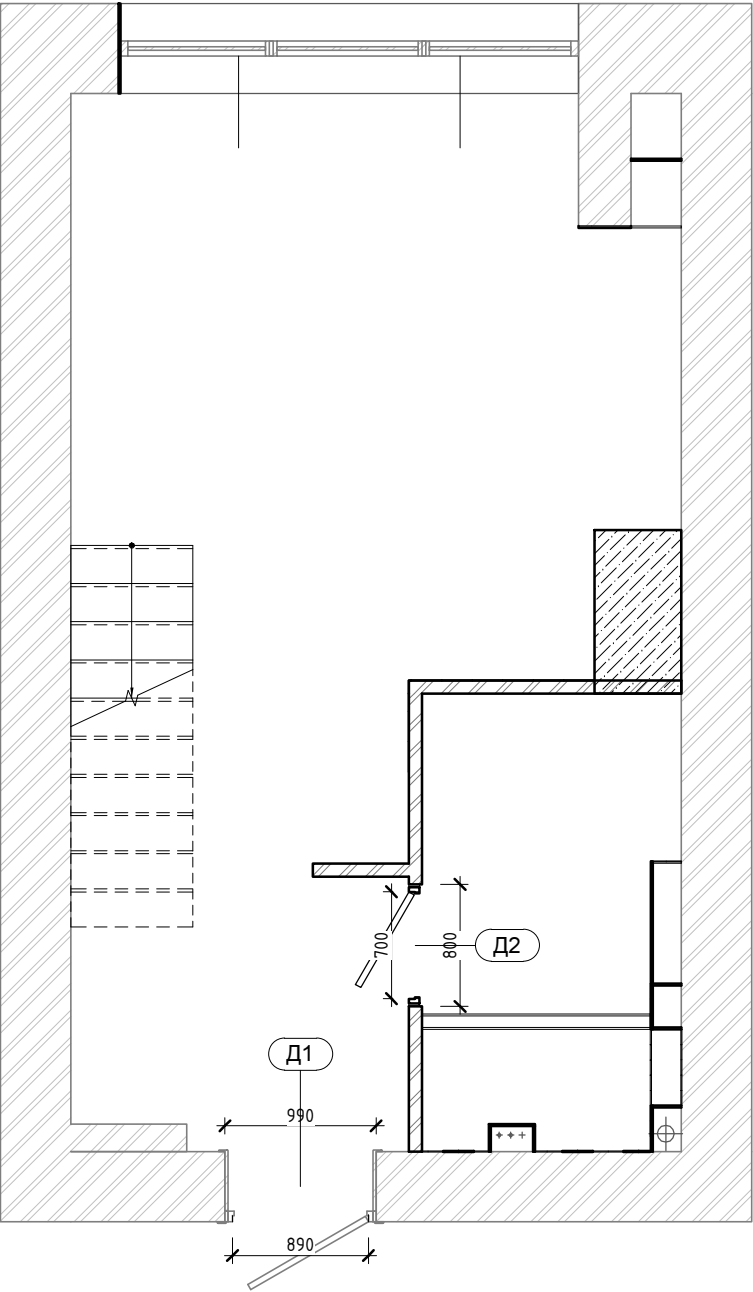


Заполнение дверных проемов		
Тип	Описание	Кол-во
Д1	Проем 990х1960мм для дверного полотна 890х1900мм. Дверь стальная наружная глухая.	1
Д2	Проем 800х1960мм для дверного полотна 700х1900мм. Дверь деревянная внутренняя глухая	1
Общий итог: 2		

Дизайнер		г. Москва, Нижняя Красносельская, 26.7 кв.м.	Стадия	Лист	
Клиент		План заполнения дверных проемов	РП	15	

План привязки сантехники 1 : 15

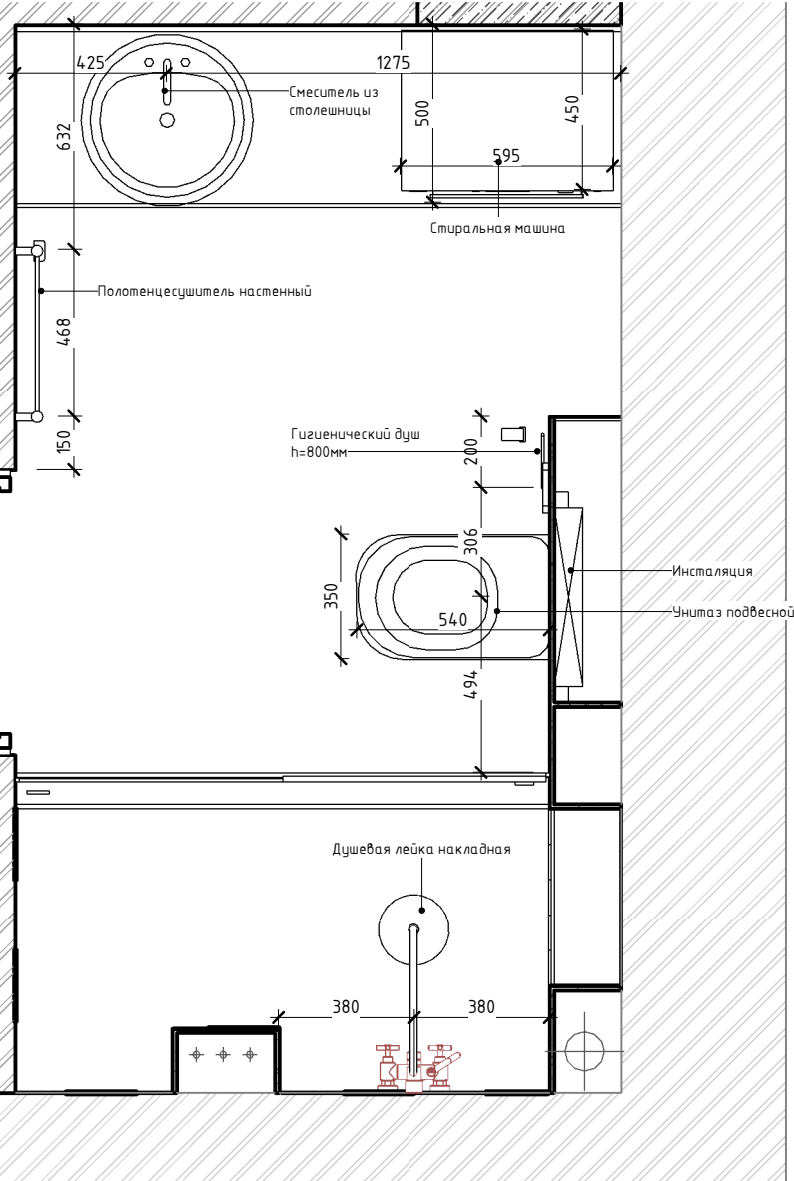


Душевая. Аксонометрия

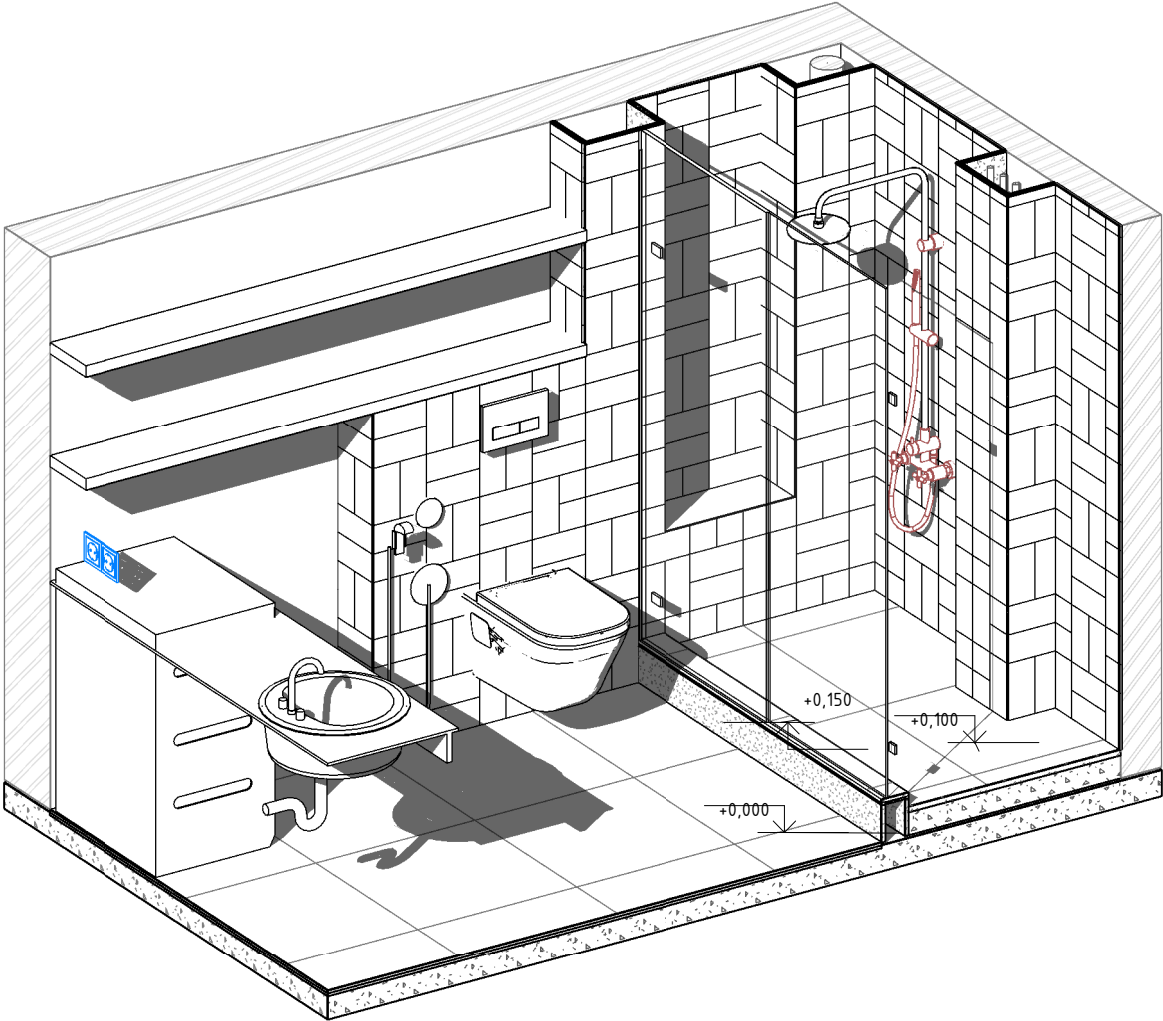


Дизайнер		г. Москва, Нижняя Красносельская, 26.7 кв.м.	Стадия	Лист
Клиент		План привязки сантехники	РП	16

1 : 35

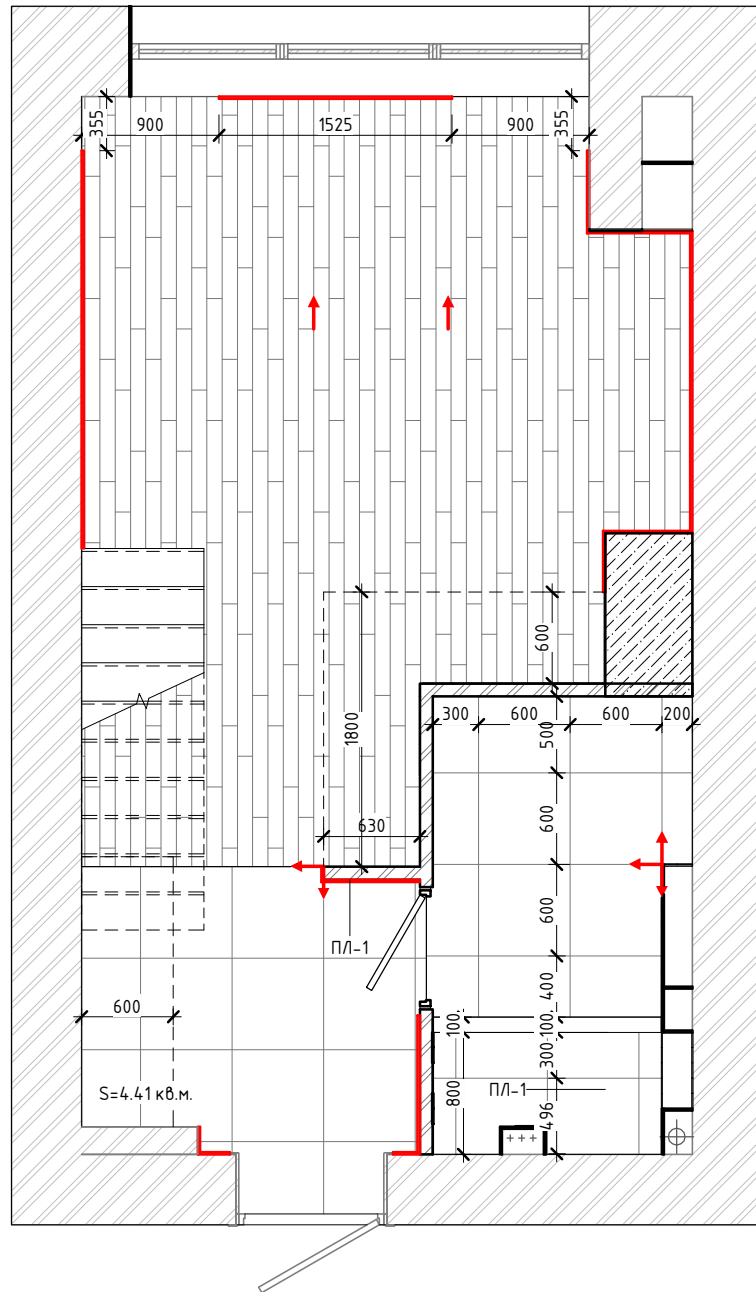

1 : 35

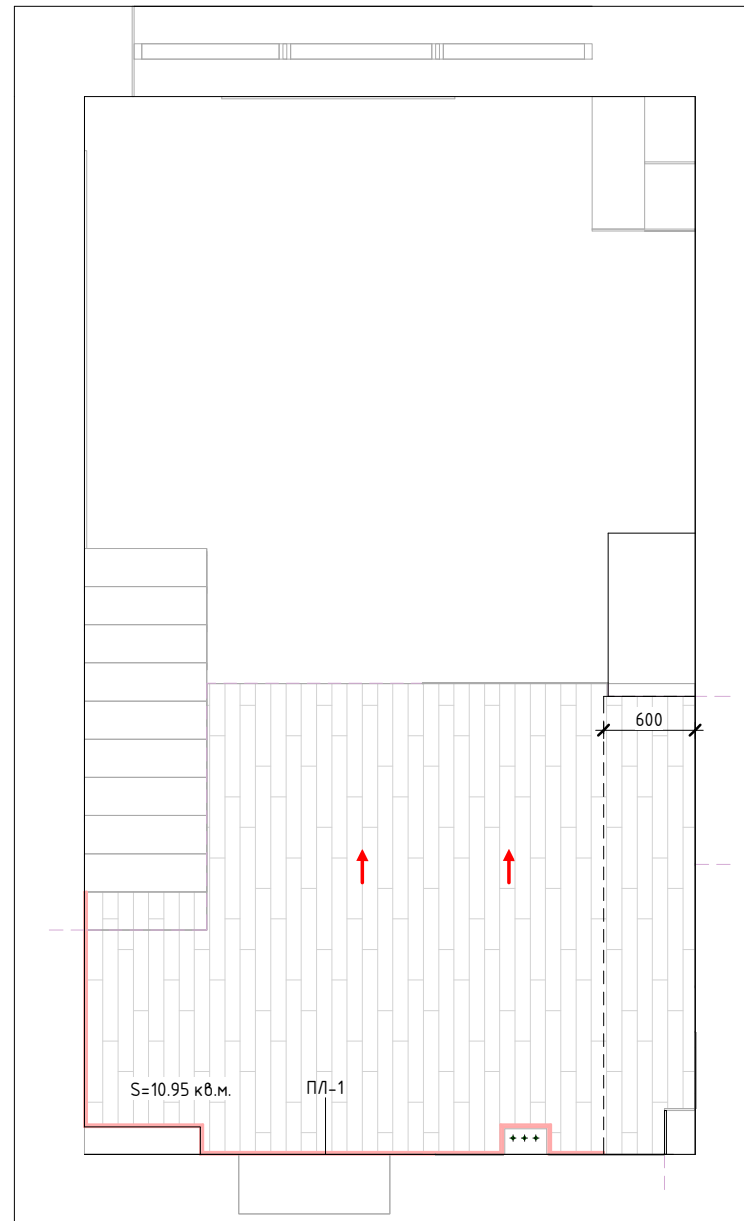


Ведомость напольных покрытий	
Наименование	Площадь
Керамогранит VZ 01 Venezia неполированный 600х600мм	9,11 м ²
Ламинат	27,83 м ²


Спецификация плитусов		
Марка	Наименование	Длина, мм
ПЛ-1	Плитус	15965

Дизайнер		г. Москва, Нижняя Красносельская, 26.7 кв.м.	Стадия	Лист	
Клиент		План напольных покрытий	РП	17	

План потолка. 1 этаж
1 : 35

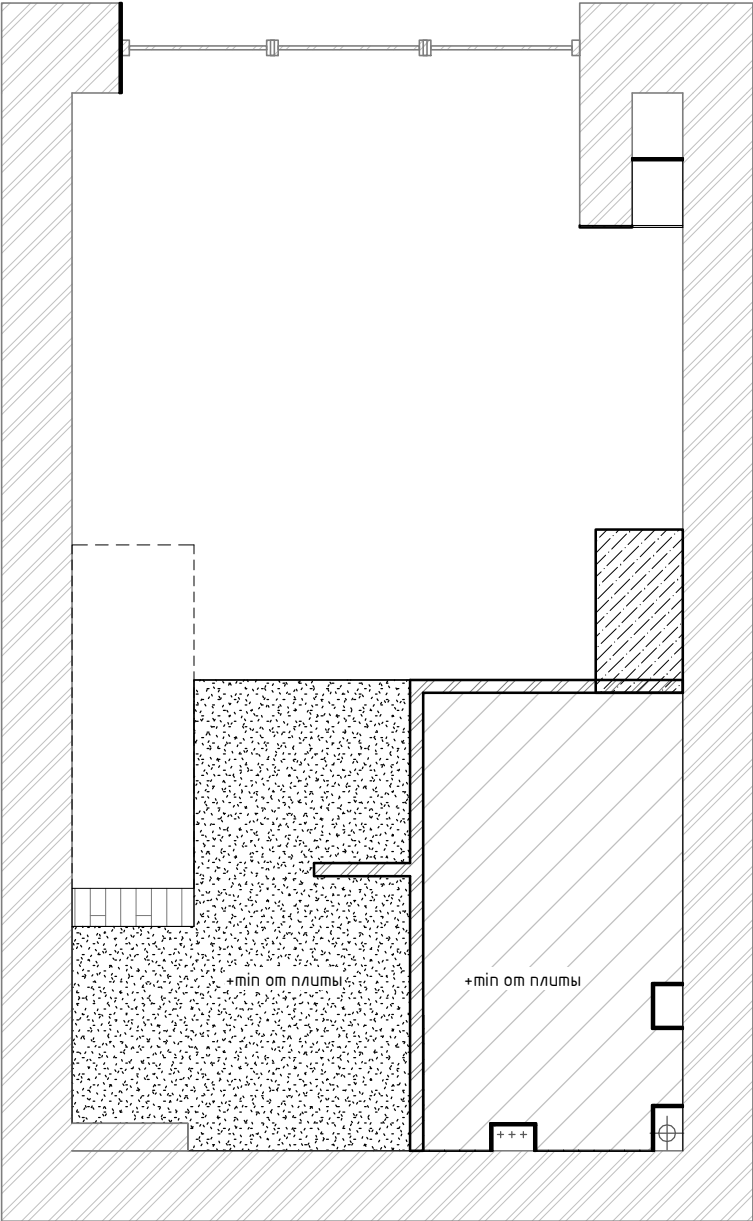

План потолка. 2 этаж
1 : 35

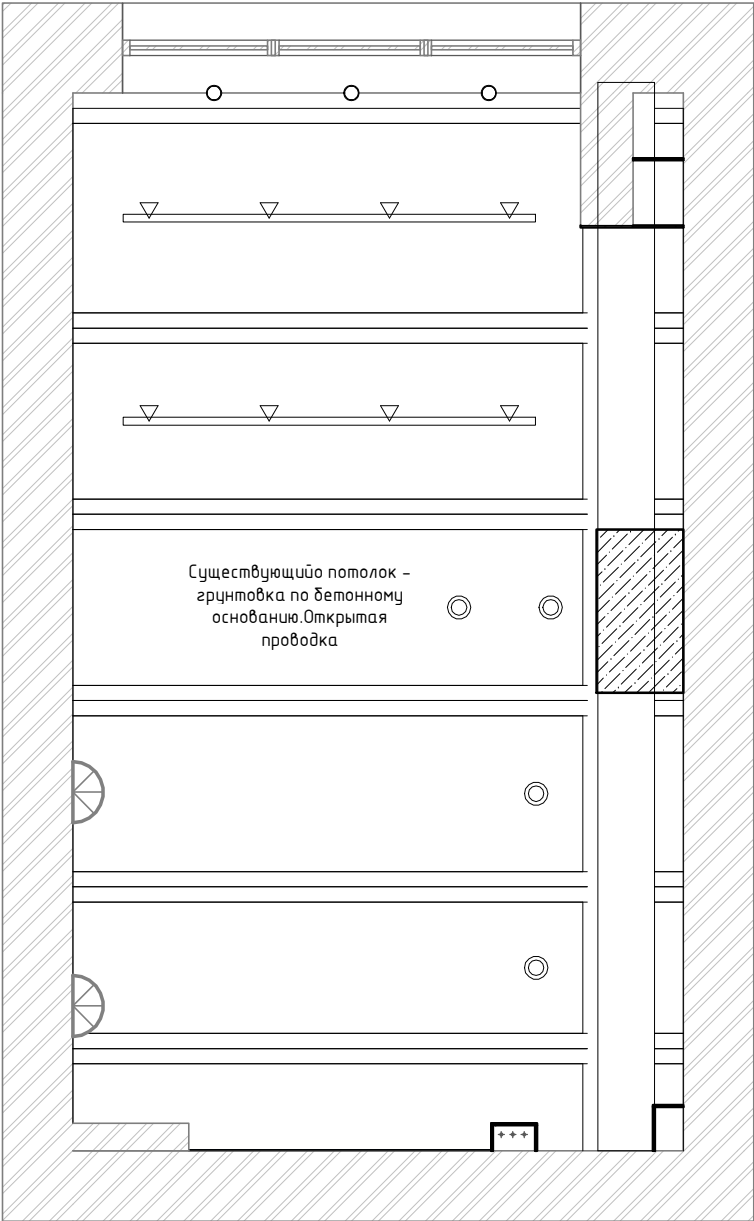


Ведомость материалов потолков		
Тип	Площадь	Помещения
Гипсокартон, краска белая Beckers Beckerplast	5,35 м²	Прихожая
Натяжной потолок	4,93 м²	Санузел
Существующий потолок. Грунтовка по бетонному основанию	27,72 м²	Гостиная - Кухня. Спальня


-  - ГКЛ, краска - белая Beckers Beckerplast
-  - Натяжной потолок
-  - Существующий потолок, покраска

Дизайнер		г. Москва, Нижняя Красносельская, 26.7 кв.м.	Стадия	Лист	
Клиент		План потолков	РП	18	

План осветительного
оборудования. 1 этаж
1: 35

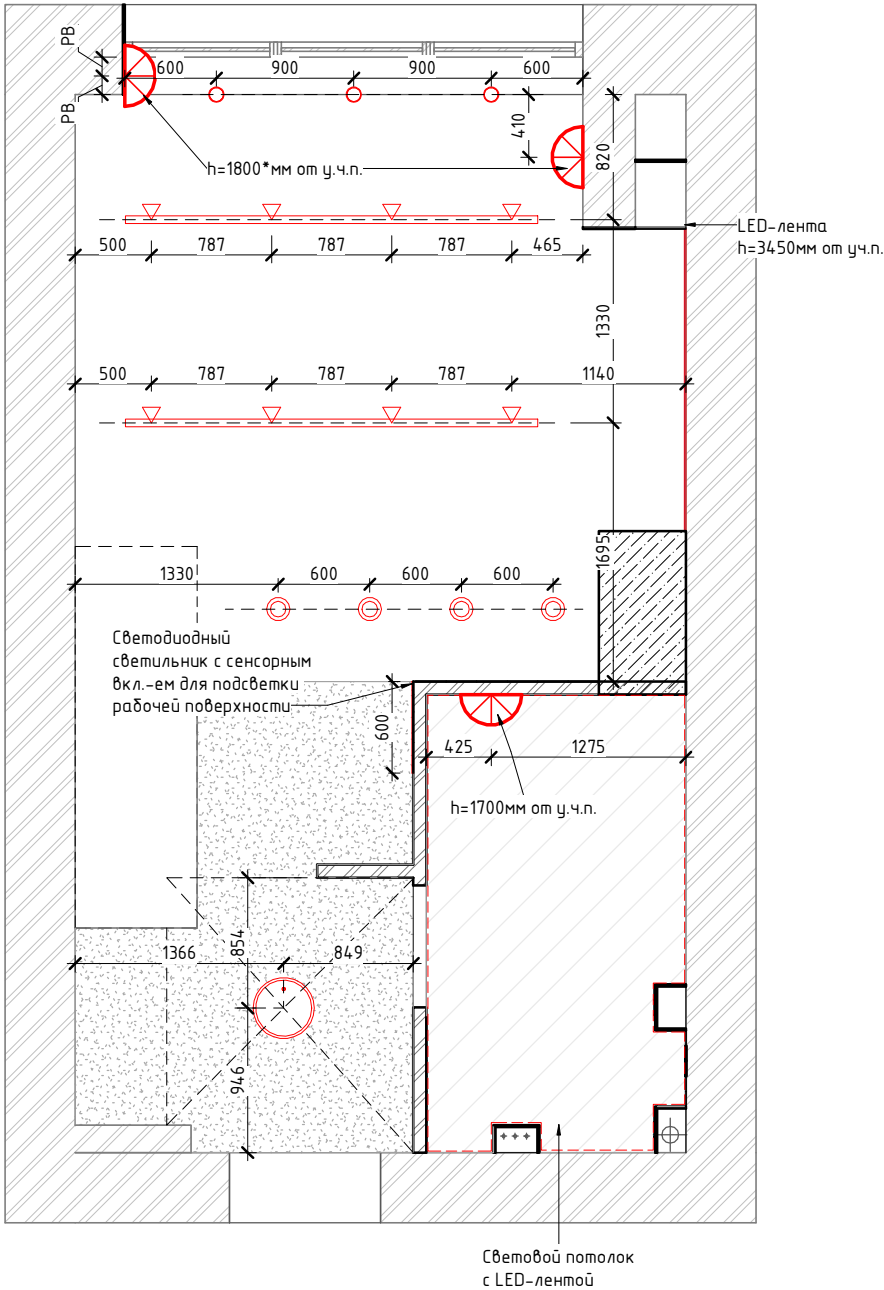


План осветительного
оборудования. 2 этаж
1: 35

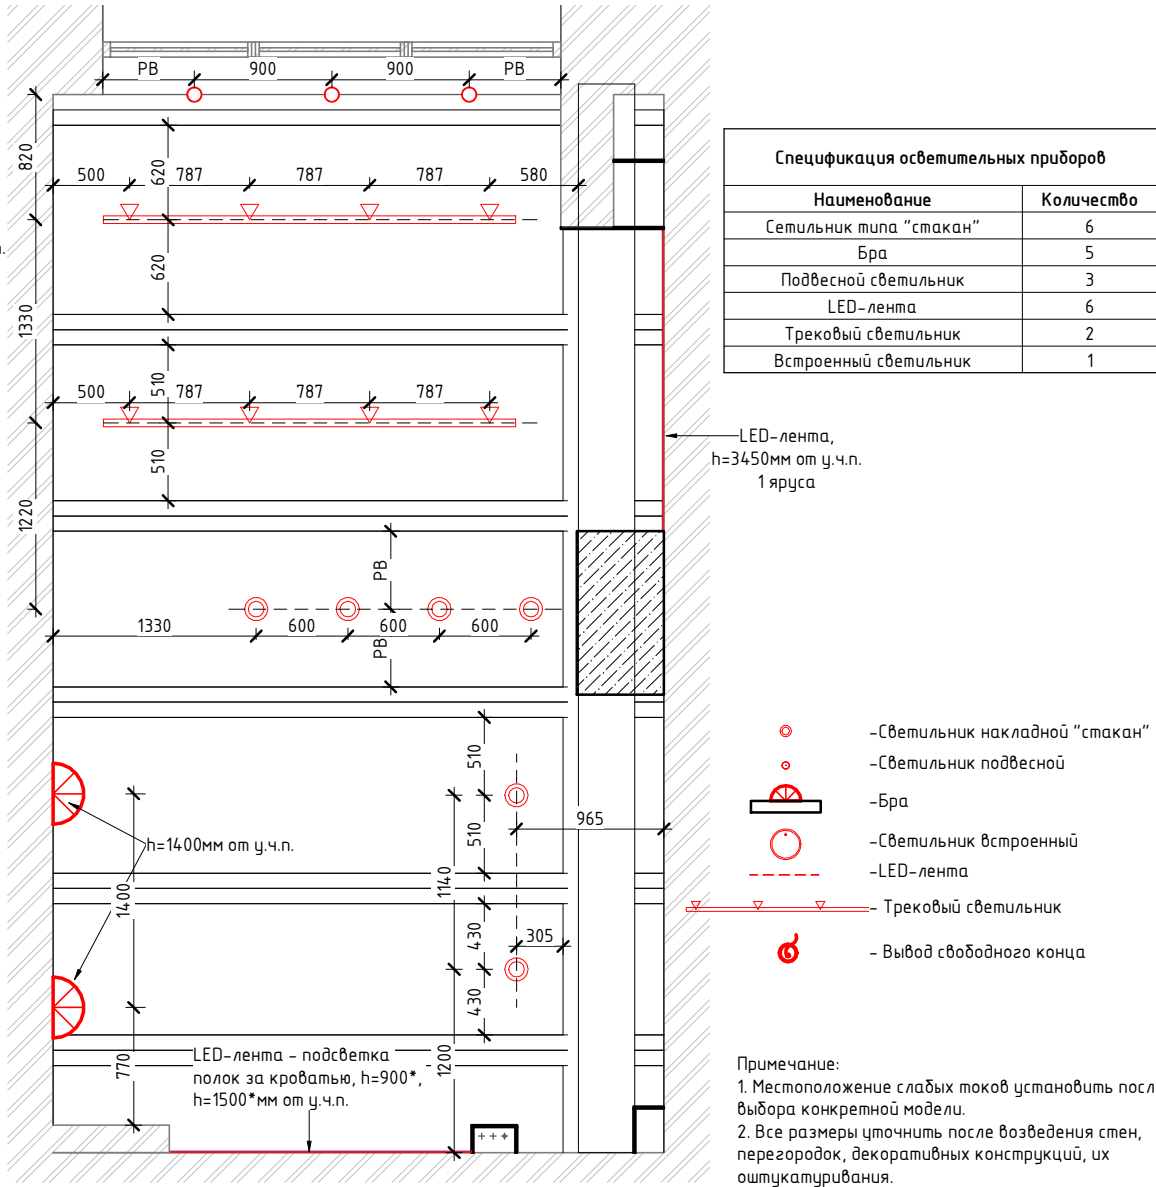


Дизайнер	г. Москва, Нижняя Красносельская, 26.7 кв.м.	Стадия	Лист
Клиент	План осветительного оборудования	РП	19

План осветительного
оборудования с мебелью. 1 этаж
1 : 35

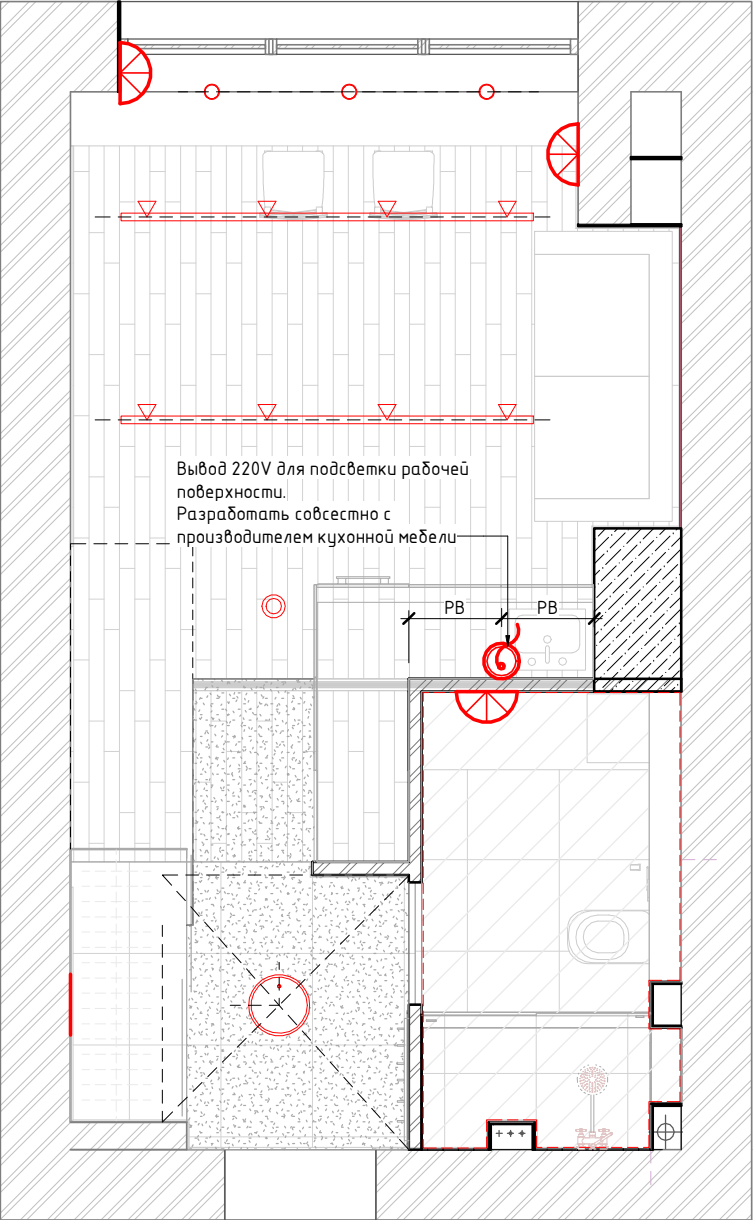

План осветительного
оборудования с мебелью. 2 этаж
1 : 35

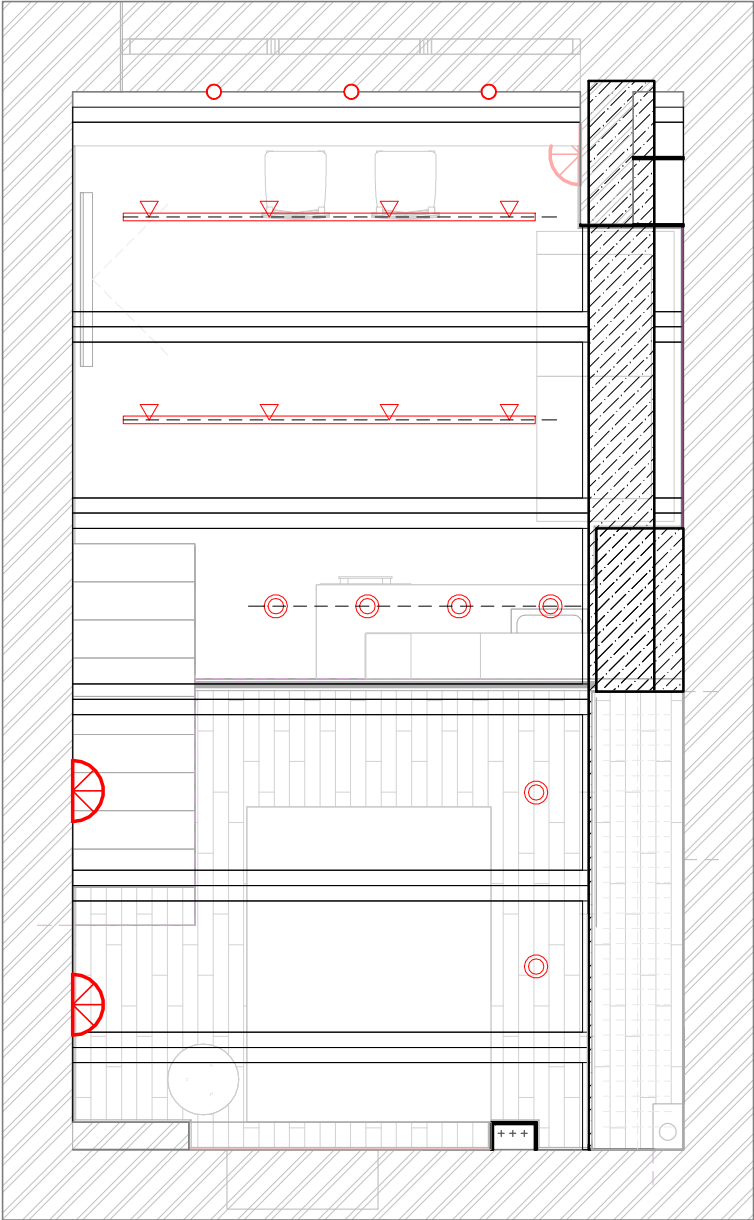


- -Светильник накладной "стакан"
- -Светильник подвесной
- ⌢ -Бра
- -Светильник встроенный
- - - LED-лента
- ▽ - Трековый светильник
- ⚡ - Вывод свободного конца


Примечание:
1. Местоположение слабых токов установить после выбора конкретной модели.
2. Все размеры уточнить после возведения стен, перегородок, декоративных конструкций, их оштукатуривания.

Дизайнер		г. Москва, Нижняя Красносельская, 26.7 кв.м.	Стадия	Лист	
Клиент		План осветительного оборудования с мебелью	РП	20	

1:35

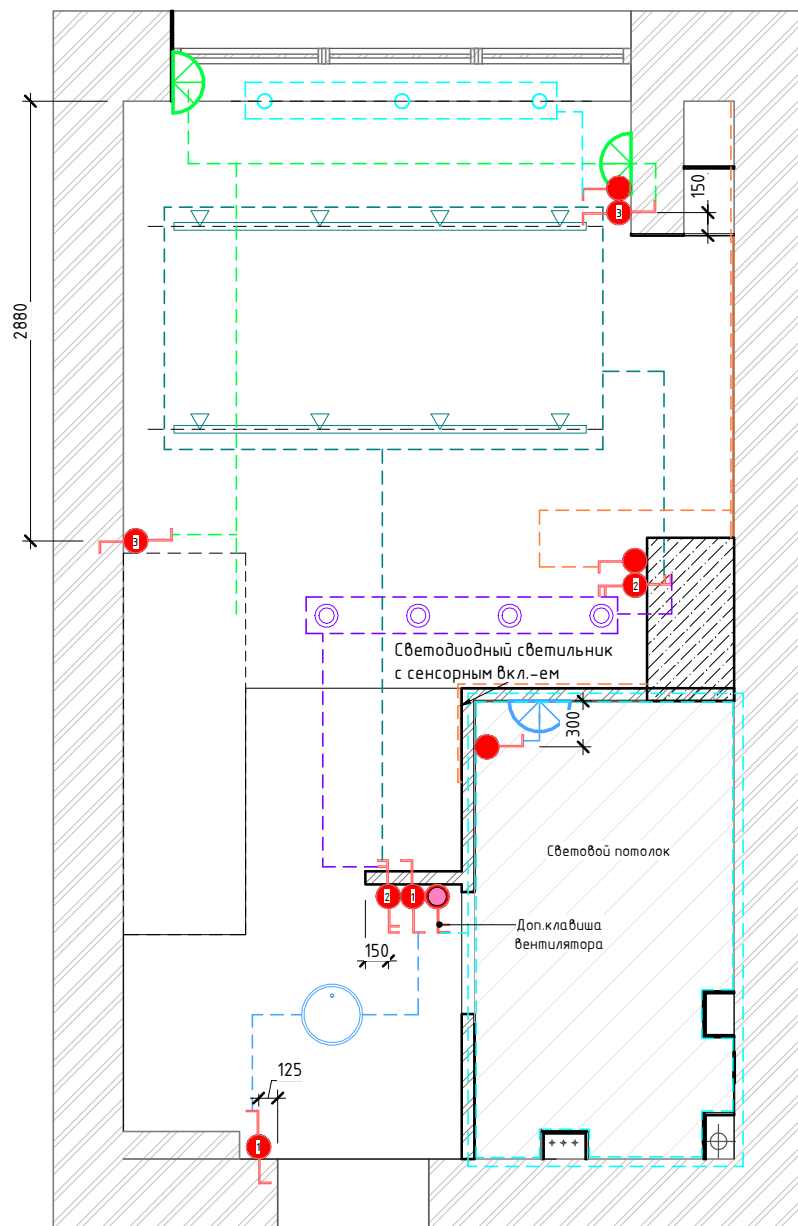


1:35

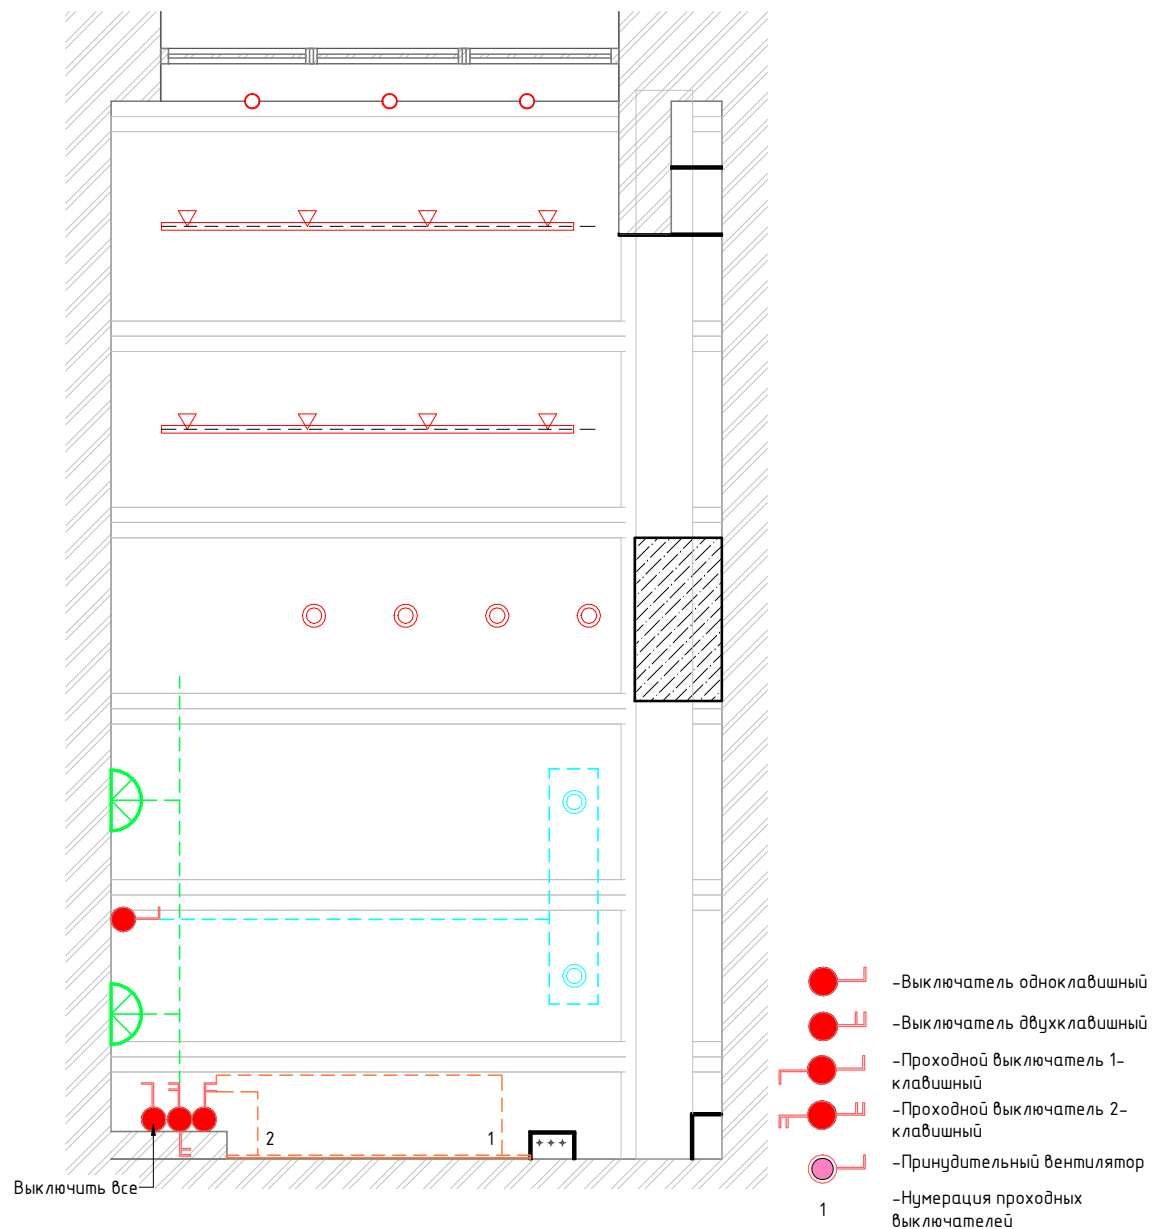

Дизайнер		г. Москва, Нижняя Красносельская, 26.7 кв.м.	Стадия	Лист	
Клиент		Привязка светильников и выключателей	РП	21	


Привязка выключателей и мебели. 1 этаж

1: 35

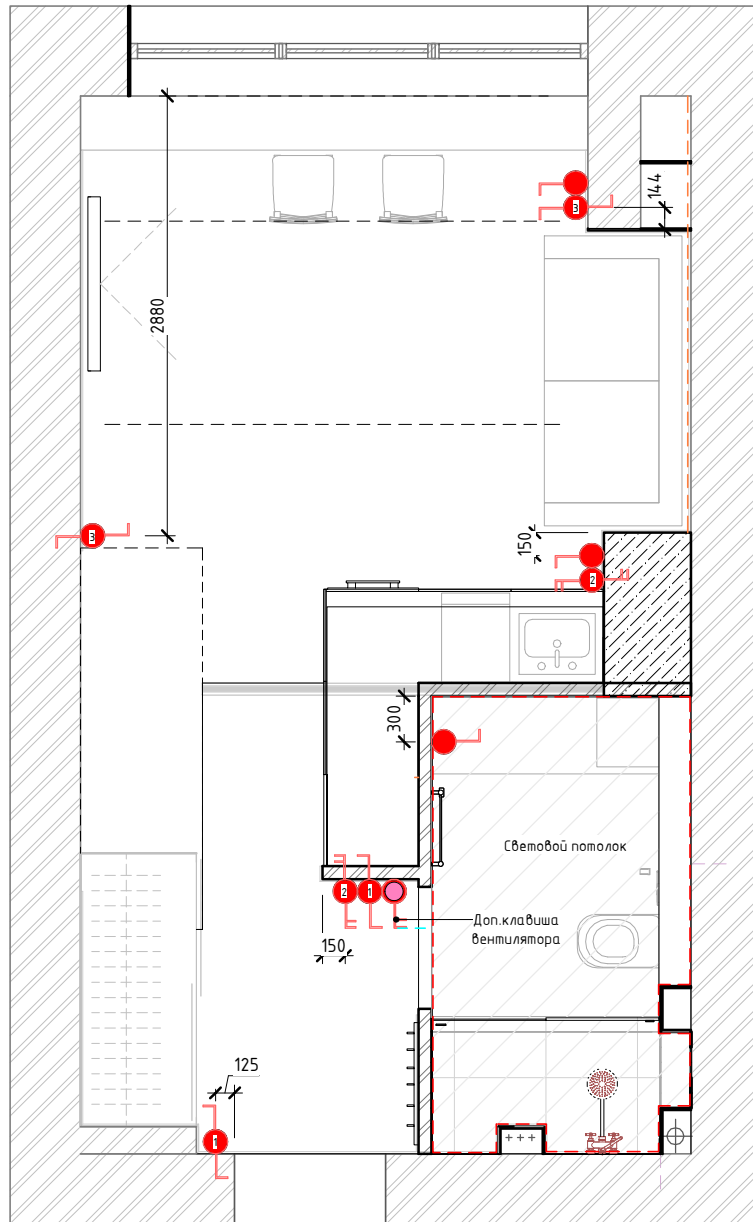

Привязка выключателей и мебели. 2 этаж


1: 35

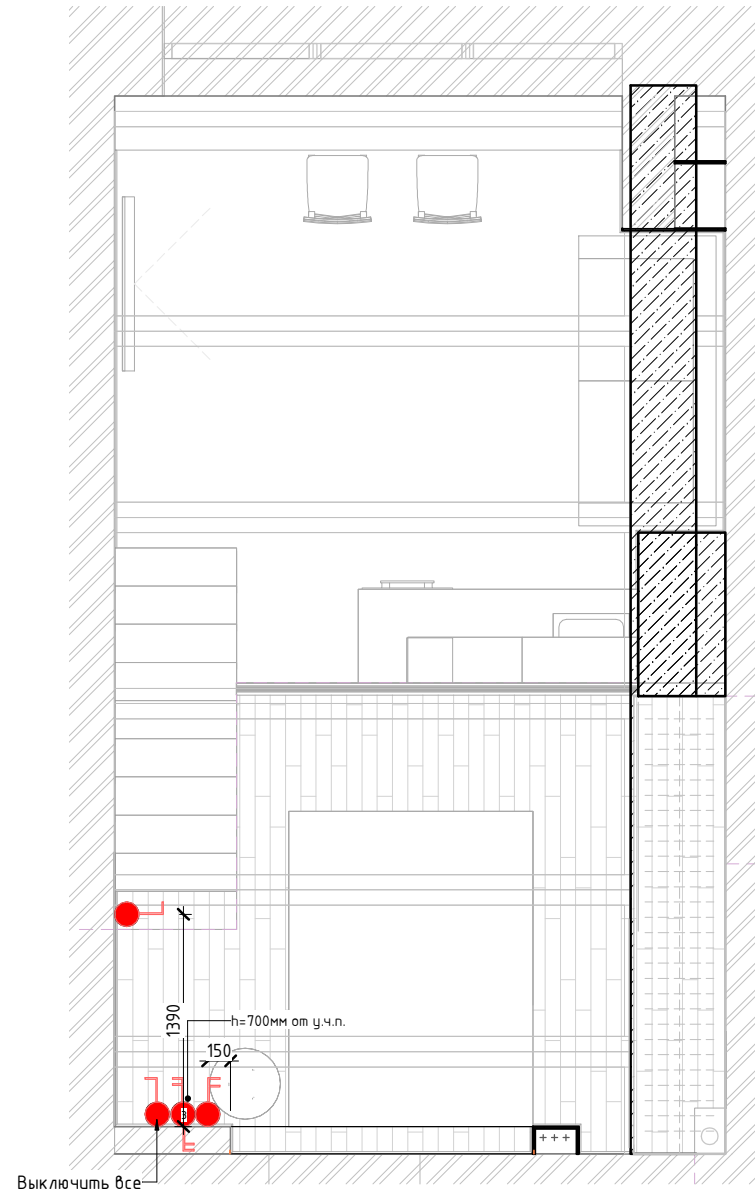


-  -Выключатель одноклавишный
-  -Выключатель двухклавишный
-  -Проходной выключатель 1-клавишный
-  -Проходной выключатель 2-клавишный
-  -Принудительный вентилятор
-  -Нумерация проходных выключателей

Дизайнер		г. Москва, Нижняя Красносельская, 26.7 кв.м.	Стадия	Лист	
Клиент		Привязка выключателей с мебелью	РП	22	

1:35

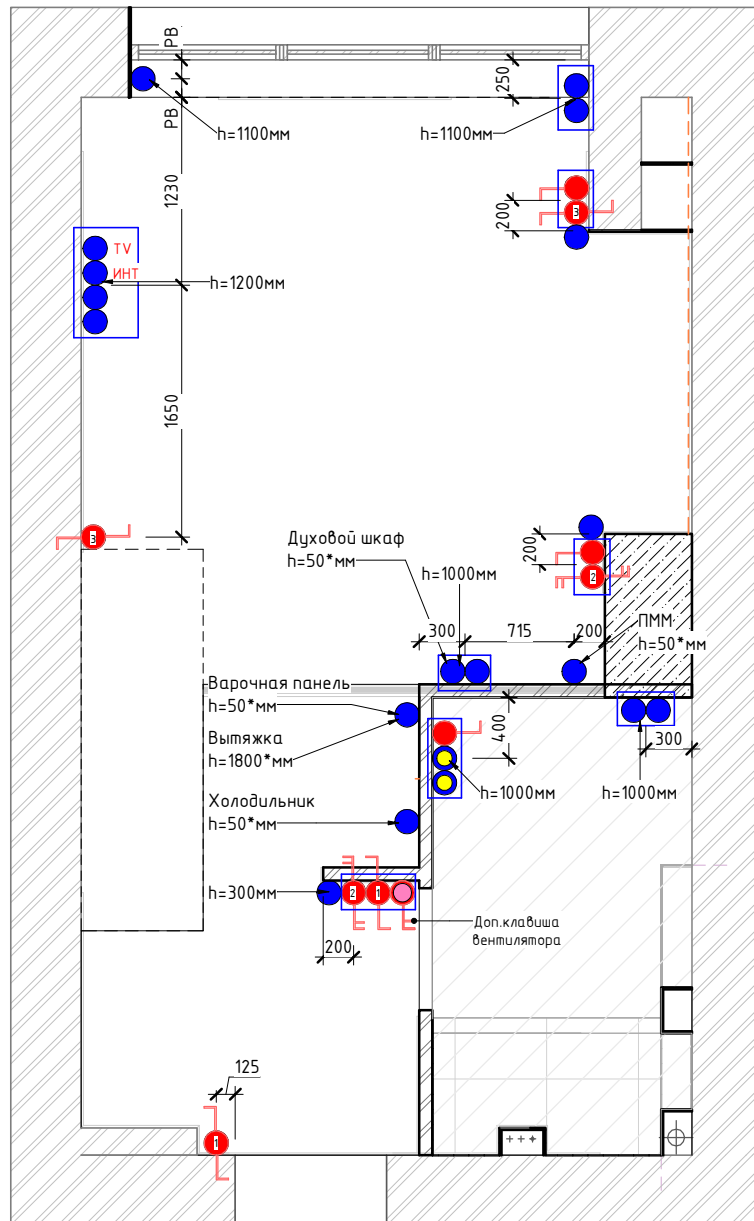

1:35

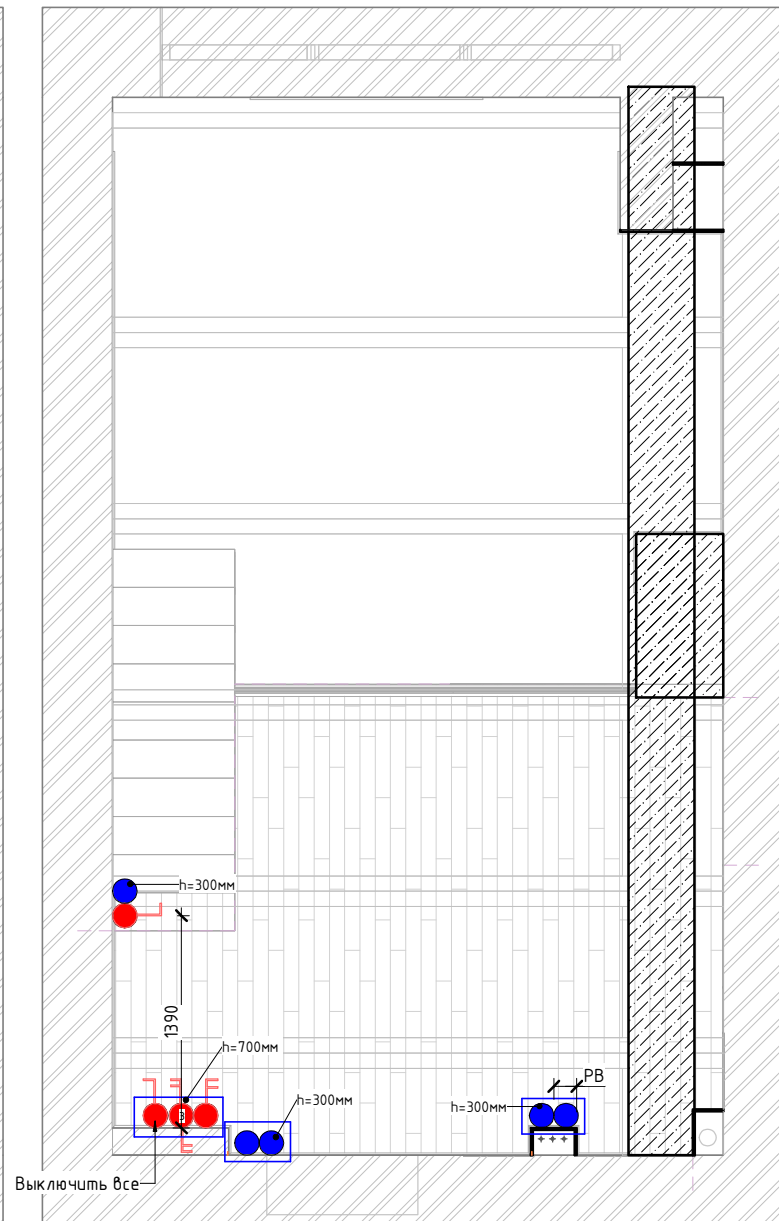

-  -Выключатель одноклавишный
 -  -Выключатель двухклавишный
 -  -Проходной выключатель 1-клавишный
 -  -Проходной выключатель 2-клавишный
 -  -Принудительный вентилятор
 -  -Нумерация проходных выключателей
- 1
-  -Розетка с защитным контактом IP20
 -  -Розетка интернет
 -  -Розетка ТВ
 -  -Розетка влагостойкая
- (с защитным контактом не менее IP44)

1. Местоположение слабых токов установить после выбора конкретной модели.
2. Все размеры следует уточнить после возведения стен, перегородок, декоративных конструкций, их оштукатуривания, а также после выбора конкретных моделей мебели и оборудования.
3. Концы выводов оставлять не менее 700мм.
4. Розетки и выключатели устанавливать блоками.
5. Все привязки даны по центрам групп.
6. Если участок стены не позволяет разместить нужное количество розеток и выключателей горизонтально, то разместить группы вертикально.

7. Все розетки, кроме особо оговоренных, установить на отм. h=300мм от уровня чистого пола и на расстоянии не менее 200мм от угол стен и проемов.
8. * – размер зависит от модели.
9. Все выключатели, кроме особо оговоренных, установить на отм. h=900мм от уровня чистого пола и на расстоянии не менее 200мм от угол стен и проемов.

10. Электрическую сеть выполнить с устройством заземляющего провода.
 11. Проводку выполнить из медного провода. Сечение провода принять по расчету.
 12. Данная схема является рекомендуемой по функциональной эксплуатации объекта, может быть откорректирована на стадии строительства с учетом технологических нюансов.
 13. Совместное обозначение розеток и выключателей обозначает общую рамку.
- Раздельное обозначение розеток и выключателей следует считать по группам в рамках.

Дизайнер		г. Москва, Нижняя Красносельская, 26.7 кв.м.	Стадия	Лист	
Клиент		План привязки розеток и выключателей	РП	23	

Схема размещения розеток,
выключателей и мебели. 1 этаж

1:35


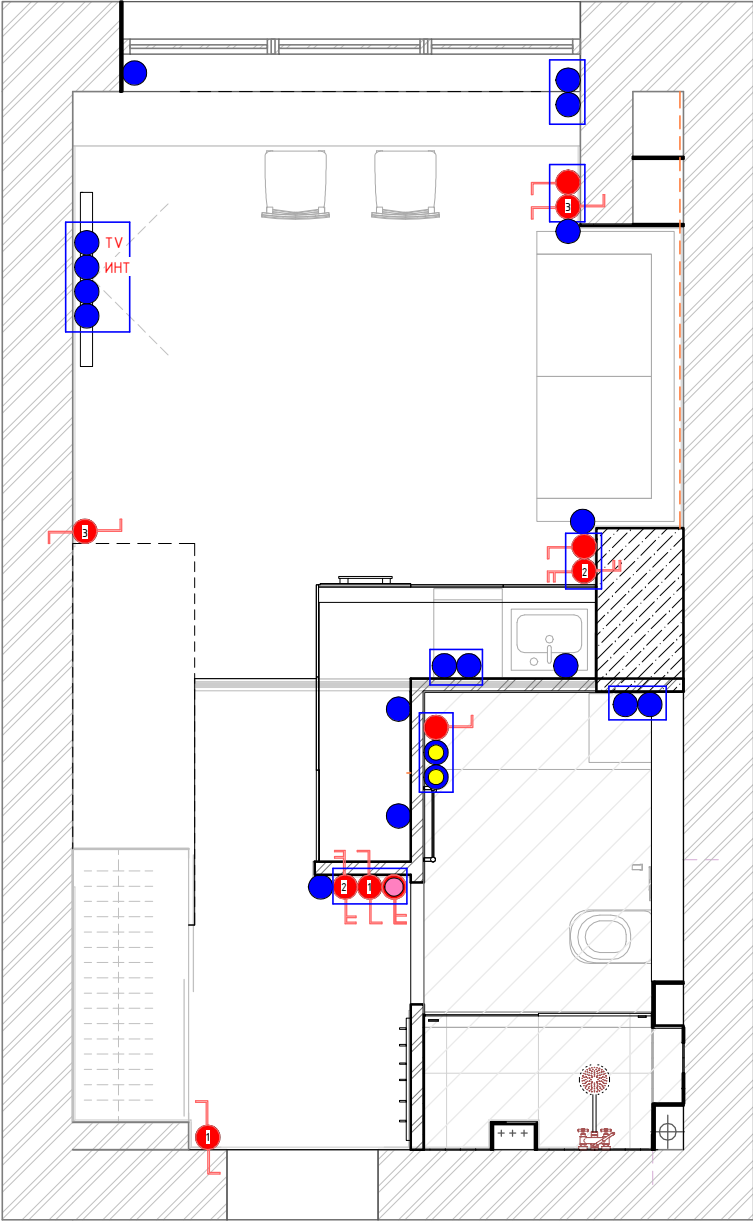


Схема размещения розеток,
выключателей и мебели. 2 этаж

1:35

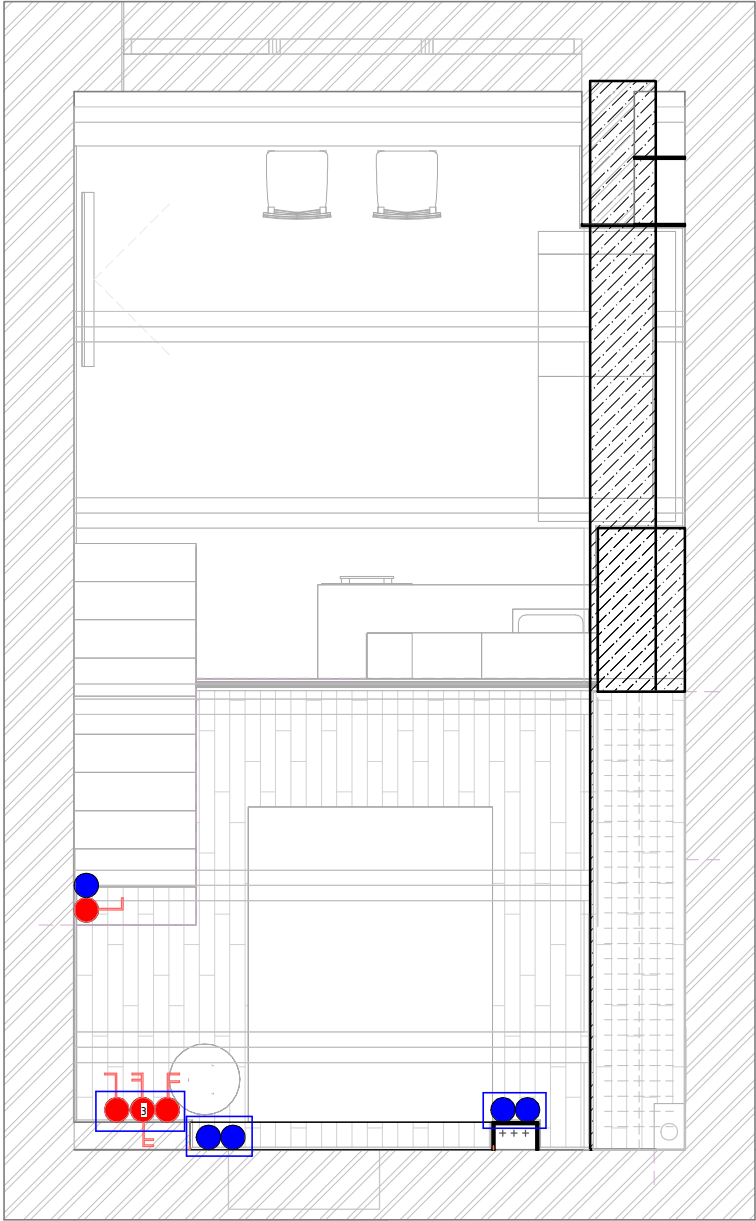


- -Розетка с защитным контактом IP20
- ИНТ ● -Розетка интернет
- ТВ ● -Розетка ТВ
- -Розетка влагостойкая (с защитным контактом не менее IP44)
- -Выключатель одноклавишный
- -Выключатель двухклавишный
- -Проходной выключатель 1-клавишный
- -Проходной выключатель 2-клавишный
- -Принудительный вентилятор
- 1 -Нумерация проходных выключателей

- Примечание:**
1. Местоположение слабых токов установить после выбора конкретной модели.
 2. Все размеры следует уточнить после возведения стен, перегородок, декоративных конструкций, их оштукатуривания, а также после выбора конкретных моделей мебели и оборудования.
 3. Концы выводов оставлять не менее 700мм.
 4. Розетки и выключатели устанавливать блоками.
 5. Все привязки даны по центрам групп.
 6. Если участок стены не позволяет разместить нужное количество розеток и выключателей горизонтально, то разместить группы вертикально.
 7. Все розетки, кроме особо оговоренных, установить на отм. $h=300\text{мм}$ от уровня чистого пола и на расстоянии не менее 200мм от угол стен и проемов.
 8. * -размер зависит от модели.
 9. Все выключатели, кроме особо оговоренных, установить на отм. $h=900\text{мм}$ от уровня чистого пола и на расстоянии не менее 200мм от угол стен и проемов.
 10. Электрическую сеть выполнить с устройством заземляющего провода.
 11. Проводку выполнить из медного провода. Сечение провода принять по расчету.
 12. Данная схема является рекомендуемой по функциональной эксплуатации объекта, может быть откорректирована на стадии строительства с учетом технологических нюансов.
 13. Совместное обозначение розеток и выключателей обозначает общую рамку. Раздельное обозначение розеток и выключателей следует считать по группам в рамках.

Дизайнер	г. Москва, Нижняя Красносельская, 26.7 кв.м.	Стадия	Лист
Клиент	Схема размещения розеток, выключателей и мебели	РП	24


План отделки стен. 1 этаж

1:35

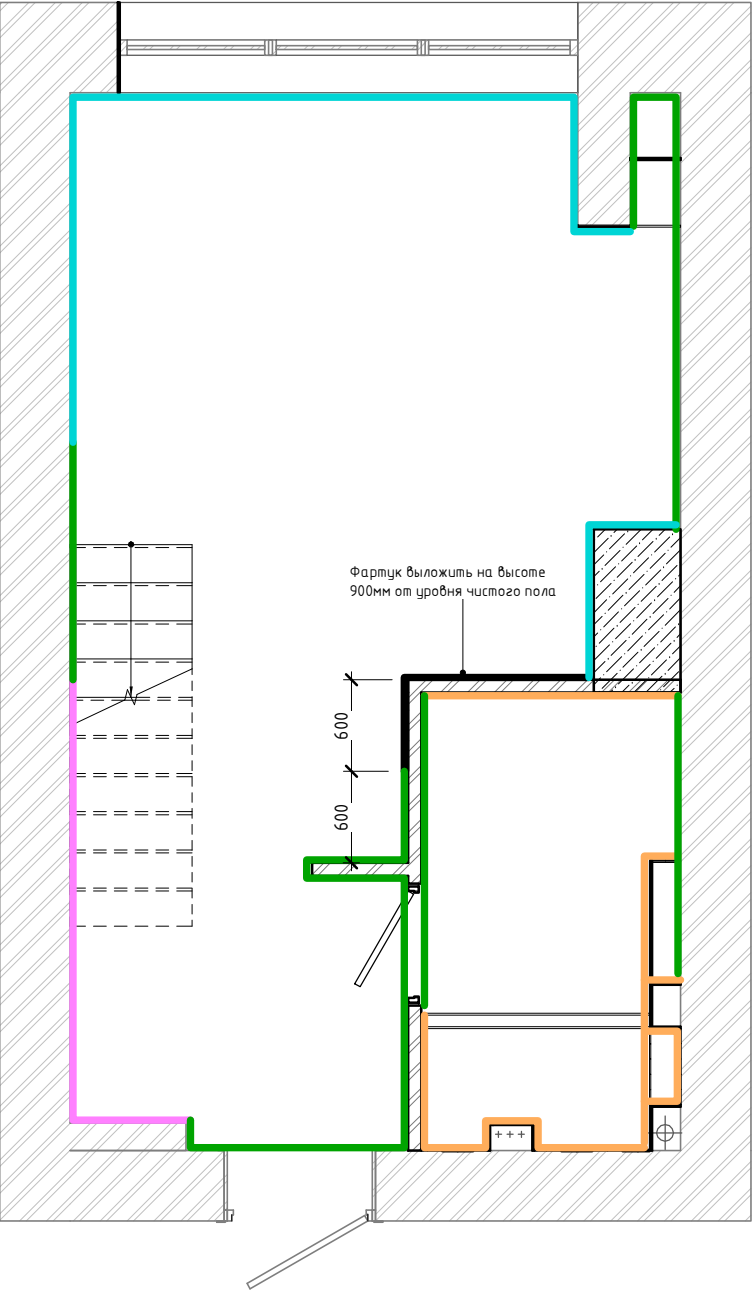

План отделки стен. 2 этаж

1:35

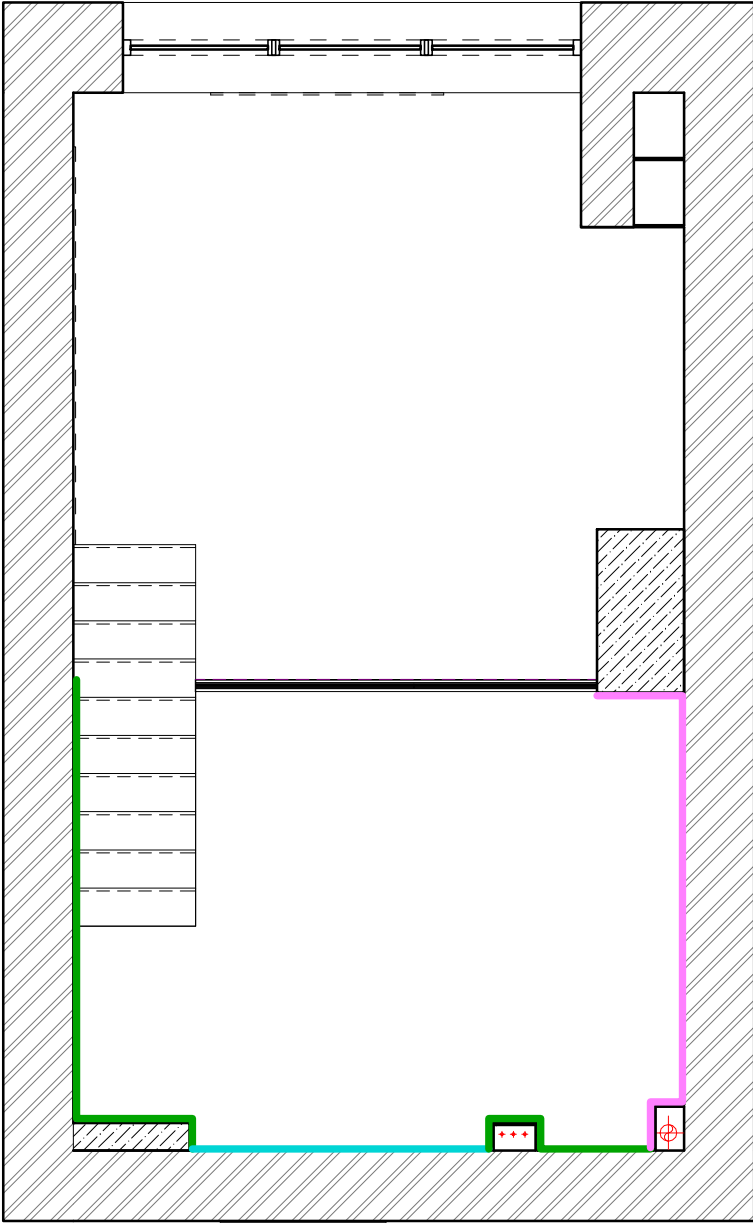

- Плитка
- Технический выкрас
- Декоративный облицовочный кирпич
- Покраска
- Фартук

За мебелью кухни – технический выкрас, фартук кухни –плитка

Дизайнер		г. Москва, Нижняя Красносельская, 26.7 кв.м.	Стадия	Лист	
Клиент		План отделки стен	РП	25	

Схема развертки стен. 1 этаж

1: 35



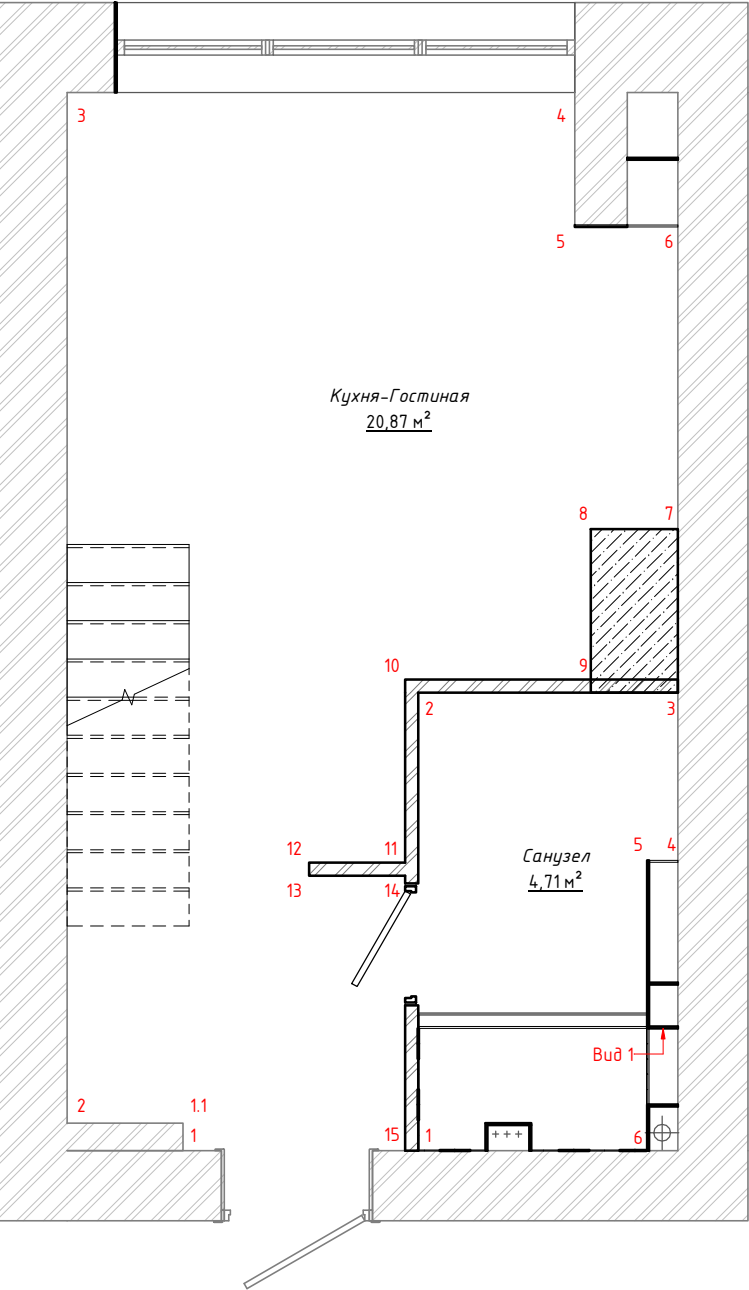


Схема развертки стен. 2 этаж

1: 35


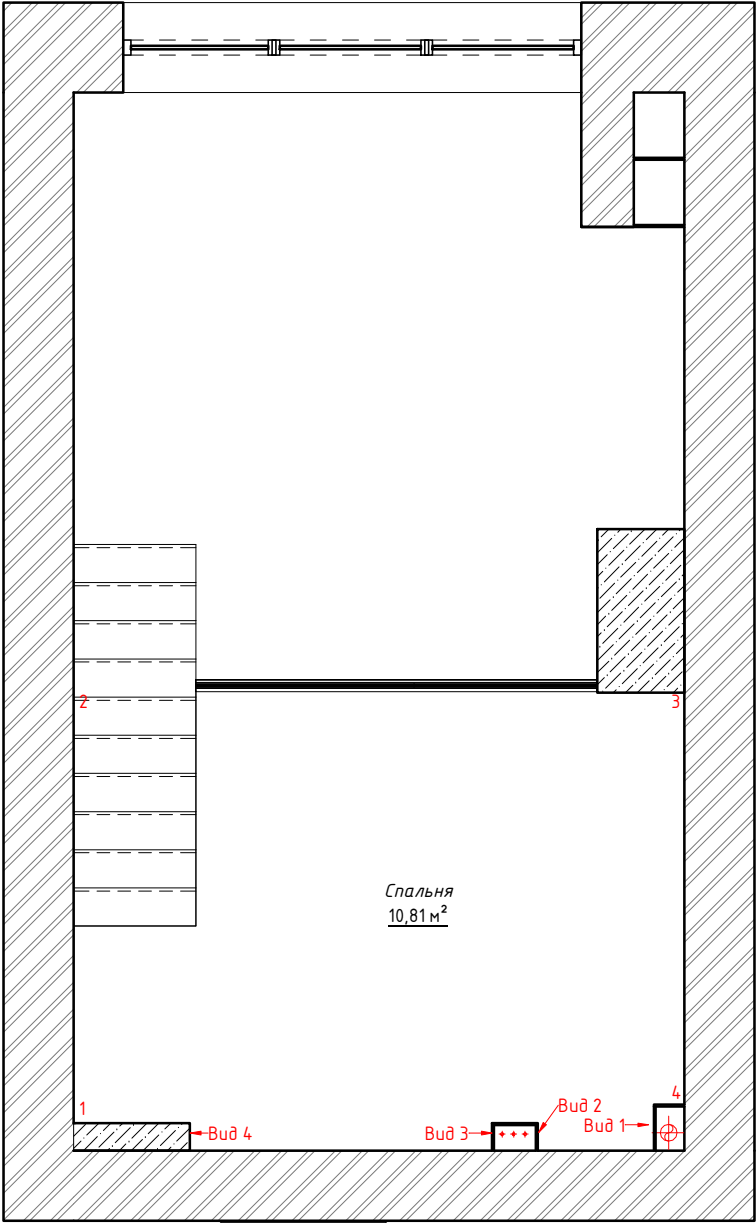


Дизайнер		г. Москва, Нижняя Красносельская, 26.7 кв.м.	Стадия	Лист	
Клиент		Схема развертки стен	РП	26	

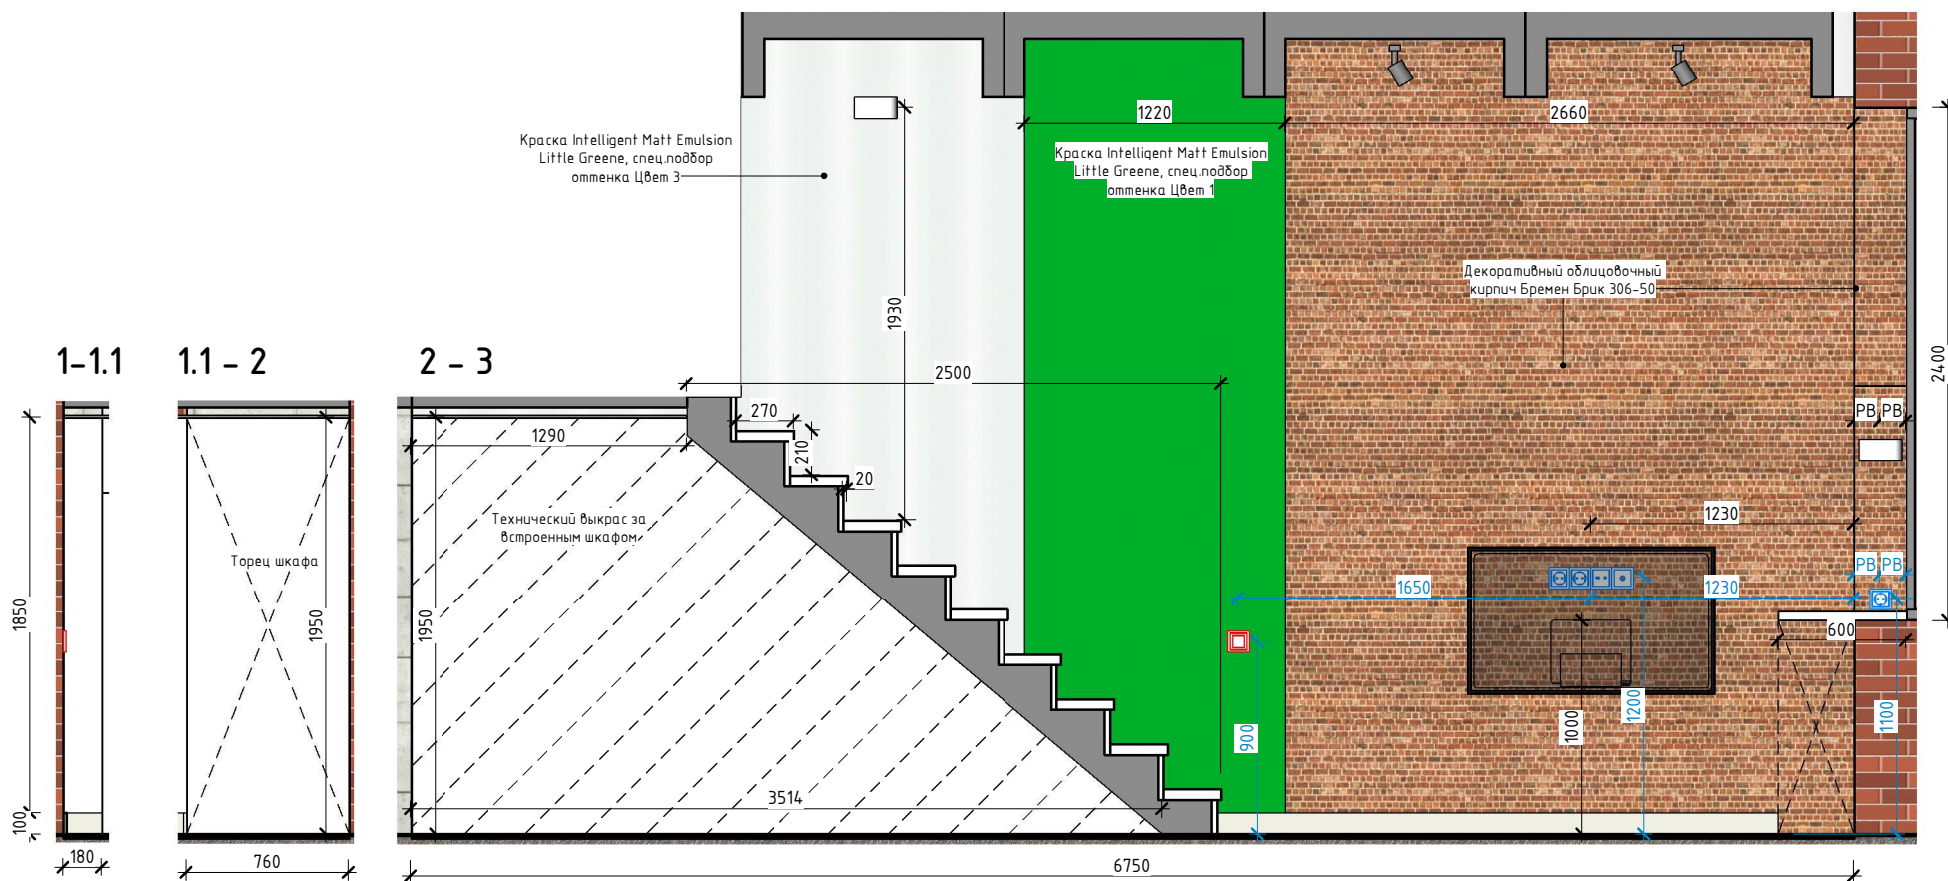


Дизайнер		г. Москва, Нижняя Красносельская, 26.7 кв.м.	Стадия	Лист	
Клиент		Развертка Гостиной-Кухни	РП	28	


3 - 4

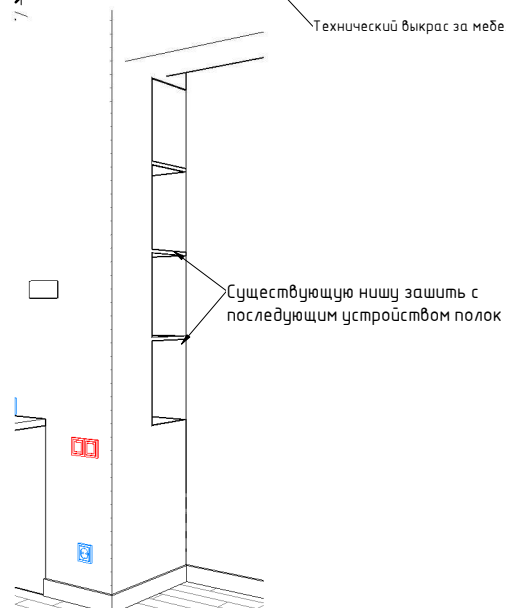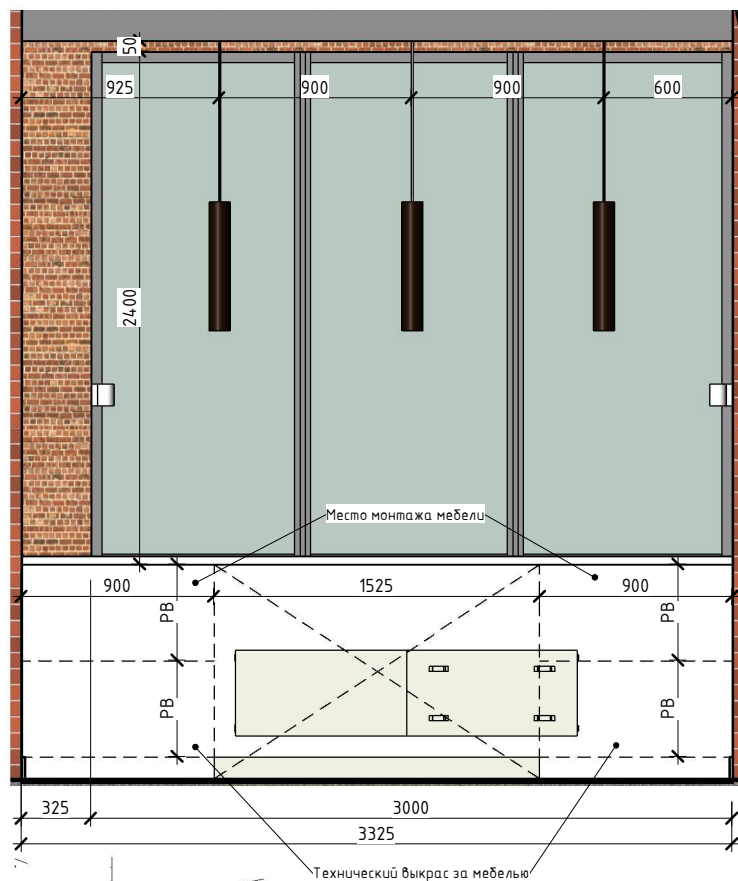


4 - 5

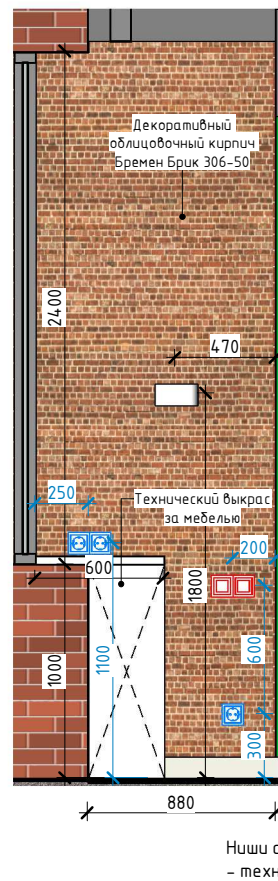


5 - 6

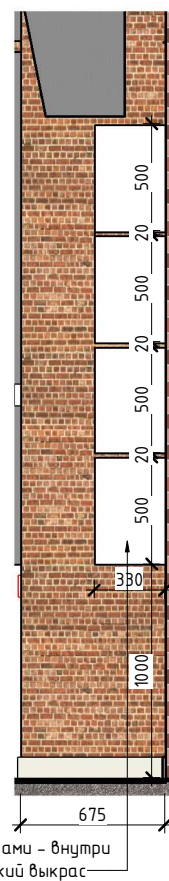

6 - 7

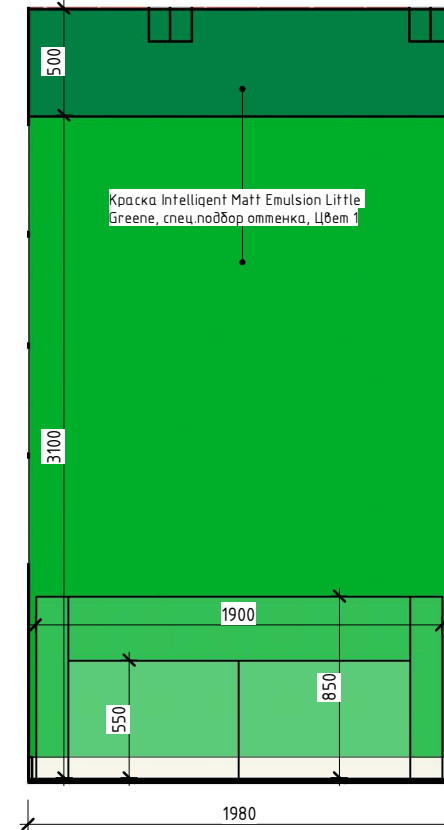


7 - 8






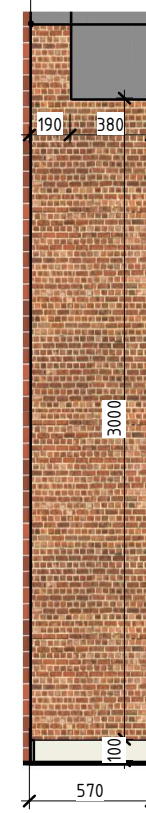
LED-лента -
подсветка за балкой

Дизайнер		г. Москва, Нижняя Красносельская, 26.7 кв.м.	Стадия	Лист	
Клиент		Развертка Гостиной-Кухни	РП	29	

8 - 9

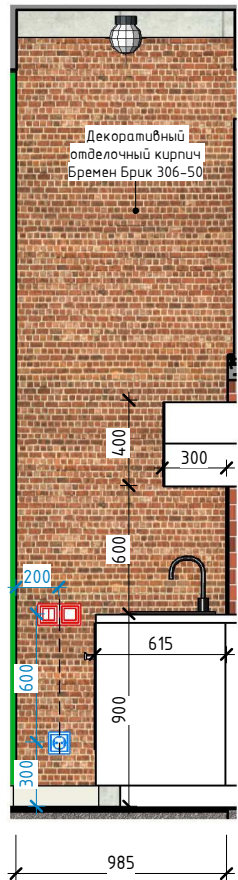

15 - 1

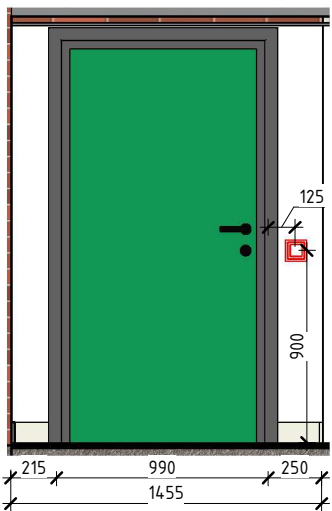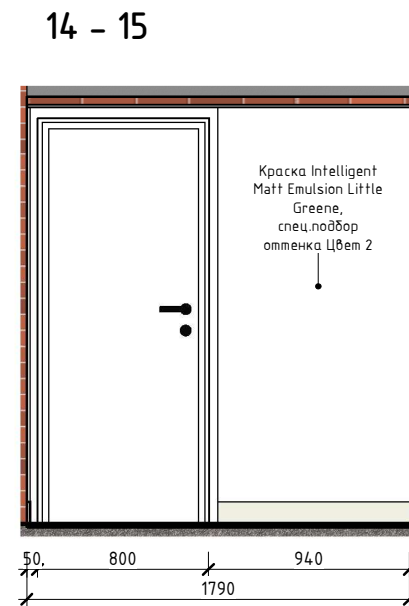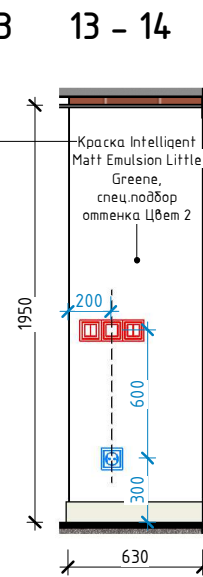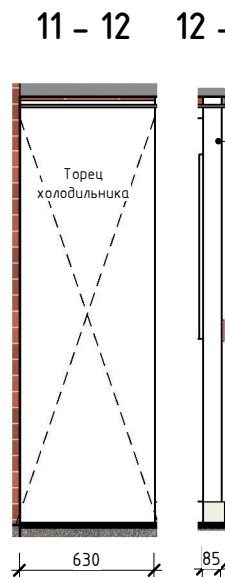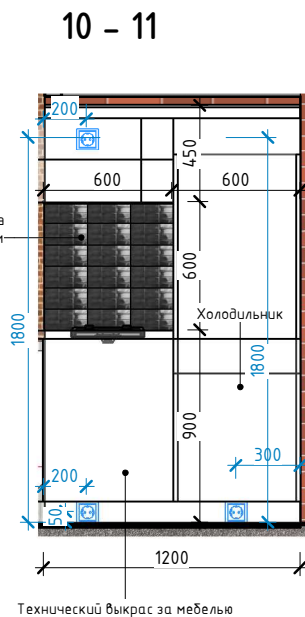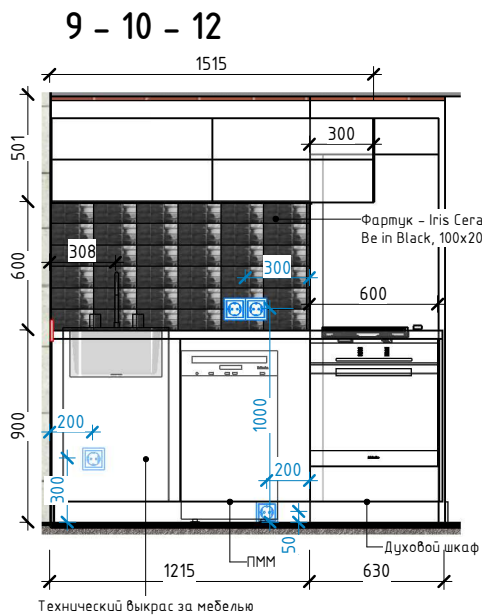

- Декоративный облицовочный кирпич - 21.87м²
Бремен Брик 306-50



- Фармык - Iris Ceramica Be in Black, - 54см.
100x200мм



- Краска Intelligent Matt Emulsion Little Greene, спец.подбор оттенка Цвѐм 1 - 12.05м²

- Краска Intelligent Matt Emulsion Little Greene, спец.подбор оттенка Цвѐм 2 - 7.59м²



- Краска Intelligent Matt Emulsion Little Greene, спец.подбор оттенка Цвем 3 - 2.99м²



- Технический выкрас за мебелью - 11.88м²








-Керамогранит VZ 01 Venezia -14шт.
неполированный 600х600мм



-Ламинат	-16.88м ²
----------	----------------------

ПРИМЕЧАНИЕ: Все количественные показатели посчитаны БЕЗ ЗАПАСА


Дизайнер		г. Москва, Нижняя Красносельская, 26.7 кв.м.	Стадия	Лист	
Клиент		Развертка Гостиной-Кухни	РП	30	

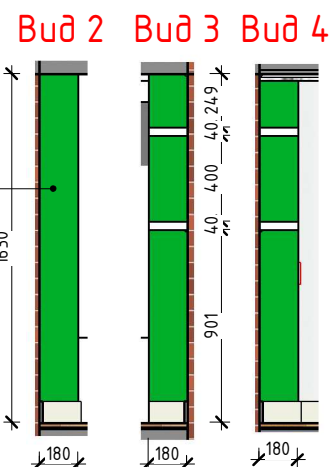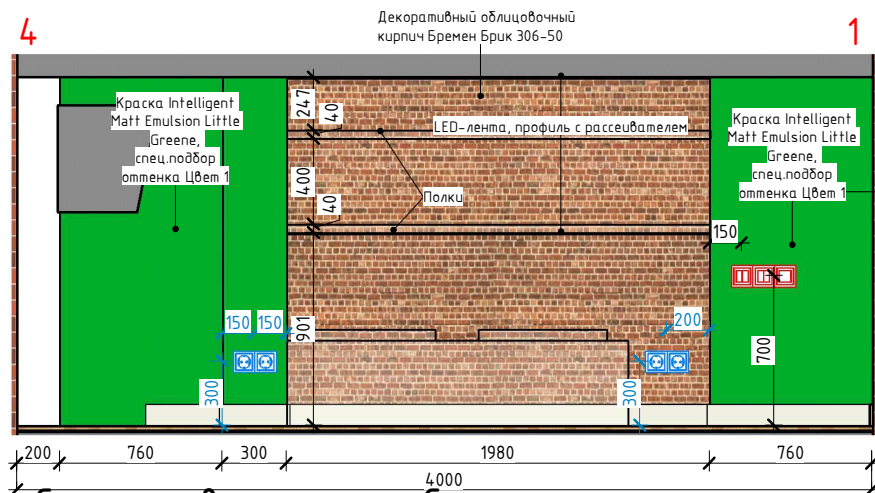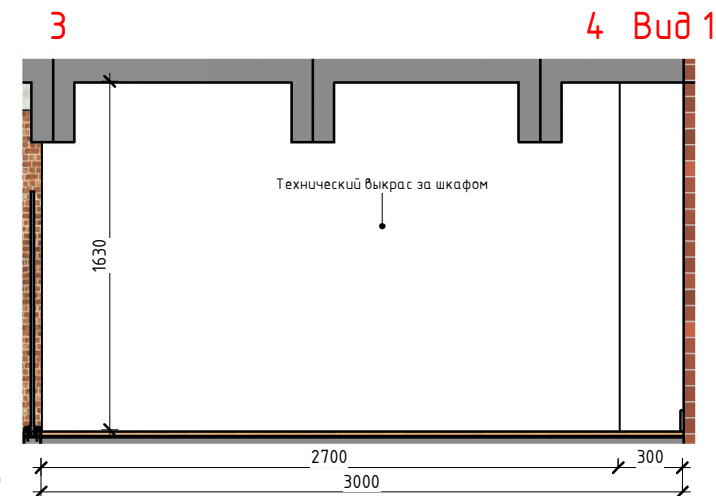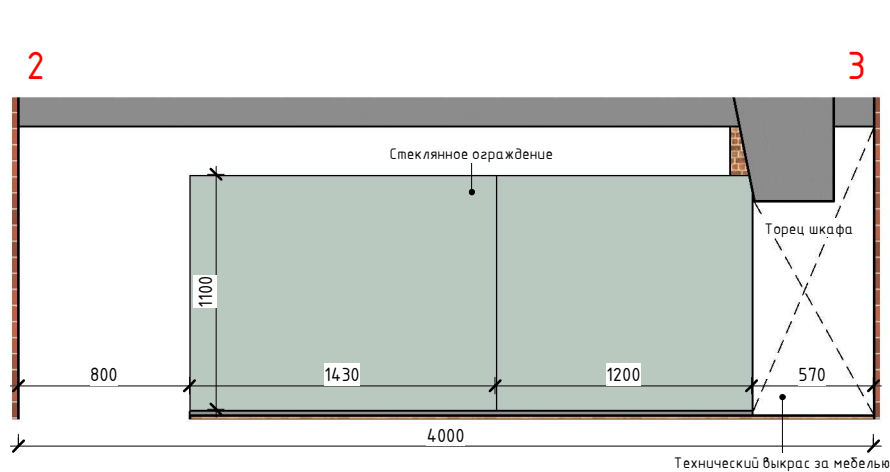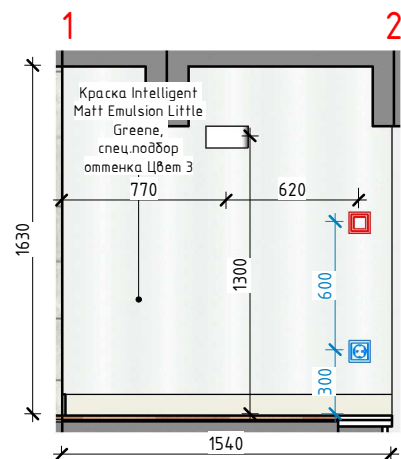

- Декоративный облицовочный кирпич Бремен Брик 306-50 - 3.22м²
- Краска Intelligent Matt Emulsion Little Greene, спец.подбор оттенка Цвет 1 - 7.89м²
- Краска Intelligent Matt Emulsion Little Greene, спец.подбор оттенка Цвет 3 - 11.11м²
- Технический выкрас за мебелью - 5.85м²
- Ламинат - 10.95м²

ПРИМЕЧАНИЕ: Все количественные показатели посчитаны БЕЗ ЗАПАСА

Схема развертки стен. Спальня

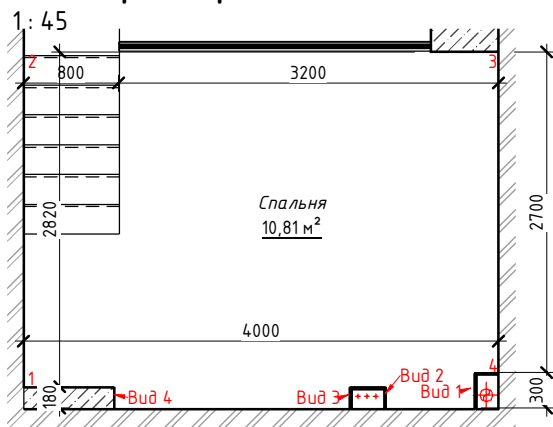

Дизайнер		г. Москва, Нижняя Красносельская, 26.7 кв.м.	Стадия	Лист
Клиент		Развертка Спальни	РП	31





Ведомость напольных покрытий	
Наименование	Площадь
Керамогранит VZ 01 Venezia неполированный 600х600мм	9,11 м ²
Ламинат	27,83 м ²

Спецификация плитусов		
Марка	Наименование	Длина, мм
ПЛ-1	Плитус	15965

Ведомость материалов потолков		
Тип	Площадь	Помещения
Гипсокартон, краска белая Beckers Beckerplast	5,35 м ²	Прихожая
Натяжной потолок	4,93 м ²	Санузел
Существующий потолок. Грунтовка по бетонному основанию	27,72 м ²	Гостиная – Кухня. Спальня

	-Настенная плитка Iris May Fern, матовая поверхность, 100х200мм	-500шт.
	-Керамогранит VZ 01 Venezia неполированный 600х600мм	-17шт.
	-Краска водостойкая Intelligent Eggshell Little Greene, спец.подбор оттенка	-5,32м ²
	-Технический выкрас за мебелью	-1,53м ²

ПРИМЕЧАНИЕ: Все количественные
показатели посчитаны БЕЗ ЗАПАСА

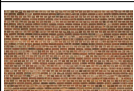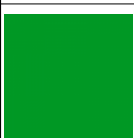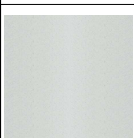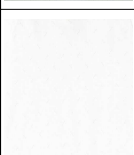Ведомость отделки стен		
Изображение	Наименование	Площадь
	Декоративный облицовочный кирпич Бремен Брик 306-50	24,84 м ²
	Краска Intelligent Matt Emulsion Little Greene, спец.подбор оттенка Цвет 1	15,02 м ²
	Краска Intelligent Matt Emulsion Little Greene, спец.подбор оттенка Цвет 2	7,43 м ²
	Краска Intelligent Matt Emulsion Little Greene, спец.подбор оттенка Цвет 3	11,11 м ²
	Краска водостойкая Intelligent Eggshell Little Greene, спец.подбор оттенка	5,32 м ²
	Технический выкрас	18,80 м ²

Количество материала указано БЕЗ ЗАПАСА

Дизайнер		г. Москва, Нижняя Красносельская, 26.7 кв.м.	Стадия	Лист	
Клиент		Ведомость рекомендуемых отделочных материалов	РП	32	